


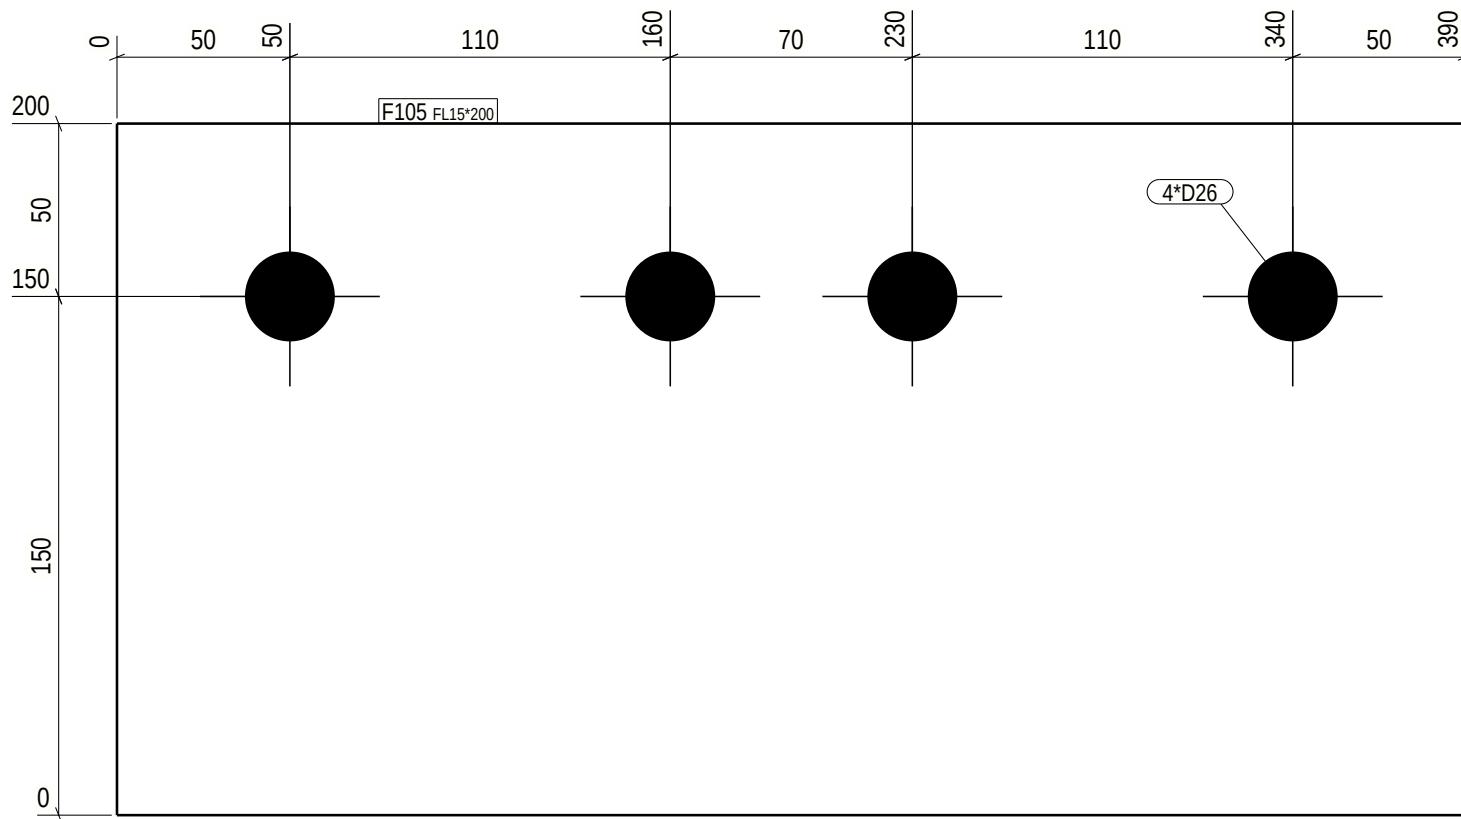

GENERAL NOTES: For your safety, check weight before handling:						
0-5kg Light 5-15kg Normal 15+kg Heavy						
MATERIAL LIST FOR PART - F105 8 PARTS REQUIRED						
POS. No.	PROFILE	No.	GRADE	L (mm)	AREA (m ²)	WEIGHT (kg)
F105	FL15*200	1	S355J2	390	0.2	9.2
TOTAL WEIGHT FOR				8	PARTS	73.5

Part list	Qty.
DR	8

Execution class: EXC 2		* o 3 0 4 8 0 - 1 *  DS <i>Skalkonstruktion</i> * WF 1 0 5 *			
No utilization on drawings = over 50%					
V-SEAM Utilization under 50% EXC 2=> Acc. to process control EXC 3=> 20% UT Utilization over 50% EXC 2=> 10% UT EXC 3=> 20% UT		PROJECT	Akkasæter Lager- og vedlikeholdshall	PHASE	1 / Phase 1
		MEMBER	Fladstål	QUANTITY:	8 PROJECT No 30480-1
		REVISION		ISSUED: 07.11.2025	DRAFTER: ZLL BIM control: SST DRAWING No. F.105