


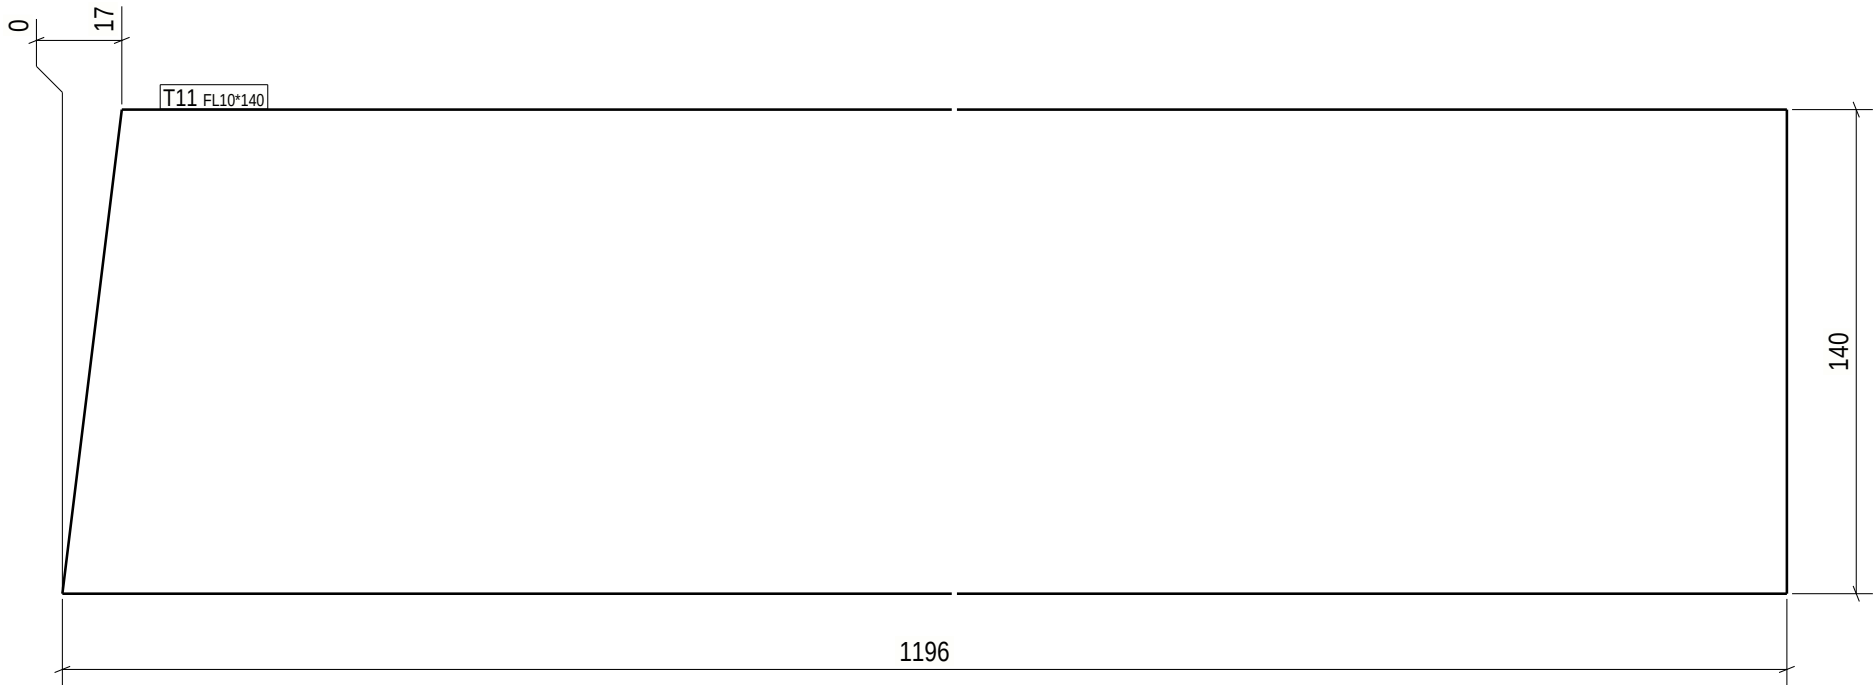

GENERAL NOTES:						
For your safety, check weight before handling:						
0-5kg Light 5-15kg Normal 15+kg Heavy						
MATERIAL LIST FOR PART - T11						
2 PARTS REQUIRED						
POS. No.	PROFILE	No.	GRADE	L (mm)	AREA (m ²)	WEIGHT (kg)
T11	FL10*140	1	S355J2	1196	0.4	13.0
TOTAL WEIGHT FOR				2	PARTS	26.1

Part list	Qty.
GS	2

Execution class: EXC 2	
No utilization on drawings = over 50%	
V-SEAM	
Utilization under 50%	
EXC 2=> Acc. to process control	
EXC 3=> 20% UT	
Utilization over 50%	
EXC 2=> 10% UT	
EXC 3=> 20% UT	

* o 3 0 4 8 0 - 1 *  DS <i>Skalkonstruktion</i> * W T 1 1 *			
PROJECT	Akkasæter Lager- og vedlikeholdshall		PHASE 1 / Phase 1
MEMBER	Opstik	QUANTITY: 2	PROJECT No 30480-1
REVISION		ISSUED: 07.11.2025	DRAWING No. T.11
		DRAFTER: ZLL	BIM control: SST