


Tekla Structures

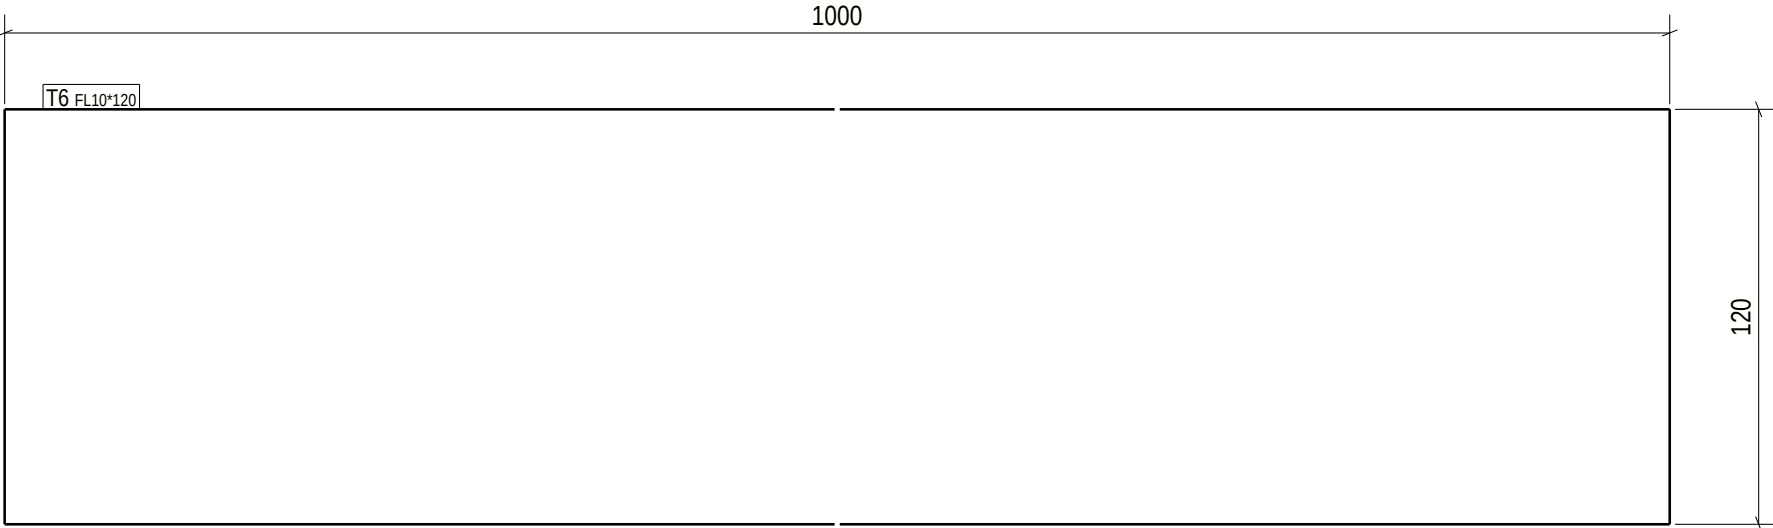

GENERAL NOTES:						
For your safety, check weight before handling:						
0-5kg Light 5-15kg Normal 15+kg Heavy						
MATERIAL LIST FOR PART - T6				17 PARTS REQUIRED		
POS. No.	PROFILE	No.	GRADE	L (mm)	AREA (m ²)	WEIGHT (kg)
T6	FL10*120	1	S355J2	1000	0.3	9.4
TOTAL WEIGHT FOR				17	PARTS	160.1

Part list	Qty.
GS	17

Execution class: EXC 2		* o 3 0 4 8 0 - 1 *  DS <i>Stålkonstruktion</i> * WT 6 *			
No utilization on drawings = over 50%					
V-SEAM Utilization under 50% EXC 2=> Acc. to process control EXC 3=> 20% UT Utilization over 50% EXC 2=> 10% UT EXC 3=> 20% UT		PROJECT	Akkasæter Lager- og vedlikeholdshall		PHASE 1 / Phase 1
		MEMBER	Opstik		QUANTITY: 17 PROJECT No 30480-1
		REVISION		ISSUED: 07.11.2025	DRAFTER: ZLL BIM control: SST DRAWING No. T.6