


Tekla Structures

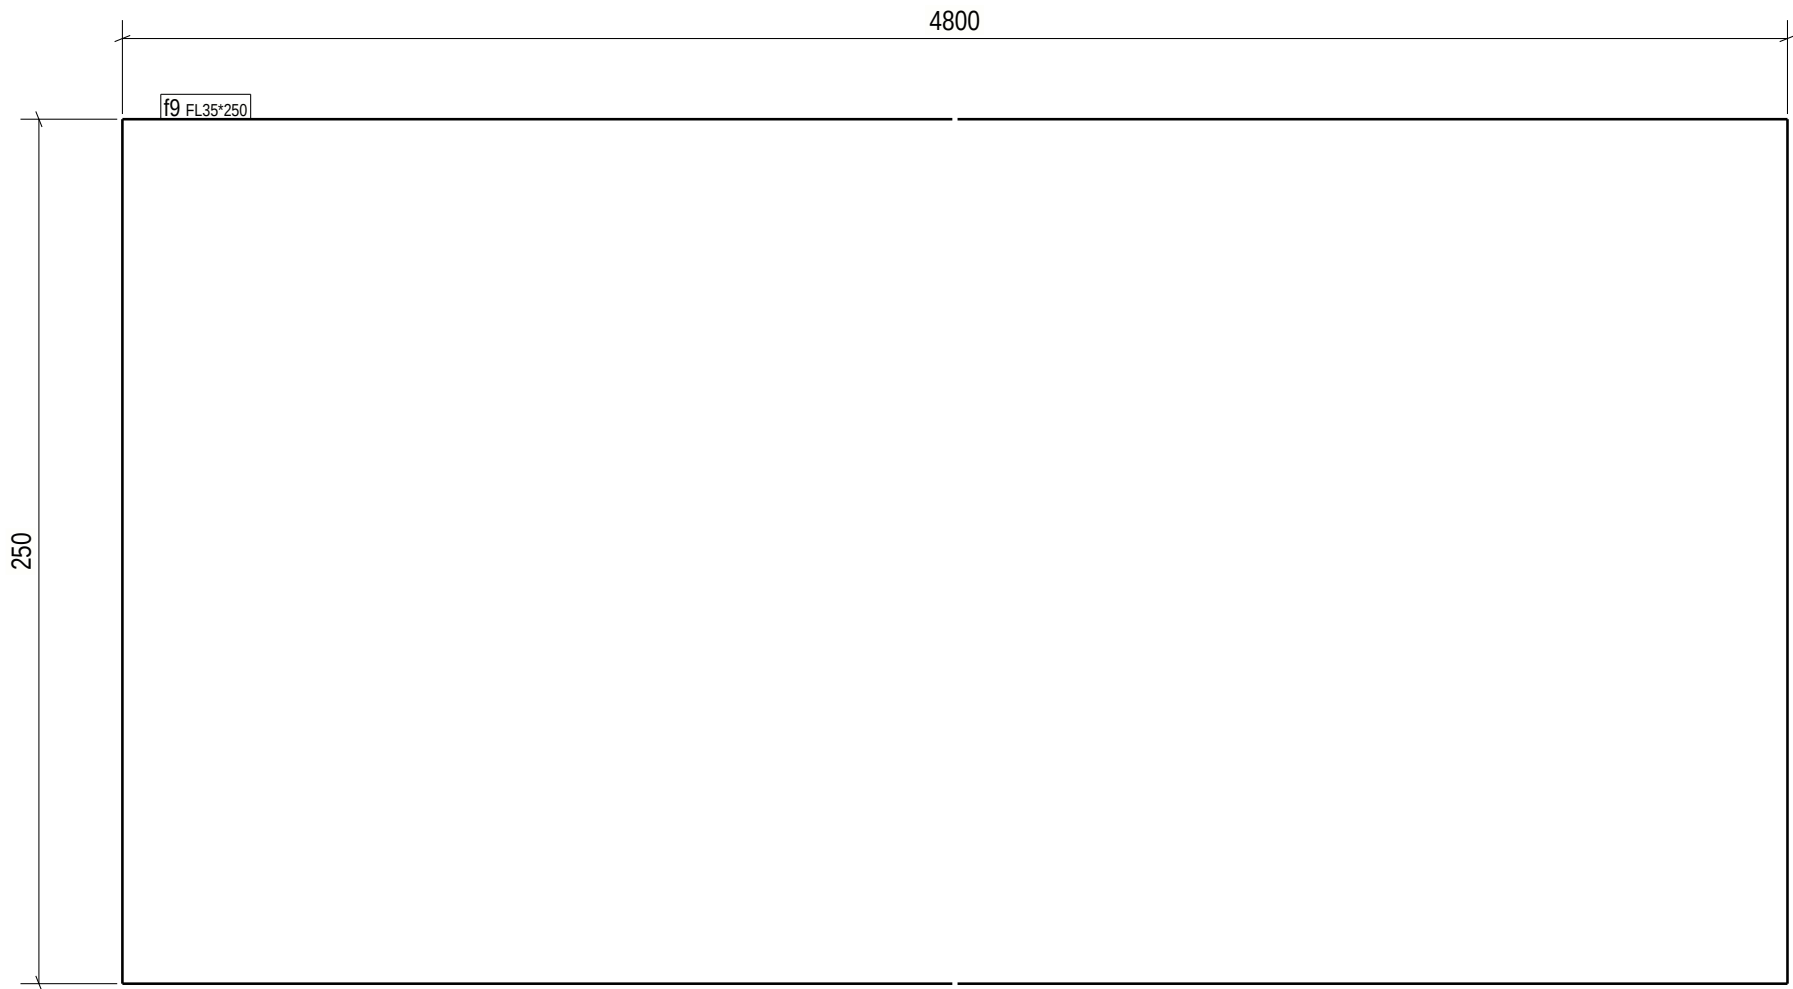

|                                                |          |     |        |        |                        |             |
|------------------------------------------------|----------|-----|--------|--------|------------------------|-------------|
| GENERAL NOTES:                                 |          |     |        |        |                        |             |
| For your safety, check weight before handling: |          |     |        |        |                        |             |
| 0-5kg Light    5-15kg Normal    15+kg Heavy    |          |     |        |        |                        |             |
| MATERIAL LIST FOR PART - f9                    |          |     |        |        |                        |             |
| 1 PARTS REQUIRED                               |          |     |        |        |                        |             |
| POS. No.                                       | PROFILE  | No. | GRADE  | L (mm) | AREA (m <sup>2</sup> ) | WEIGHT (kg) |
| f9                                             | FL35*250 | 1   | S355J2 | 4800   | 2.8                    | 329.7 !!    |
| TOTAL WEIGHT FOR                               |          | 1   | PARTS  | 329.7  |                        |             |

|           |      |
|-----------|------|
| Part list | Qty. |
| OB        | 1    |

|   |  |   |                                      |  |                                                  |
|---|--|---|--------------------------------------|--|--------------------------------------------------|
| Execution class: EXC 2   |  | * o 3 0 4 8 0 - 1 *  <b>DS</b> <i>Stålkonstruktion</i> * W f 9 * |                                      |  |                                                  |
| No utilization on drawings = over 50%   |  |   |                                      |  |                                                  |
| V-SEAM<br>Utilization under 50%<br>EXC 2=> Acc. to process control<br>EXC 3=> 20% UT<br>Utilization over 50%<br>EXC 2=> 10% UT<br>EXC 3=> 20% UT |  | PROJECT   | Akkasæter Lager- og vedlikeholdshall |  | PHASE 1 / Phase 1                                |
|   |  | MEMBER   | HSQ                                  |  | QUANTITY: 1 PROJECT No 30480-1                   |
|   |  | REVISION   | ISSUED: 07.11.2025                   |  | DRAFTER: ZLL<br>BIM control: SST DRAWING No. f.9 |