


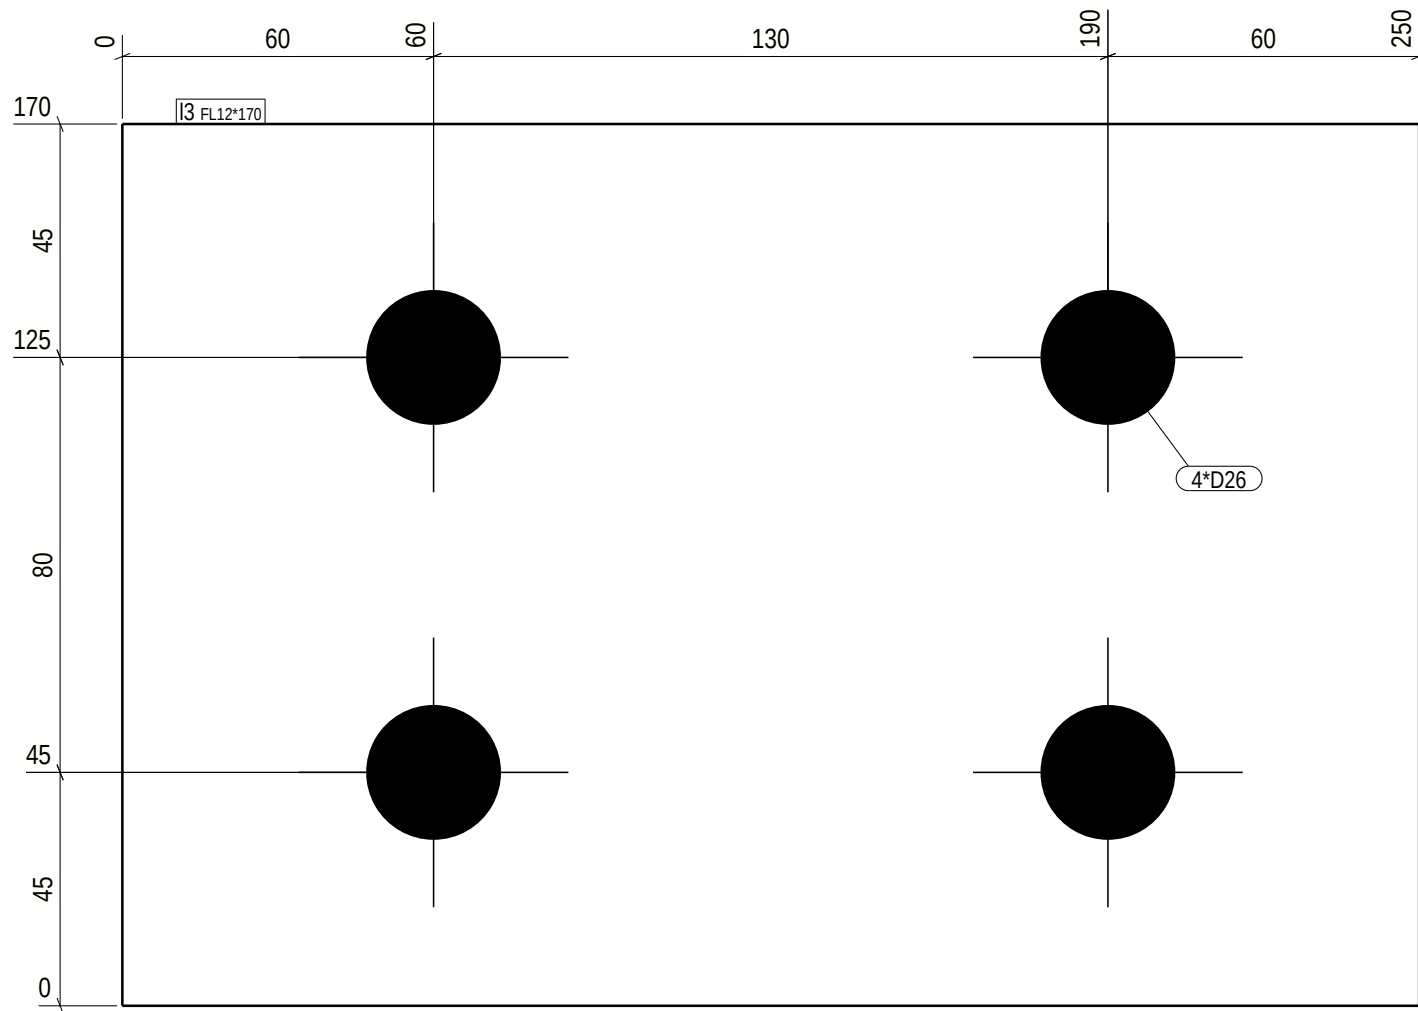

GENERAL NOTES:						
For your safety, check weight before handling:						
0-5kg Light 5-15kg Normal 15+kg Heavy						
MATERIAL LIST FOR PART - I3				32 PARTS REQUIRED		
POS. No.	PROFILE	No.	GRADE	L (mm)	AREA (m ²)	WEIGHT (kg)
I3	FL12*170	1	S355J2	250	0.1	4.0
TOTAL WEIGHT FOR				32 PARTS	128.1	

Part list	Qty.
LP	32

Execution class: EXC 2	
No utilization on drawings = over 50%	
V-SEAM	
Utilization under 50%	
EXC 2=> Acc. to process control	
EXC 3=> 20% UT	
Utilization over 50%	
EXC 2=> 10% UT	
EXC 3=> 20% UT	

* o 3 0 4 8 0 - 1 *				 DS <i>Stålkonstruktion</i>		* W I 3 *	
PROJECT	Akkasæter Lager- og vedlikeholdshall				PHASE	1 / Phase 1	
MEMBER	Løsdele				QUANTITY:	32	PROJECT No 30480-1
REVISION		ISSUED:	07.11.2025	DRAFTER:	ZLL		DRAWING No. I.3
		BIM control:	SST				