


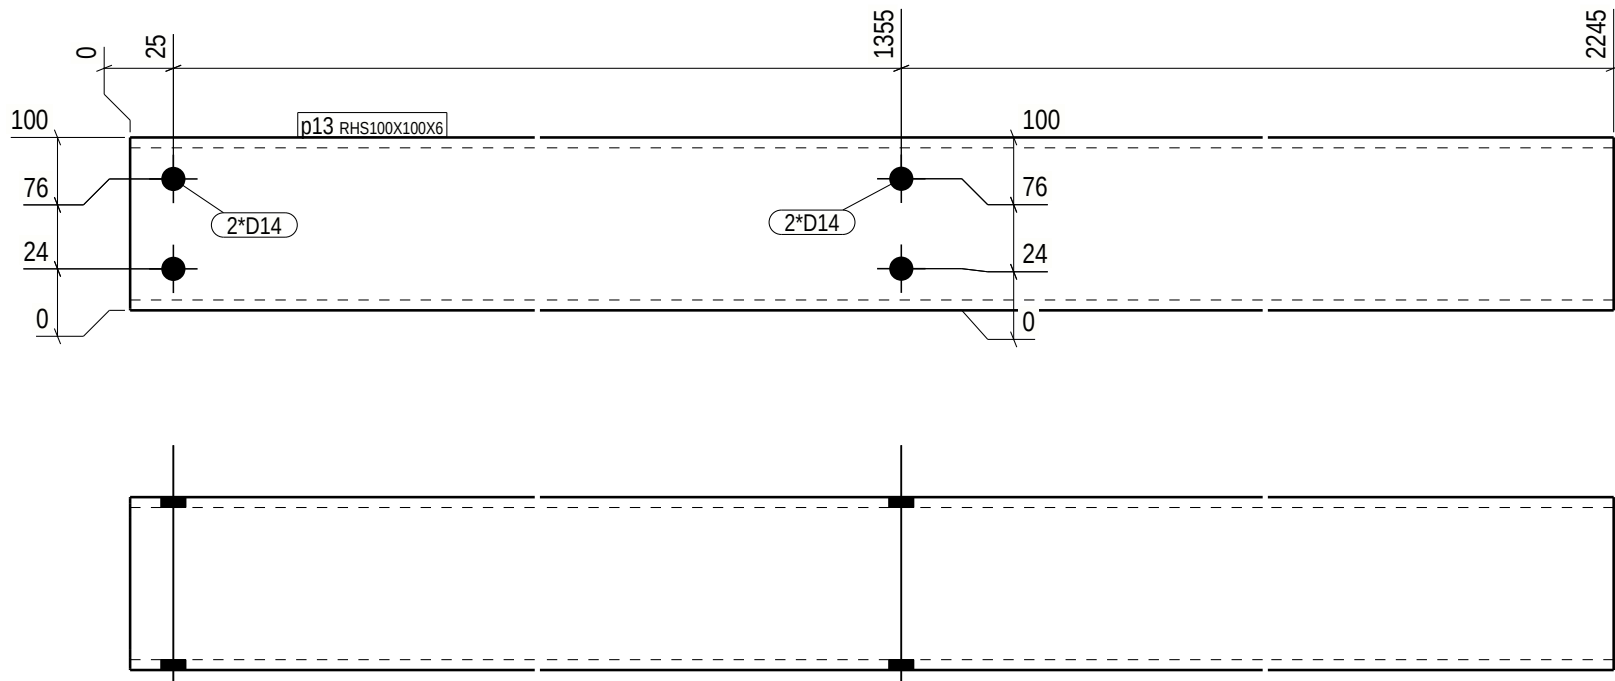

GENERAL NOTES:

For your safety, check weight before handling:
0-5kg Light 5-15kg Normal 15+kg Heavy

MATERIAL LIST FOR PART - p13

1 PARTS REQUIRED

POS. No.	PROFILE	No.	GRADE	L (mm)	AREA (m ²)	WEIGHT (kg)
p13	RHS100X100X6	1	S355J2H	2245	0.9	38.0 !!
TOTAL WEIGHT FOR				1	PARTS	38.0

Execution class: EXC 2

No utilization on drawings = over 50%

V-SEAM
Utilization under 50%
EXC 2=> Acc. to process control
EXC 3=> 20% UT
Utilization over 50%
EXC 2=> 10% UT
EXC 3=> 20% UT

Part list	Qty.
OP	1

* o 3 0 4 8 0 - 1 *



DS Steelkonstruktion

* W p 1 3 *

PROJECT	Akkasæter Lager- og vedlikeholdshall		PHASE	1 / Phase 1	
MEMBER	Portomfatning		QUANTITY:	1	PROJECT No
REVISION			ISSUED:	07.11.2025	30480-1
		DRAFTER: ZLL		BIM control: SST	DRAWING No.
				p.13	