


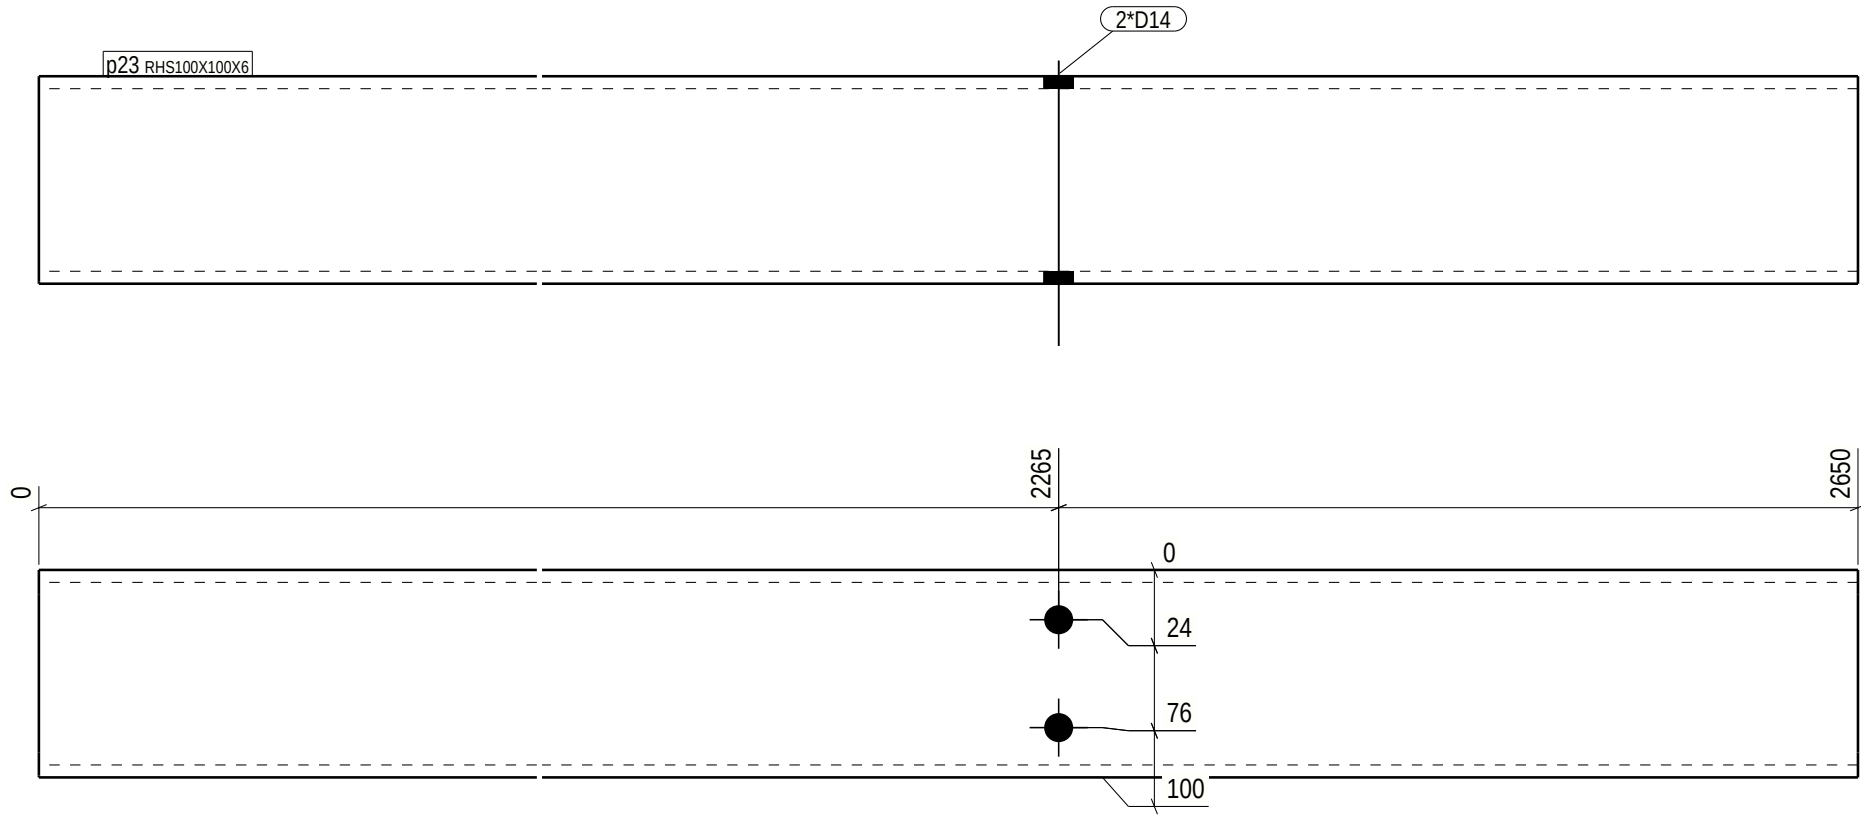

GENERAL NOTES:		For your safety, check weight before handling: 0-5kg Light 5-15kg Normal 15+kg Heavy				
MATERIAL LIST FOR PART - p23			1 PARTS REQUIRED			
POS. No.	PROFILE	No.	GRADE	L (mm)	AREA (m ²)	WEIGHT (kg)
p23	RHS100X100X6	1	S355J2H	2650	1.0	44.8 !!
TOTAL WEIGHT FOR				1	PARTS	44.8

Part list	Qty.
OP	1

Execution class: EXC 2		* o 3 0 4 8 0 - 1 *  DS <i>Skalkonstruktion</i> * W p 2 3 *			
No utilization on drawings = over 50%		PROJECT Akkasæter Lager- og vedlikeholdshall		PHASE 1 / Phase 1	
V-SEAM Utilization under 50% EXC 2=> Acc. to process control EXC 3=> 20% UT Utilization over 50% EXC 2=> 10% UT EXC 3=> 20% UT		MEMBER Portomfatning		QUANTITY: 1 PROJECT No 30480-1	
		REVISION		ISSUED: 07.11.2025 DRAFTER: ZLL BIM control: SST DRAWING No. p.23	