


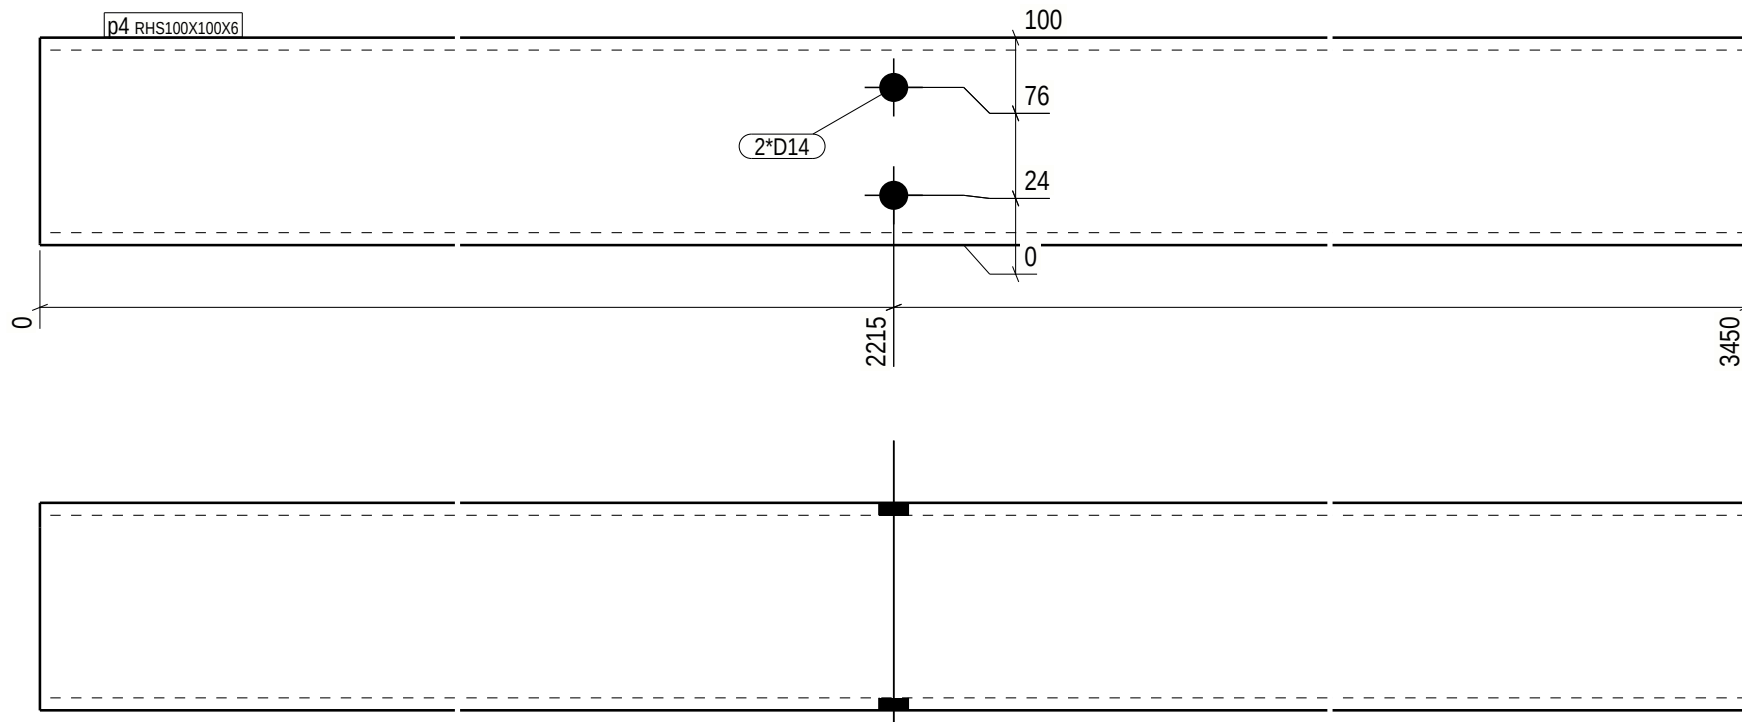

GENERAL NOTES:

For your safety, check weight before handling:
0-5kg Light 5-15kg Normal 15+kg Heavy

MATERIAL LIST FOR PART - p4

2 PARTS REQUIRED

POS. No.	PROFILE	No.	GRADE	L (mm)	AREA (m ²)	WEIGHT (kg)
p4	RHS100X100X6	1	S355J2H	3450	1.3	58.4 !!

TOTAL WEIGHT FOR 2 PARTS 116.7

Part list	Qty.
OP	2

Execution class: EXC 2

No utilization on drawings = over 50%

V-SEAM
Utilization under 50%
EXC 2=> Acc. to process control
EXC 3=> 20% UT
Utilization over 50%
EXC 2=> 10% UT
EXC 3=> 20% UT

* o 3 0 4 8 0 - 1 *



DS Skalkonstruktion * W p 4 *

PROJECT	Akkasæter Lager- og vedlikeholdshall		PHASE	1 / Phase 1	
MEMBER	Portomfatning		QUANTITY:	2	PROJECT No 30480-1
REVISION		ISSUED: 07.11.2025	DRAFTER: BIM control:	ZLL SST	DRAWING No. p.4