


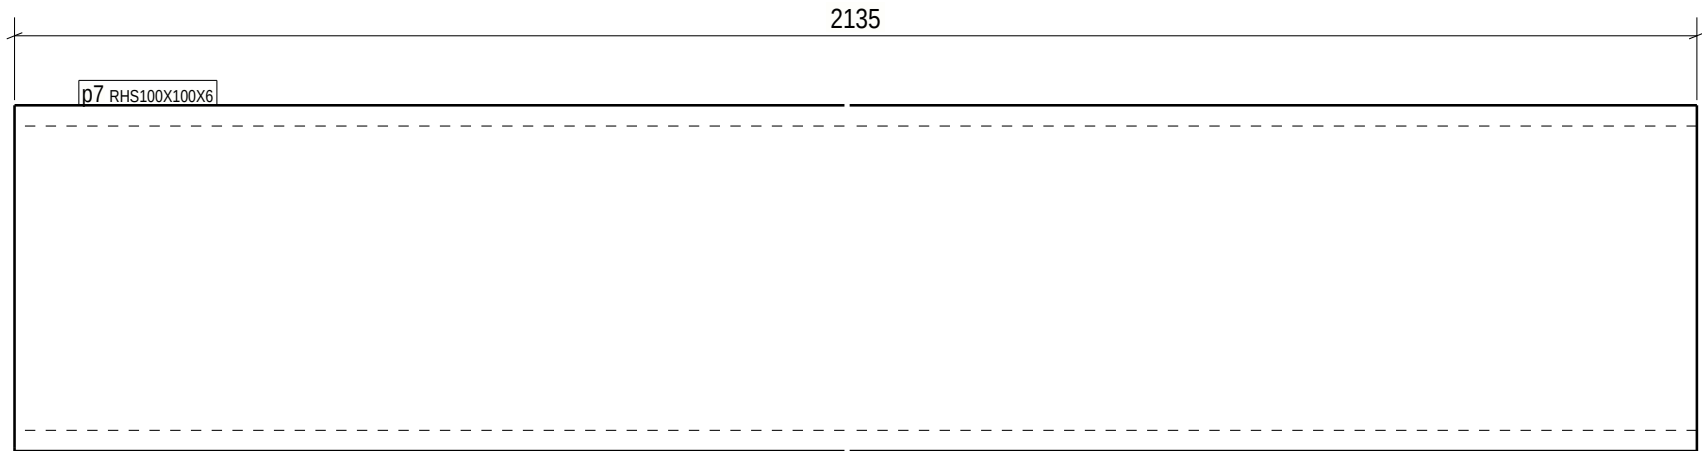

GENERAL NOTES:		For your safety, check weight before handling: 0-5kg Light 5-15kg Normal 15+kg Heavy				
MATERIAL LIST FOR PART - p7			2 PARTS REQUIRED			
POS. No.	PROFILE	No.	GRADE	L (mm)	AREA (m ²)	WEIGHT (kg)
p7	RHS100X100X6	1	S355J2H	2135	0.8	36.1 !!
TOTAL WEIGHT FOR			2	PARTS	72.2	

Execution class: EXC 2		* o 3 0 4 8 0 - 1 *  DS <i>Skalkonstruktion</i> * W p 7 *			
No utilization on drawings = over 50%		PROJECT	Akkasæter Lager- og vedlikeholdshall	PHASE	1 / Phase 1
V-SEAM Utilization under 50% EXC 2=> Acc. to process control EXC 3=> 20% UT		MEMBER	Portomfatning	QUANTITY:	2 PROJECT No 30480-1
Utilization over 50% EXC 2=> 10% UT EXC 3=> 20% UT		REVISION	ISSUED: 07.11.2025	DRAFTER: BIM control:	ZLL SST DRAWING No. p.7