


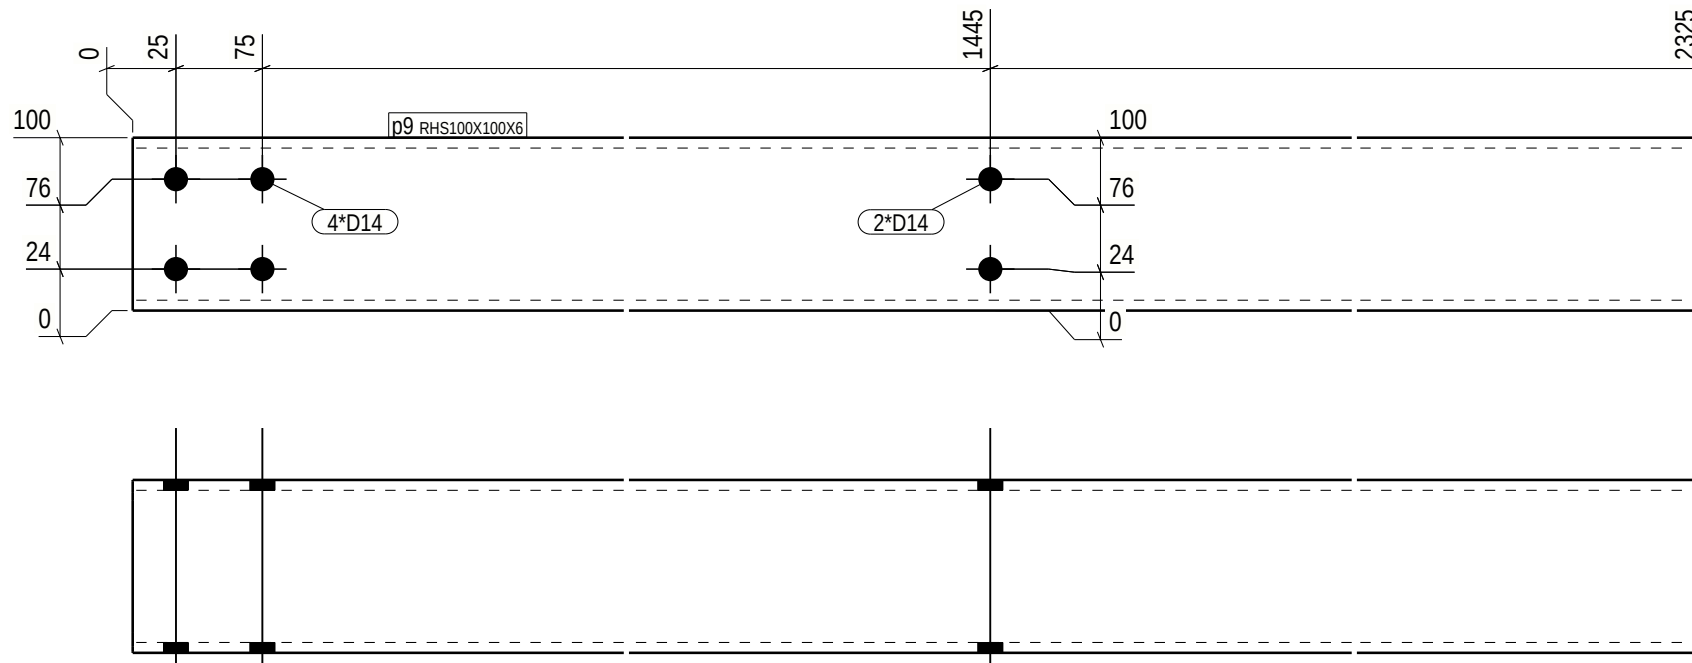

GENERAL NOTES:						
For your safety, check weight before handling:						
0-5kg Light 5-15kg Normal 15+kg Heavy						
MATERIAL LIST FOR PART - p9				1 PARTS REQUIRED		
POS. No.	PROFILE	No.	GRADE	L (mm)	AREA (m ²)	WEIGHT (kg)
p9	RHS100X100X6	1	S355J2H	2325	0.9	39.3 !!
TOTAL WEIGHT FOR				1	PARTS	39.3

Part list	Qty.
OP	1

Execution class: EXC 2		* o 3 0 4 8 0 - 1 *  DS <i>Skalkonstruktion</i> * W p 9 *			
No utilization on drawings = over 50%					
V-SEAM Utilization under 50% EXC 2=> Acc. to process control EXC 3=> 20% UT Utilization over 50% EXC 2=> 10% UT EXC 3=> 20% UT		PROJECT	Akkasæter Lager- og vedlikeholdshall	PHASE	1 / Phase 1
		MEMBER	Portomfatning	QUANTITY:	1
		REVISION		ISSUED:	07.11.2025
				DRAFTER:	ZLL
				BIM control:	SST
				PROJECT No	30480-1
				DRAWING No.	p.9