


Tekla Structures

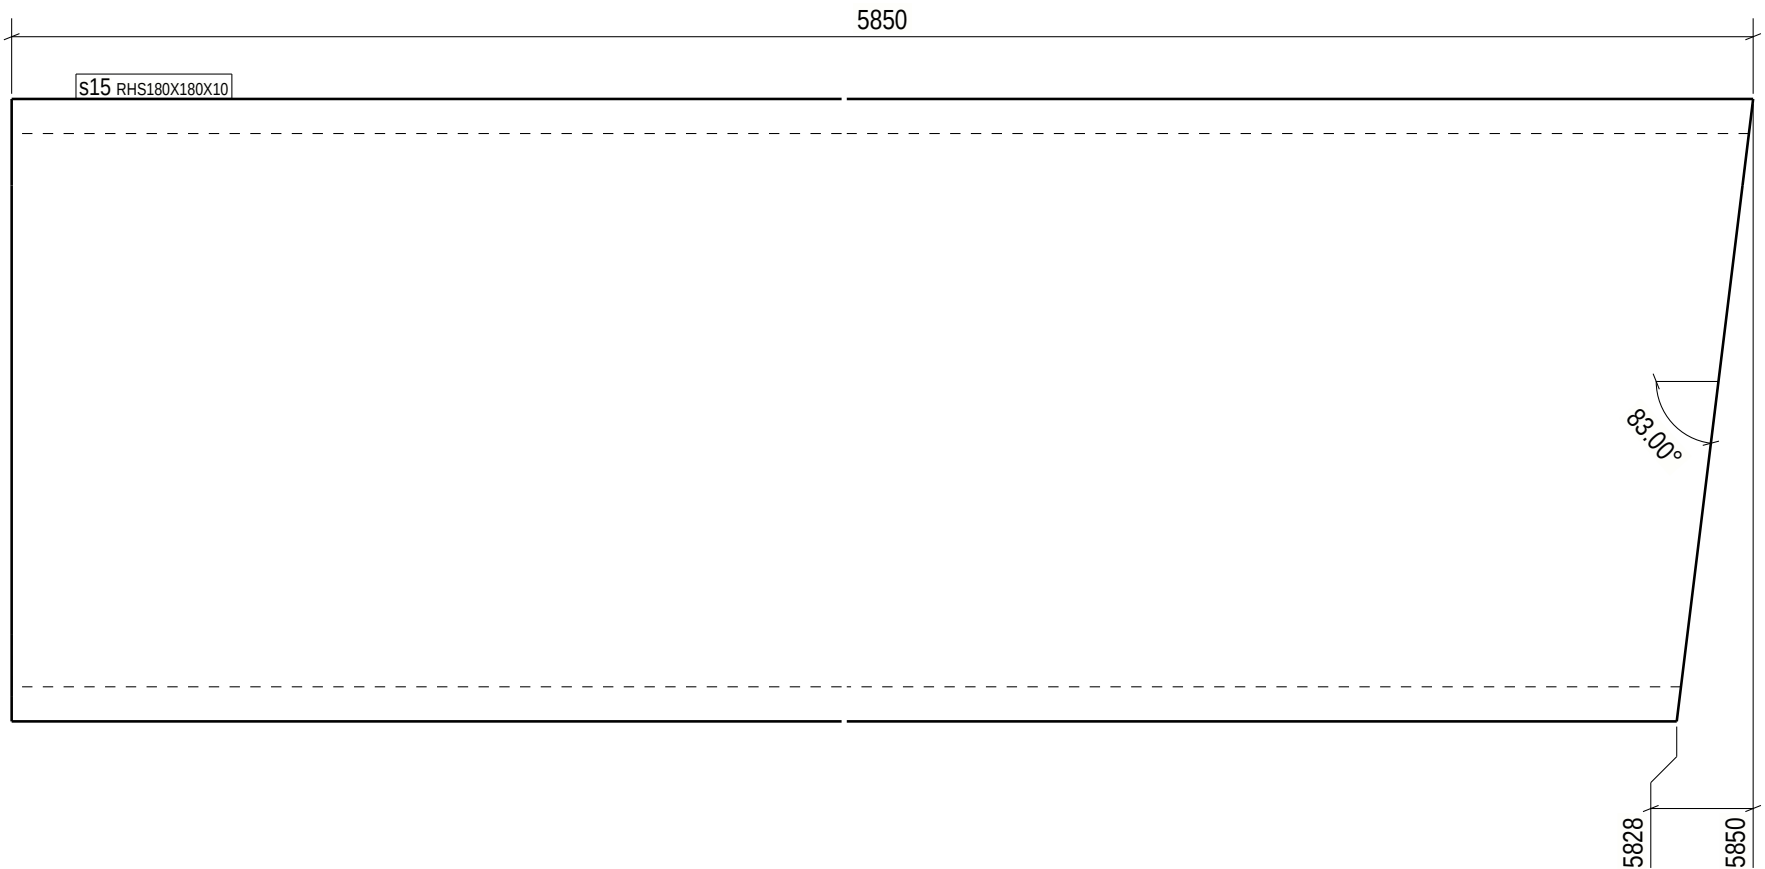

GENERAL NOTES:						
For your safety, check weight before handling:						
0-5kg Light 5-15kg Normal 15+kg Heavy						
MATERIAL LIST FOR PART - S15				1 PARTS REQUIRED		
POS. No.	PROFILE	No.	GRADE	L (mm)	AREA (m ²)	WEIGHT (kg)
s15	RHS180X180X10	1	S355J2H	5850	4.0	294.5 !!
TOTAL WEIGHT FOR				1	PARTS	294.5

Part list	Qty.
GS	1

Execution class: EXC 2		* o 3 0 4 8 0 - 1 *  DS <i>Skalkonstruktion</i> * W s 1 5 *					
No utilization on drawings = over 50%		PROJECT Akkasæter Lager- og vedlikeholdshall				PHASE 1 / Phase 1	
V-SEAM Utilization under 50% EXC 2=> Acc. to process control EXC 3=> 20% UT Utilization over 50% EXC 2=> 10% UT EXC 3=> 20% UT		MEMBER Søje		QUANTITY: 1		PROJECT No 30480-1	
		REVISION		ISSUED: 07.11.2025		DRAFTER: ZLL BIM control: SST	
						DRAWING No. s.15	