


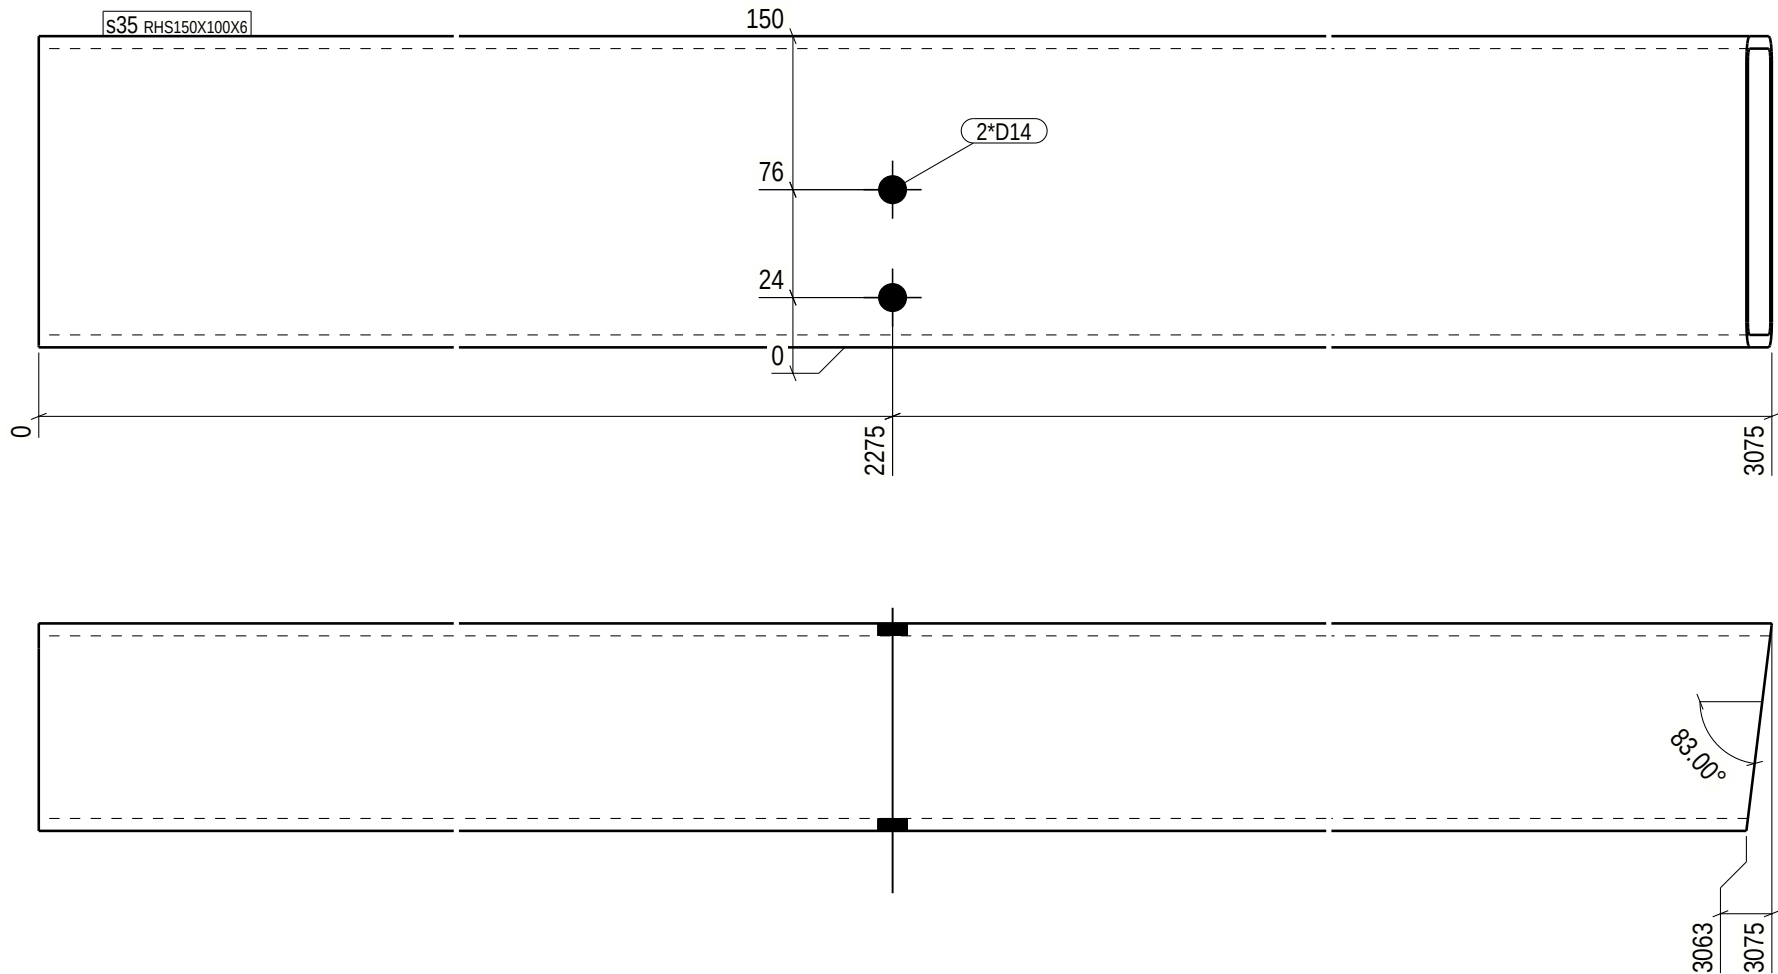

GENERAL NOTES:

For your safety, check weight before handling:
0-5kg Light 5-15kg Normal 15+kg Heavy

MATERIAL LIST FOR PART - S35

1 PARTS REQUIRED

POS. No.	PROFILE	No.	GRADE	L (mm)	AREA (m ²)	WEIGHT (kg)
s35	RHS150X100X6	1	S355J2H	3075	1.5	66.4 !!
TOTAL WEIGHT FOR				1	PARTS	66.4

Execution class: EXC 2

No utilization on drawings = over 50%

V-SEAM
Utilization under 50%
EXC 2=> Acc. to process control
EXC 3=> 20% UT
Utilization over 50%
EXC 2=> 10% UT
EXC 3=> 20% UT

Part list	Qty.
GS	1

* o 3 0 4 8 0 - 1 *



DS Steelkonstruktion

* W s 3 5 *

PROJECT	Akkasæter Lager- og vedlikeholdshall		PHASE	1 / Phase 1	
MEMBER	Søjle		QUANTITY:	1	PROJECT No 30480-1
REVISION	ISSUED: 07.11.2025		DRAFTER:	ZLL	DRAWING No. s.35
		BIM control:		SST	