


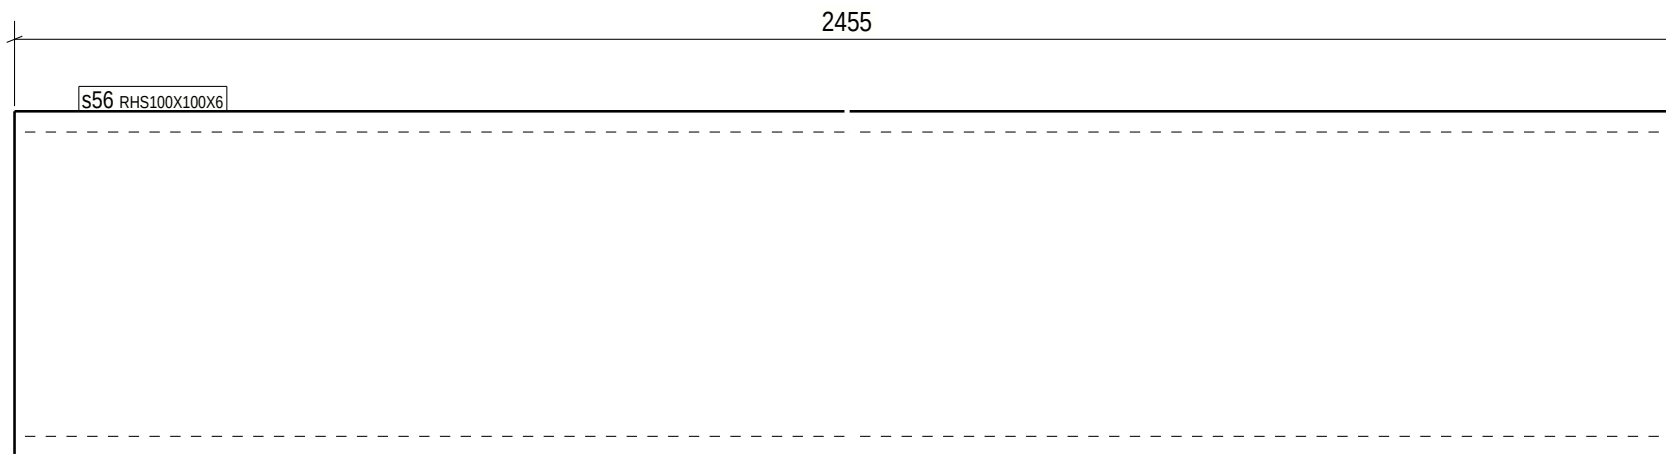

GENERAL NOTES:						
For your safety, check weight before handling:						
0-5kg Light 5-15kg Normal 15+kg Heavy						
MATERIAL LIST FOR PART - S56						
3 PARTS REQUIRED						
POS. No.	PROFILE	No.	GRADE	L (mm)	AREA (m ²)	WEIGHT (kg)
s56	RHS100X100X6	1	S355J2H	2455	0.9	41.5 !!
TOTAL WEIGHT FOR				3	PARTS	124.6

Execution class: EXC 2	
No utilization on drawings = over 50%	
V-SEAM	
Utilization under 50%	
EXC 2=> Acc. to process control	
EXC 3=> 20% UT	
Utilization over 50%	
EXC 2=> 10% UT	
EXC 3=> 20% UT	
Part list	Qty.
GS	3

* o 3 0 4 8 0 - 1 *  DS <i>Stalkonstruktion</i> * W s 5 6 *			
PROJECT	Akkasæter Lager- og vedlikeholdshall		PHASE 1 / Phase 1
MEMBER	Søje	QUANTITY: 3	PROJECT No 30480-1
REVISION		ISSUED: 07.11.2025	DRAWING No. s.56
		DRAFTER: ZLL	BIM control: SST