


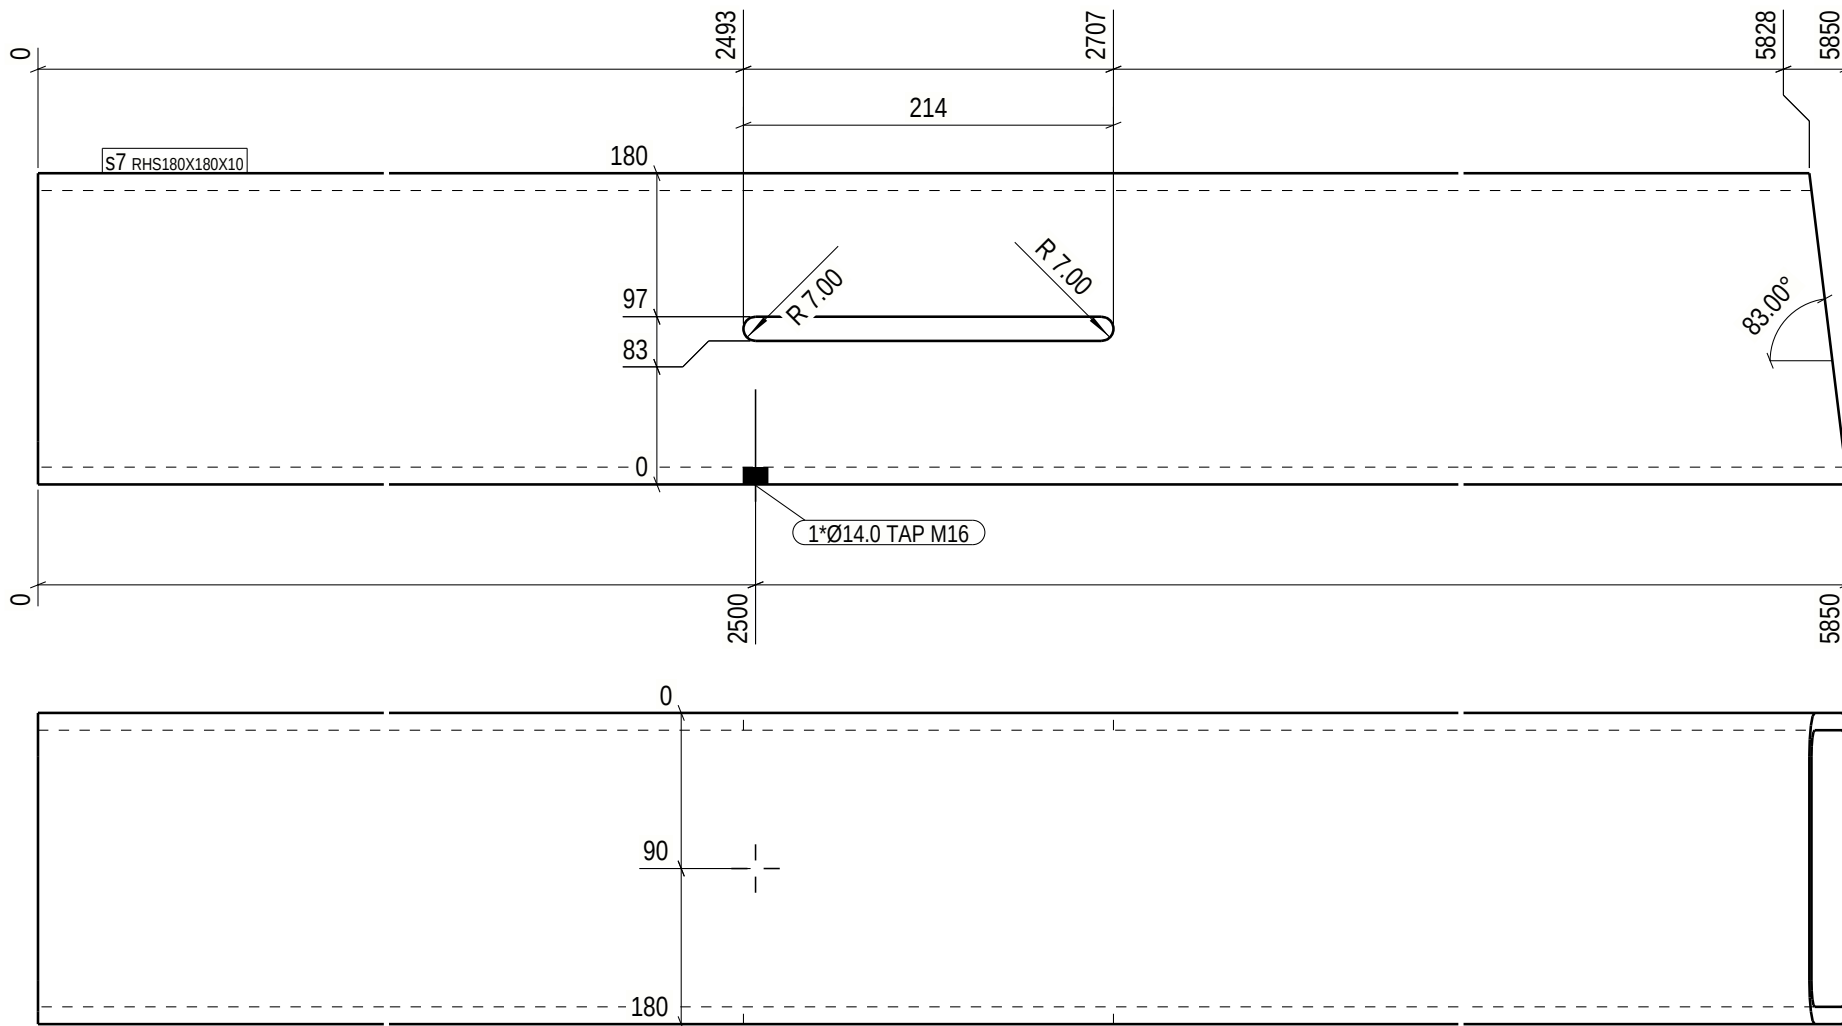

|                                                |               |     |         |                  |                        |             |
|------------------------------------------------|---------------|-----|---------|------------------|------------------------|-------------|
| GENERAL NOTES:                                 |               |     |         |                  |                        |             |
| For your safety, check weight before handling: |               |     |         |                  |                        |             |
| 0-5kg Light    5-15kg Normal    15+kg Heavy    |               |     |         |                  |                        |             |
| MATERIAL LIST FOR PART - S7                    |               |     |         | 1 PARTS REQUIRED |                        |             |
| POS. No.                                       | PROFILE       | No. | GRADE   | L (mm)           | AREA (m <sup>2</sup> ) | WEIGHT (kg) |
| s7                                             | RHS180X180X10 | 1   | S355J2H | 5850             | 4.0                    | 294.0 !!    |
| TOTAL WEIGHT FOR                               |               |     |         | 1                | PARTS                  | 294.0       |

|           |      |
|-----------|------|
| Part list | Qty. |
| GS        | 1    |

|   |  |   |                                      |                    |                                                  |
|---|--|---|--------------------------------------|--------------------|--------------------------------------------------|
| Execution class: EXC 2   |  | * o 3 0 4 8 0 - 1 *  DS <i>Skalkonstruktion</i> * W s 7 * |                                      |                    |                                                  |
| No utilization on drawings = over 50%   |  |   |                                      |                    |                                                  |
| V-SEAM<br>Utilization under 50%<br>EXC 2=> Acc. to process control<br>EXC 3=> 20% UT<br>Utilization over 50%<br>EXC 2=> 10% UT<br>EXC 3=> 20% UT |  | PROJECT   | Akkasæter Lager- og vedlikeholdshall | PHASE              | 1 / Phase 1                                      |
|   |  | MEMBER   | Søjle                                | QUANTITY:          | 1 PROJECT No 30480-1                             |
|   |  | REVISION   |                                      | ISSUED: 07.11.2025 | DRAFTER: ZLL<br>BIM control: SST DRAWING No. S.7 |