


Tekla Structures



|                                                |         |     |        |                  |                        |             |
|------------------------------------------------|---------|-----|--------|------------------|------------------------|-------------|
| GENERAL NOTES:                                 |         |     |        |                  |                        |             |
| For your safety, check weight before handling: |         |     |        |                  |                        |             |
| 0-5kg Light    5-15kg Normal    15+kg Heavy    |         |     |        |                  |                        |             |
| MATERIAL LIST FOR PART - x22                   |         |     |        | 1 PARTS REQUIRED |                        |             |
| POS. No.                                       | PROFILE | No. | GRADE  | L (mm)           | AREA (m <sup>2</sup> ) | WEIGHT (kg) |
| x22                                            | D30     | 1   | S355J2 | 5077             | 0.5                    | 26.9 !!     |
| TOTAL WEIGHT FOR                               |         |     |        | 1                | PARTS                  | 26.9        |

|           |      |
|-----------|------|
| Part list | Qty. |
| VX        | 1    |

|   |  |   |                                      |                       |                                                               |
|---|--|---|--------------------------------------|-----------------------|---------------------------------------------------------------|
| Execution class: EXC 2   |  | * o 3 0 4 8 0 - 1 *  <b>DS</b> <i>Skalkonstruktion</i> * W x 2 2 * |                                      |                       |                                                               |
| No utilization on drawings = over 50%   |  |   |                                      |                       |                                                               |
| V-SEAM<br>Utilization under 50%<br>EXC 2=> Acc. to process control<br>EXC 3=> 20% UT<br>Utilization over 50%<br>EXC 2=> 10% UT<br>EXC 3=> 20% UT |  | PROJECT   | Akkasæter Lager- og vedlikeholdshall |                       | PHASE    1 / Phase 1                                          |
|   |  | MEMBER   | Vind-X                               |                       | QUANTITY:    1    PROJECT No    30480-1                       |
|   |  | REVISION   |                                      | ISSUED:    07.11.2025 | DRAFTER:    ZLL<br>BIM control:    SST    DRAWING No.    x.22 |