


Tekla Structures



GENERAL NOTES:						
For your safety, check weight before handling:						
0-5kg Light 5-15kg Normal 15+kg Heavy						
MATERIAL LIST FOR PART - x25				4 PARTS REQUIRED		
POS. No.	PROFILE	No.	GRADE	L (mm)	AREA (m ²)	WEIGHT (kg)
x25	D30	1	S355J2	5817	0.5	30.8 !!
TOTAL WEIGHT FOR				4	PARTS	123.3

Part list		Qty.
VX		4

Execution class: EXC 2	
No utilization on drawings = over 50%	
V-SEAM	
Utilization under 50%	
EXC 2=> Acc. to process control	
EXC 3=> 20% UT	
Utilization over 50%	
EXC 2=> 10% UT	
EXC 3=> 20% UT	

* o 3 0 4 8 0 - 1 *  DS <i>Skalkonstruktion</i> * W x 2 5 *			
PROJECT	Akkasæter Lager- og vedlikeholdshall		PHASE 1 / Phase 1
MEMBER	Vind-X	QUANTITY: 4	PROJECT No 30480-1
REVISION		ISSUED: 07.11.2025	DRAWING No. x.25
		DRAFTER: ZLL	
		BIM control: SST	