
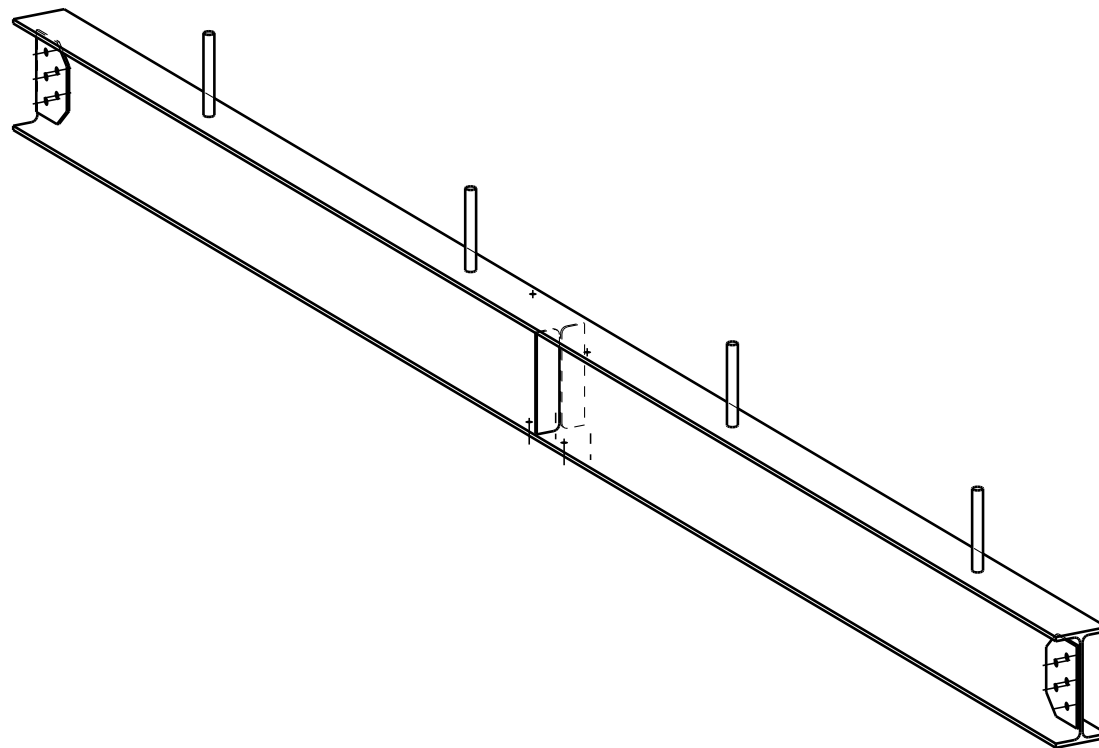


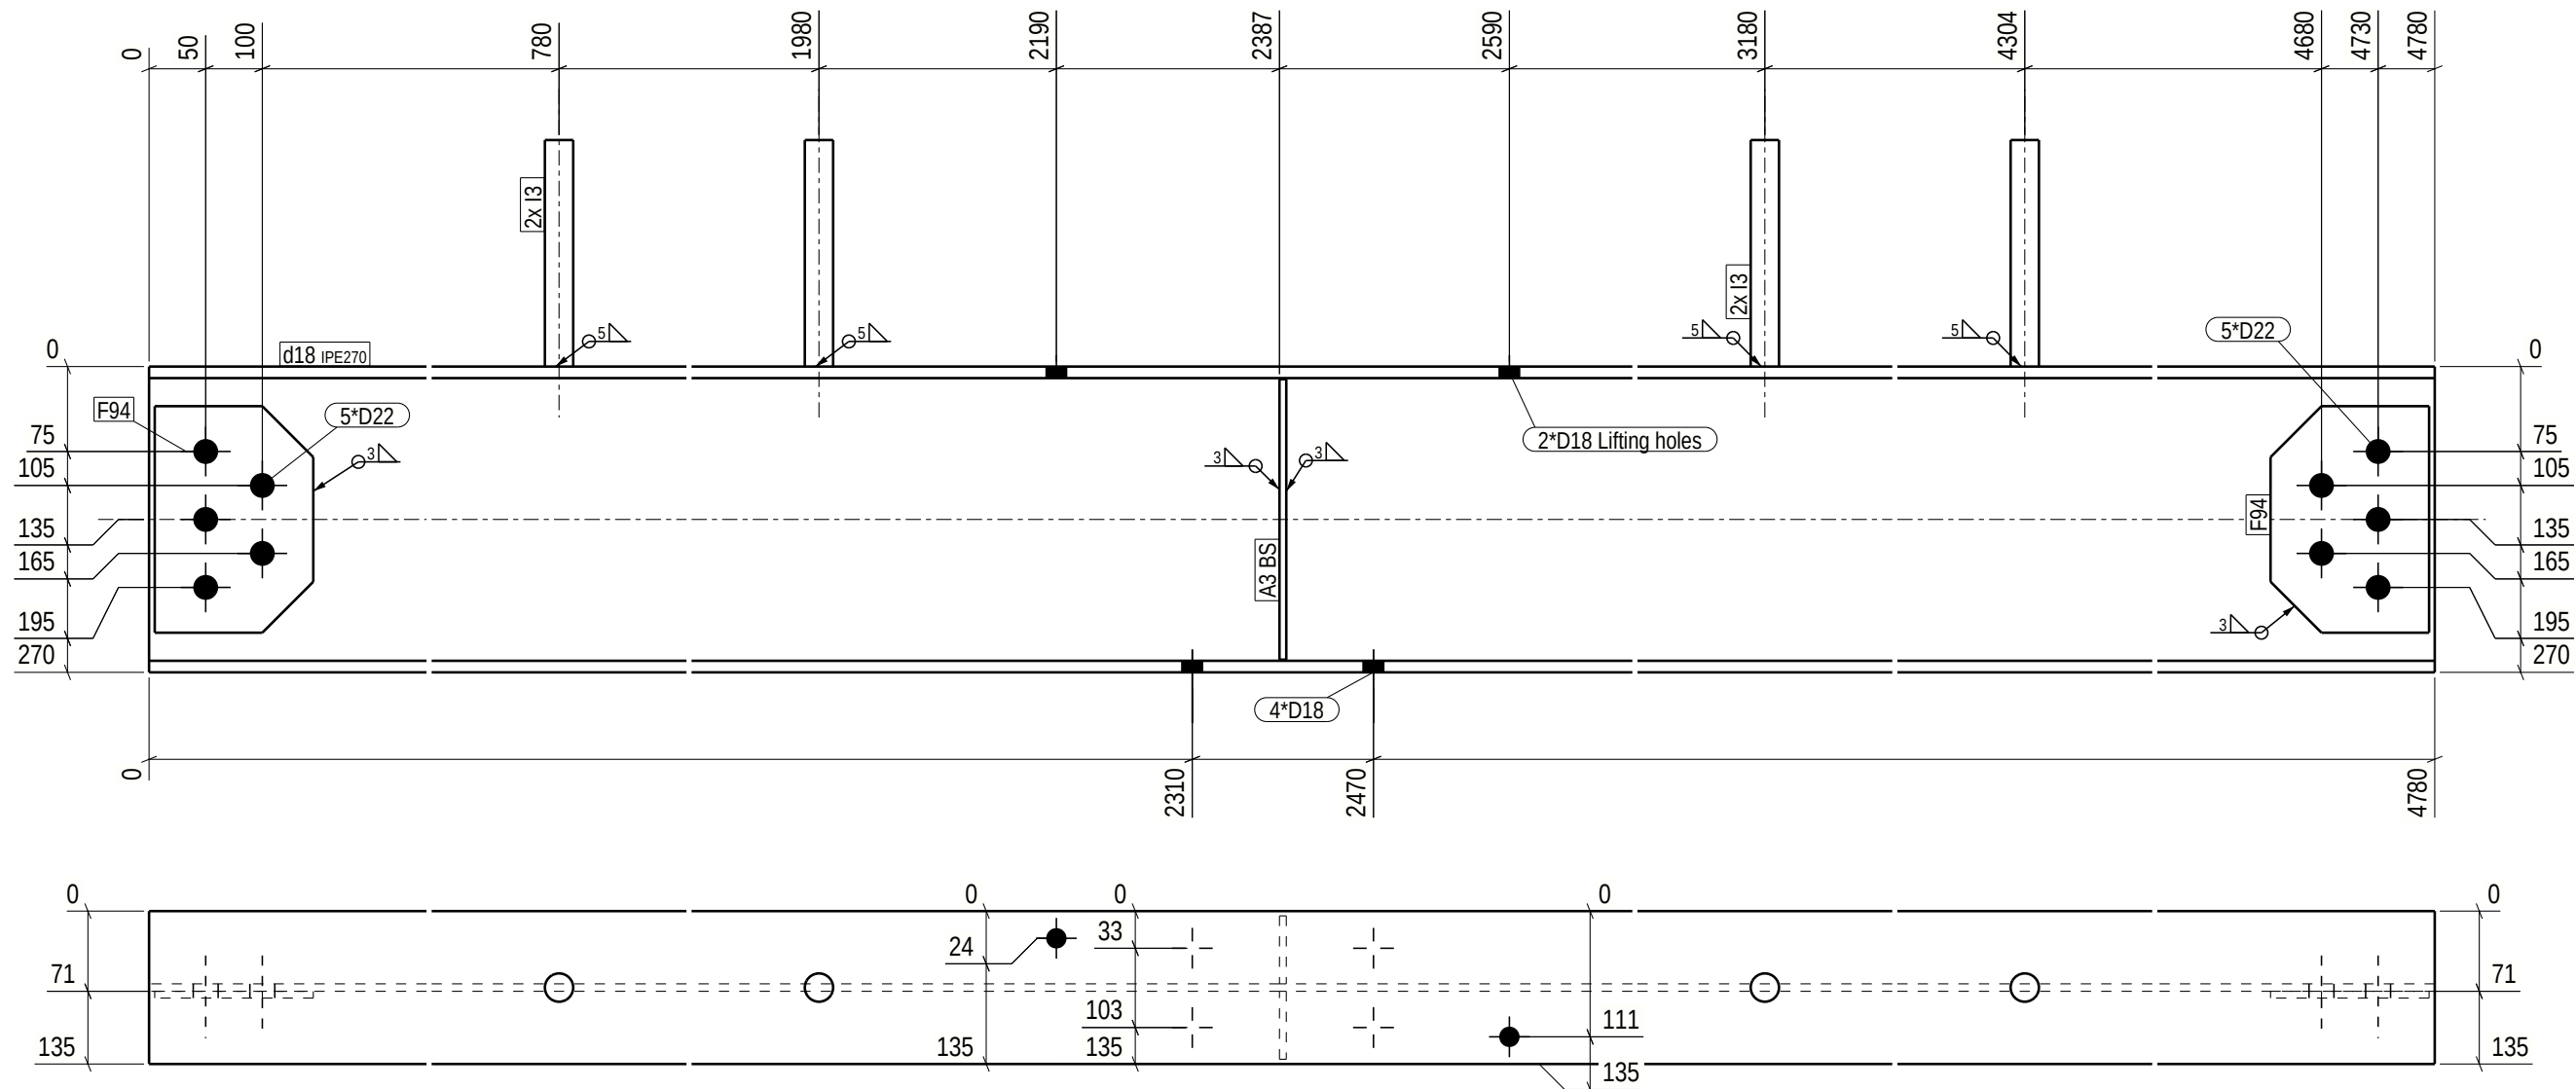

GENERAL NOTES: For your safety, check weight before handling:
0-5kg Light 5-15kg Normal 15+kg Heavy

ALL WELDS ARE 4 UNLESS NOTED ON DRAWING

MATERIAL LIST FOR ASSEMBLY MK'D **d.18** **1** No. Required

Mark	Profile	Material	No.	Length	Area	Weight
d18	IPE270	S355J2	1	4780	5.0	172.2 !!
A3	FL6*60	S355J2	2	248	0.0	0.7
F94	FL6*140	S355J2	2	200	0.1	1.2
I3	REBAR25	B550B	4	200	0.0	0.7
Total					5.2	179.0

Finish Class
Standard

Surface treatment info: Thickness/start point-> length No.

weld a = 4

PHASE	QUANTITY
1	1

* o 3 0 4 8 0 - 1 *						DS Stalkonstruktion		* A d 1 8 *	
PROJECT		Akkasæter Lager- og vedlikeholdshall				EXEC. CLASS		EXC 2	
MEMBER		Drager		QUANTITY:		1		PROJECT No 30480-1	
REVISION		ISSUED: 03.11.2025		DRAFTER: ZLL		BIM control: SST		DRAWING No. d.18	