
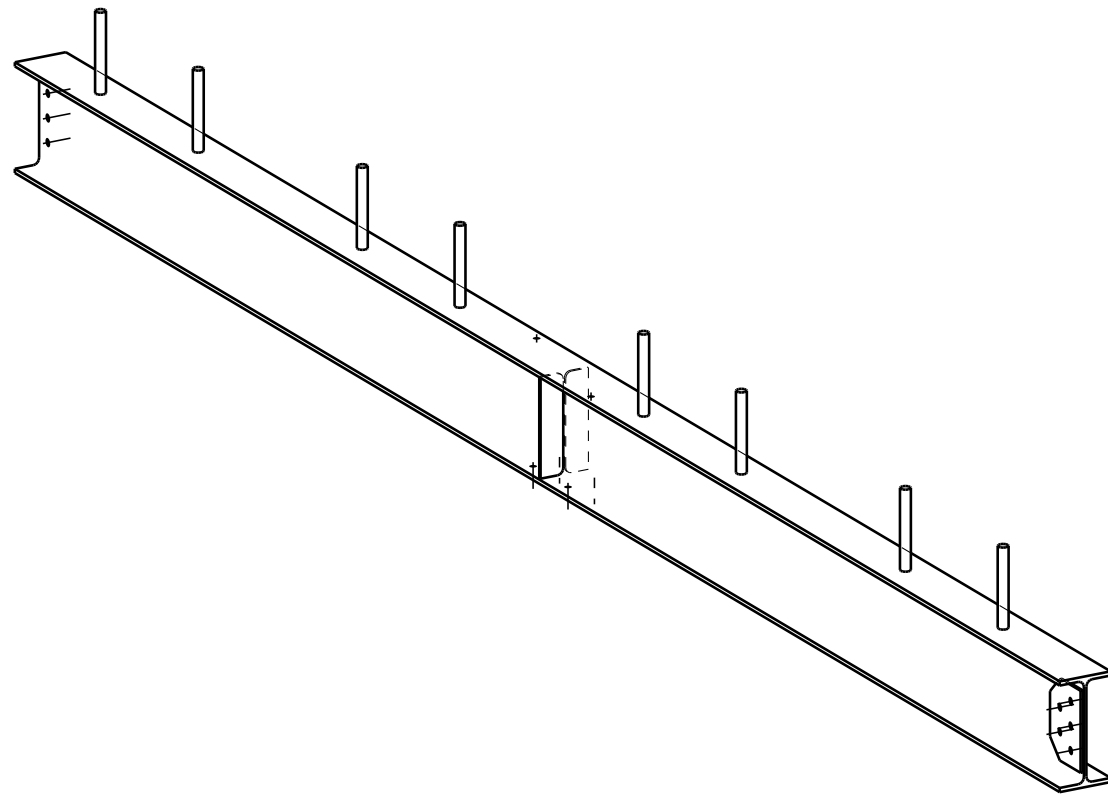


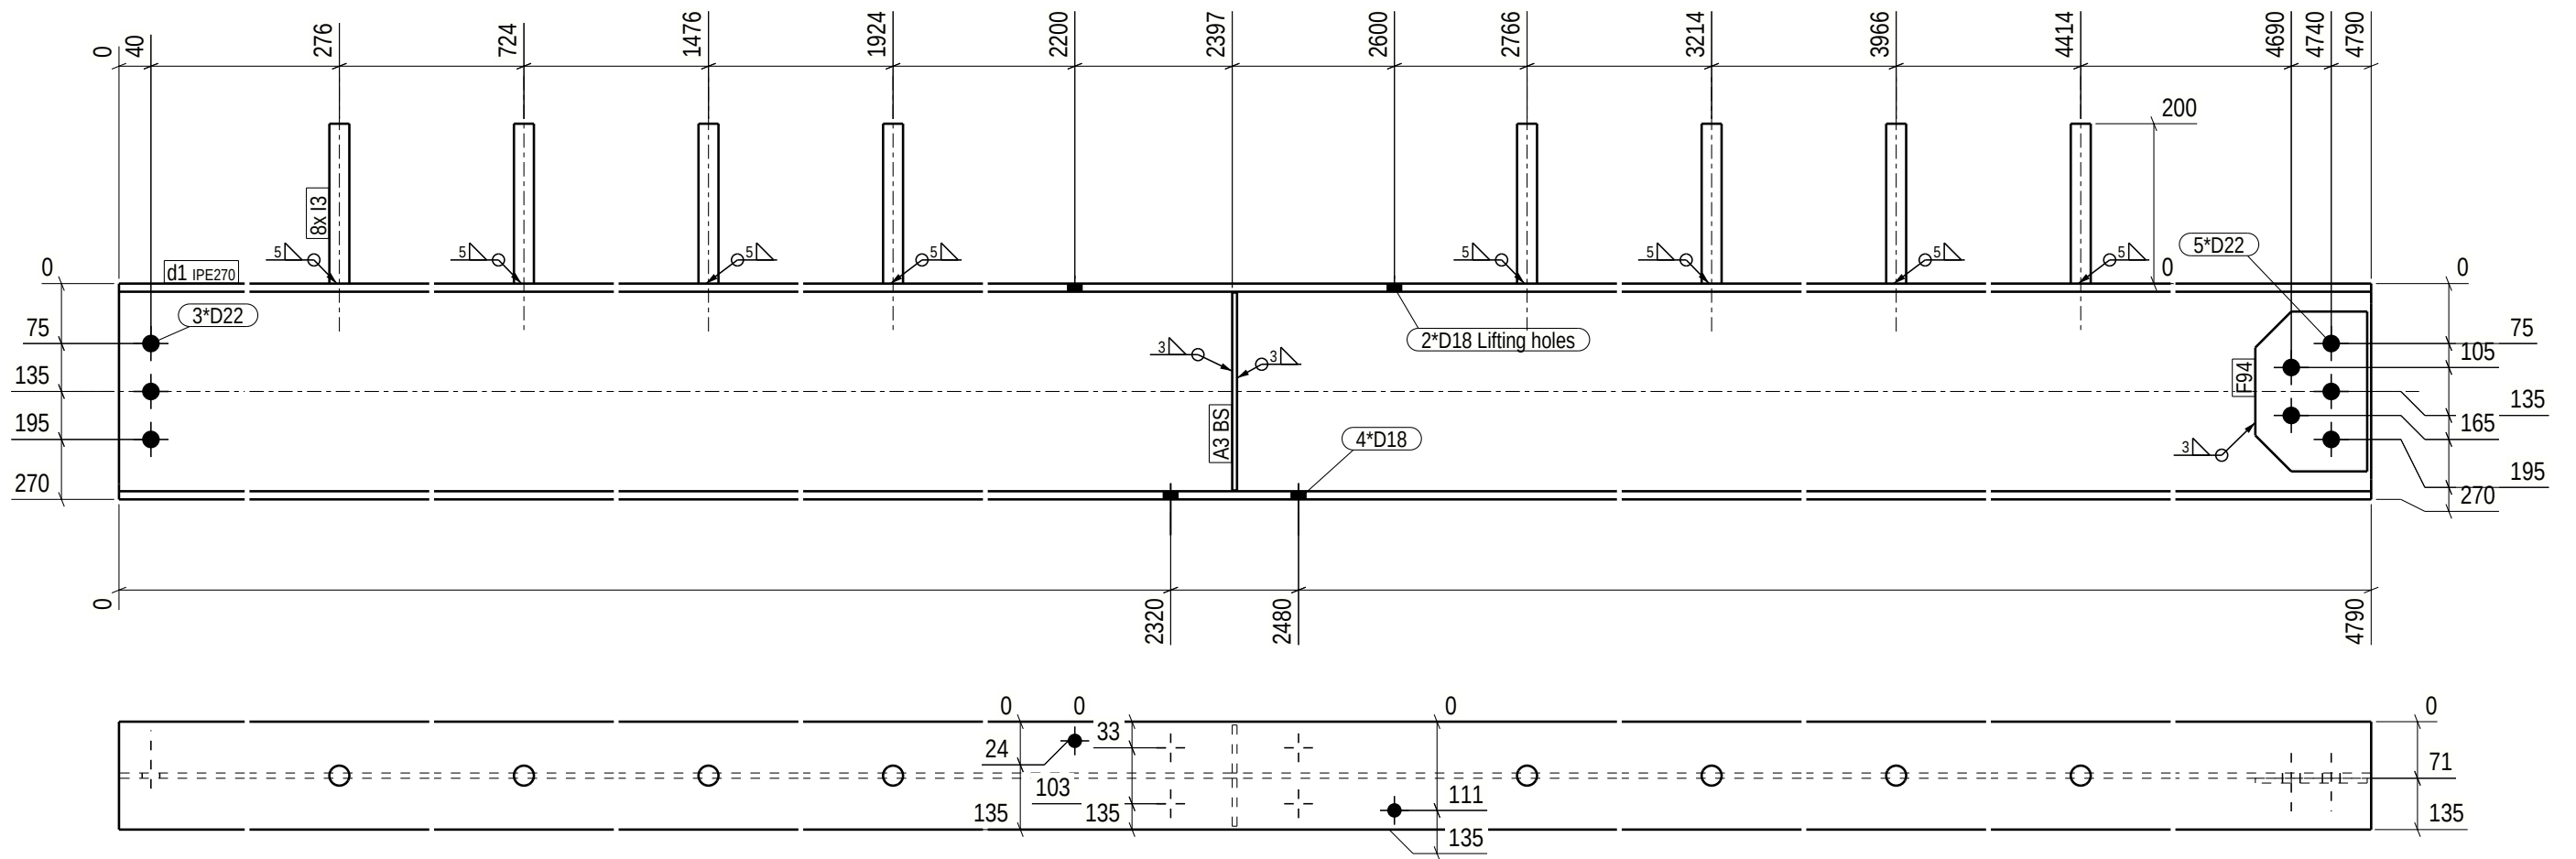

GENERAL NOTES: For your safety, check weight before handling:
0-5kg Light 5-15kg Normal 15+kg Heavy

ALL WELDS ARE 4 UNLESS NOTED ON DRAWING

MATERIAL LIST FOR ASSEMBLY MK'D **d.1** **1** No. Required

Mark	Profile	Material	No.	Length	Area	Weight
d1	IPE270	S355J2	1	4790	5.0	172.6 !!
A3	FL6*60	S355J2	2	248	0.0	0.7
F94	FL6*140	S355J2	1	200	0.1	1.2
I3	REBAR25	B550B	8	200	0.0	0.7
Total					5.2	181.1

Finish Class
Standard

Surface treatment info:	Thickness/start point-> length	No.
-------------------------	--------------------------------	-----

weld a = 4

PHASE	QUANTITY
1	1

* o 3 0 4 8 0 - 1 *  DS <i>Stalkonstruktion</i> * A d 1 *			
PROJECT	Akkasæter Lager- og vedlikeholdshall	EXEC. CLASS	EXC 2
MEMBER	Drager	QUANTITY:	1
REVISION		ISSUED:	03.11.2025
		DRAFTER:	ZLL
		BIM control:	SST
		PROJECT No	30480-1
		DRAWING No.	d.1