
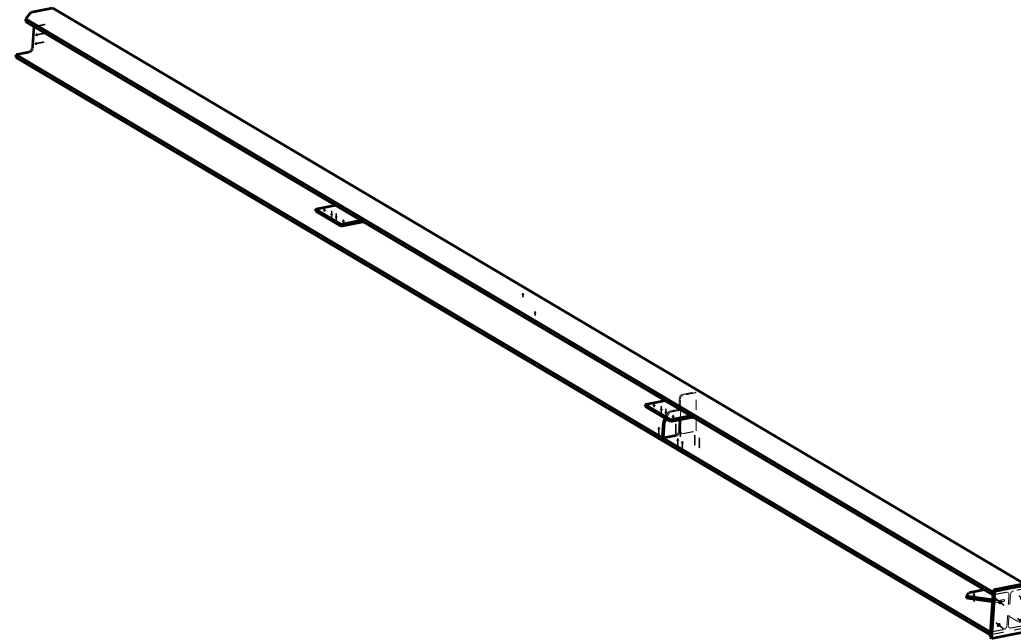
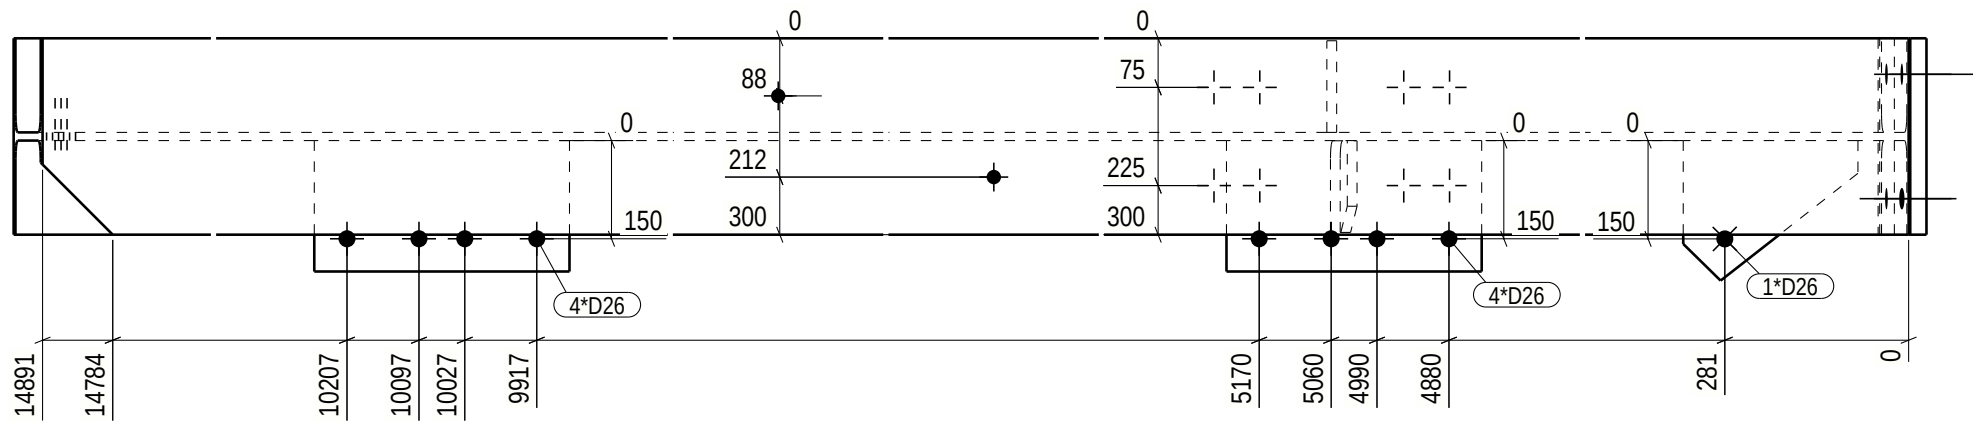
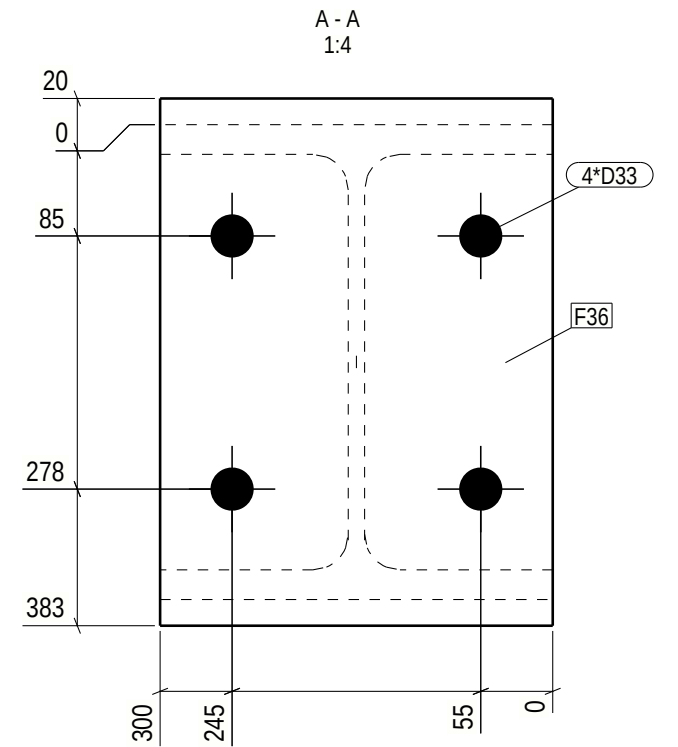


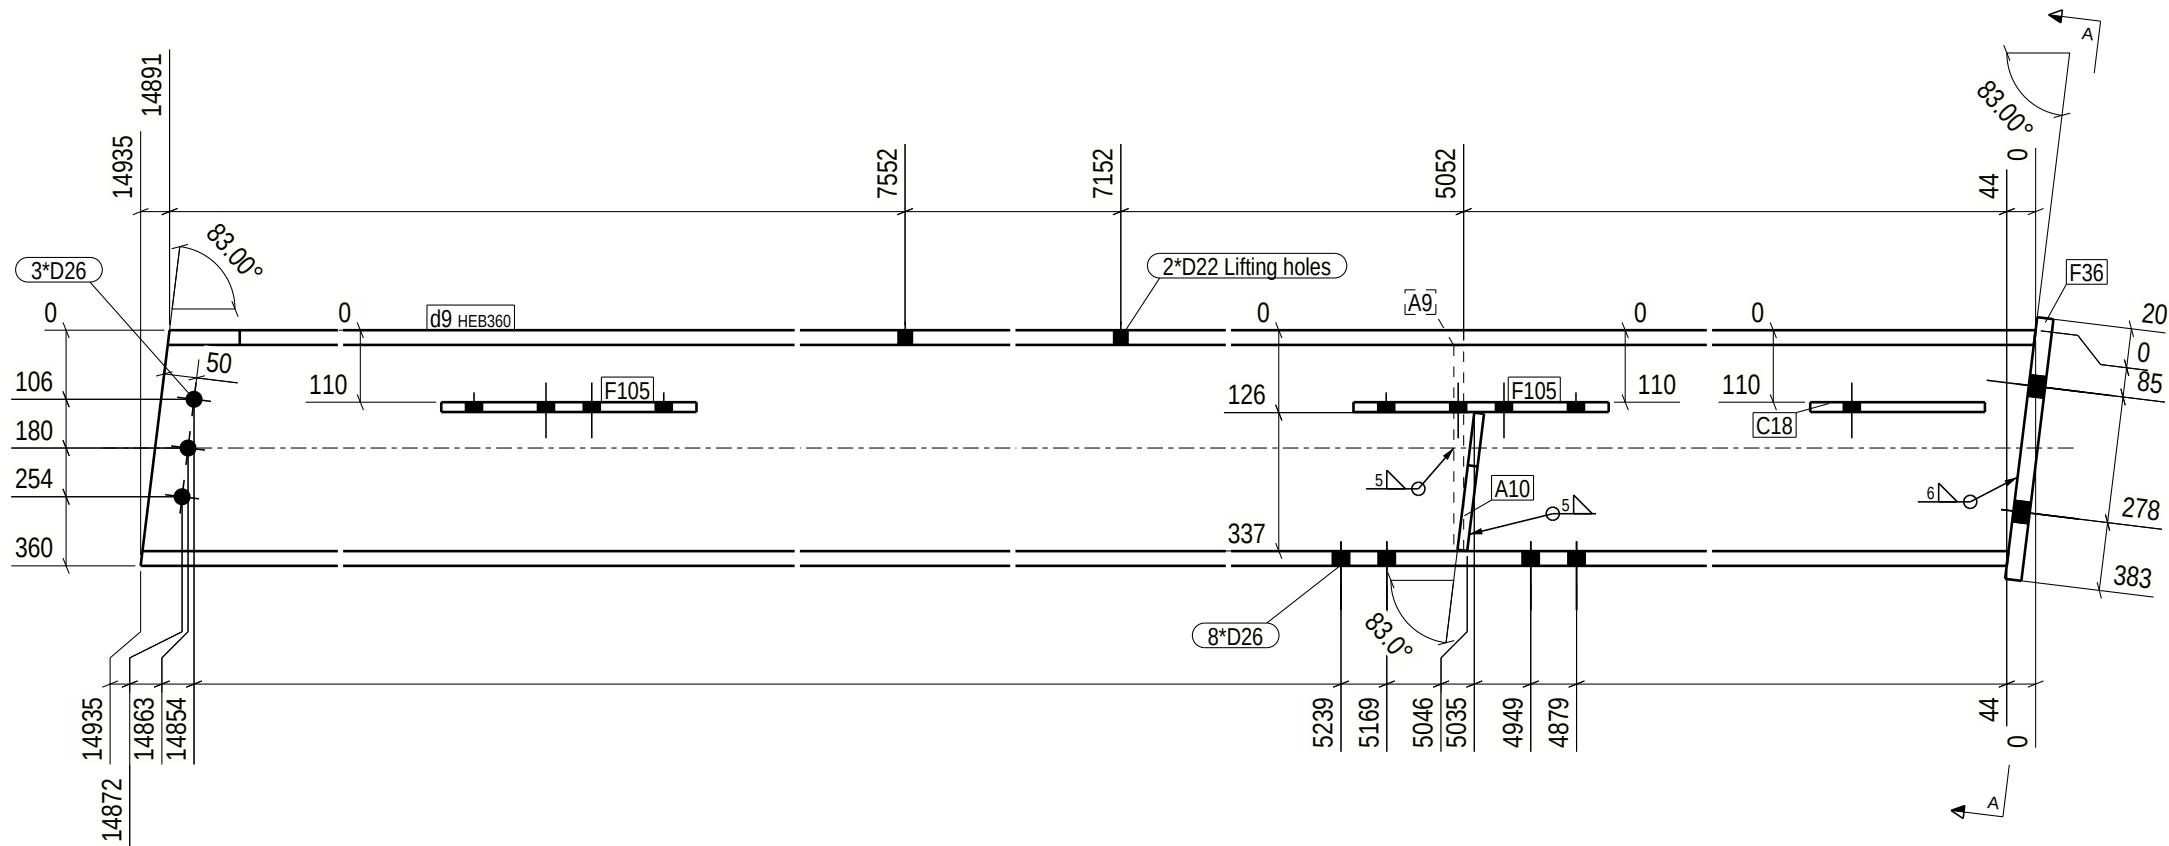

GENERAL NOTES: For your safety, check weight before handling:
0-5kg Light 5-15kg Normal 15+kg Heavy

ALL WELDS ARE 4 UNLESS NOTED ON DRAWING

MATERIAL LIST FOR ASSEMBLY MK'D **d.9** **1** No. Required

Mark	Profile	Material	No.	Length	Area	Weight
d9	HEB360	S355J2	1	14935	27.6	2117.3 !!
A9	FL15*140	S355J2	1	313	0.1	5.1
A10	FL15*140	S355J2	1	211	0.1	3.3
C18	PL15*214	S355J2	1	267	0.1	4.5
F36	FL25*300	S355J2	1	403	0.3	23.7 !!
F105	FL15*200	S355J2	2	390	0.2	9.2
Total				28.5	2172.3	

Finish Class
Standard

Surface treatment info: Thickness/start point-> length No.

weld a = 4

PHASE	QUANTITY
1	1

* o 3 0 4 8 0 - 1 *  DS <i>Stalkonstruktion</i> * A d 9 *			
PROJECT	Akkasæter Lager- og vedlikeholdshall	EXEC. CLASS	EXC 2
MEMBER	Drager	QUANTITY:	1
REVISION		ISSUED:	03.11.2025
		DRAFTER:	ZLL
		BIM control:	SST
PROJECT No		30480-1	
DRAWING No.		d.9	