
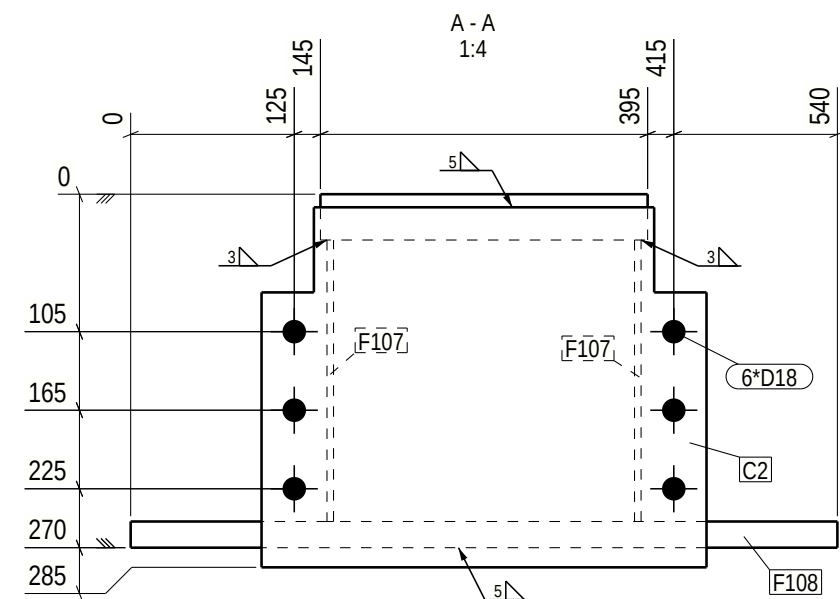
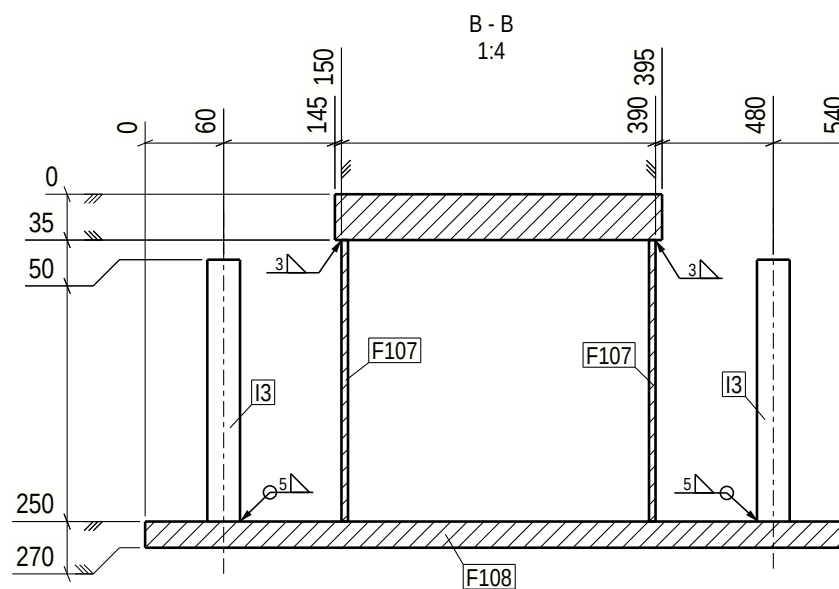
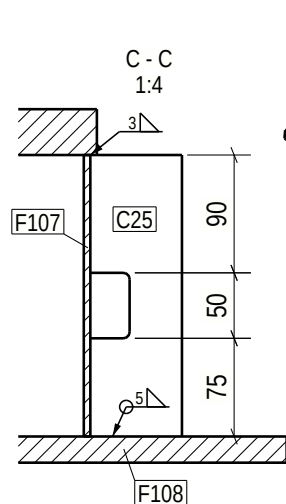
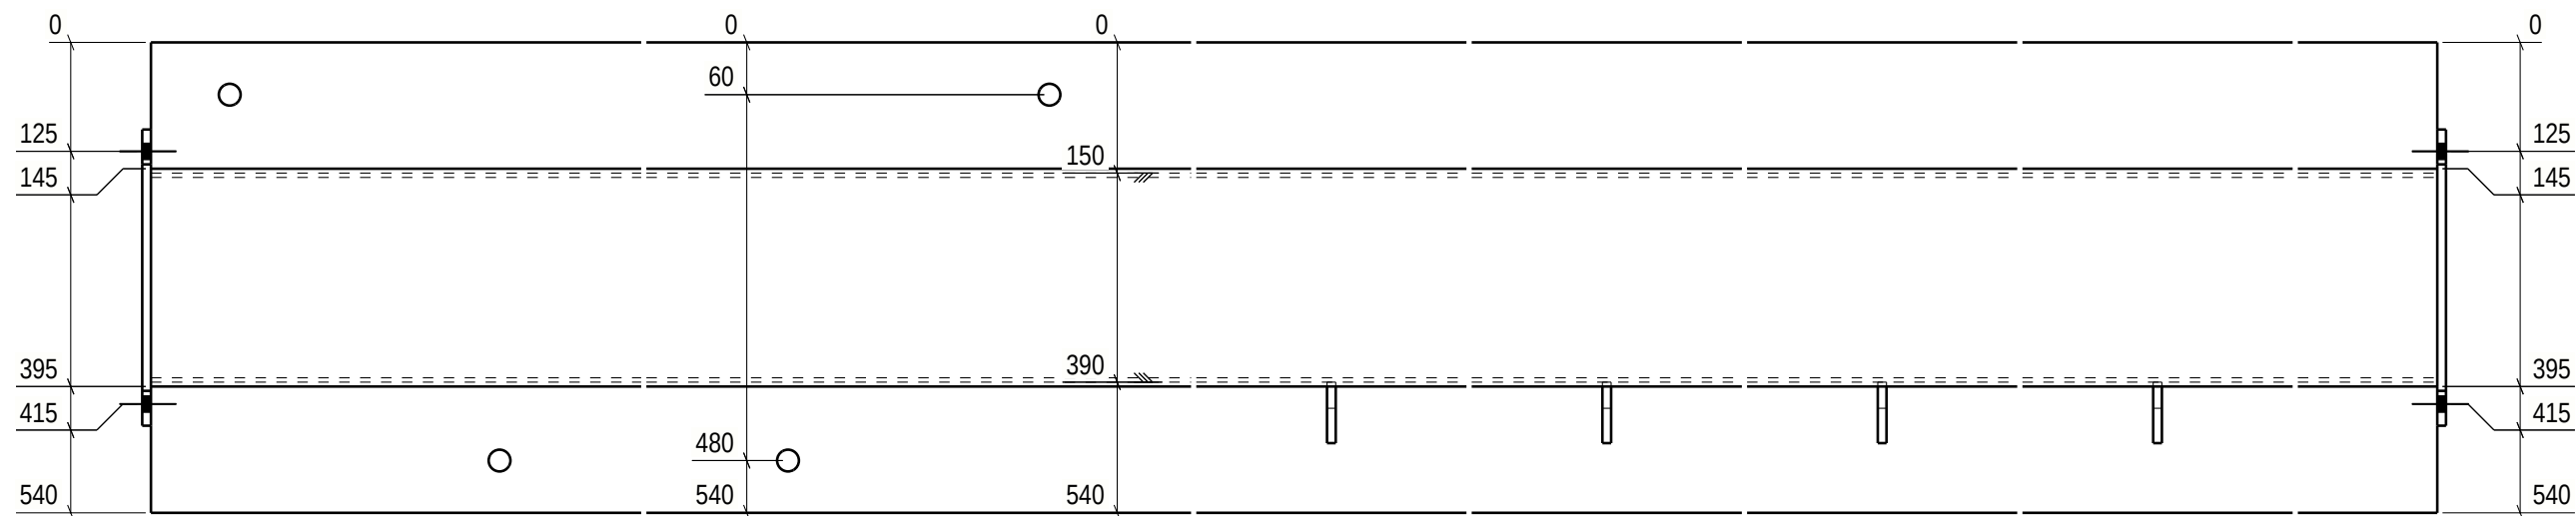


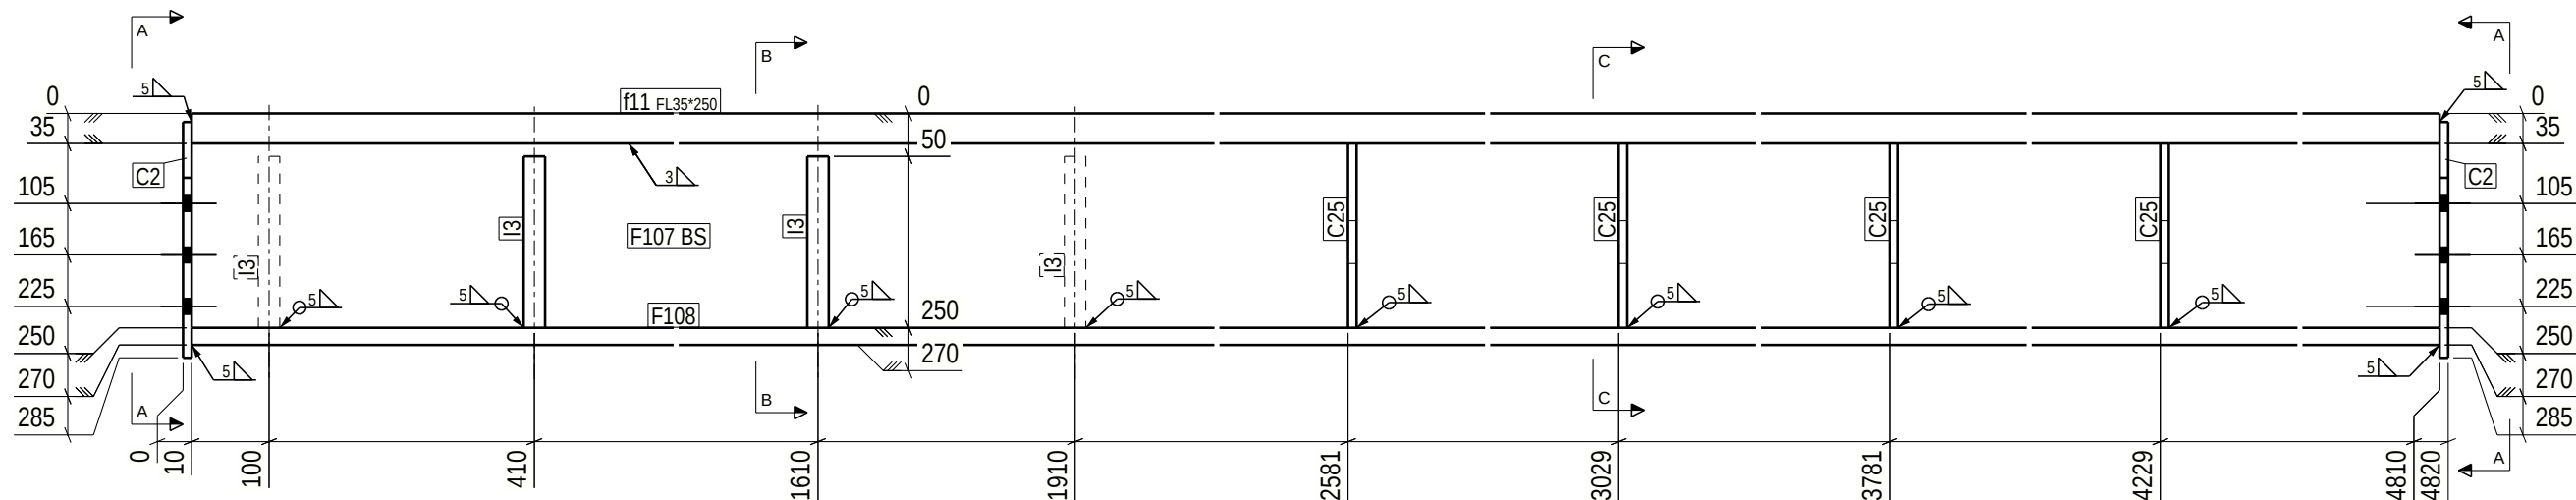

! NDT test:  
Part thickness >30mm  
f11

GENERAL NOTES: For your safety, check weight before handling:  
0-5kg Light 5-15kg Normal 15+kg Heavy

ALL WELDS ARE 4 UNLESS NOTED ON DRAWING

MATERIAL LIST FOR ASSEMBLY MK'D f.11 1 No. Required

| Mark  | Profile  | Material | No. | Length | Area | Weight   |
|-------|----------|----------|-----|--------|------|----------|
| f11   | FL35*250 | S355J2   | 1   | 4800   | 2.8  | 329.7 !! |
| C2    | PL10*275 | S355J2   | 2   | 340    | 0.2  | 6.9      |
| C25   | PL10*70  | S355J2   | 4   | 215    | 0.0  | 1.1      |
| F107  | FL5*215  | S355J2   | 2   | 4800   | 2.1  | 40.5 !!  |
| F108  | FL20*540 | S355J2   | 1   | 4800   | 5.4  | 406.9 !! |
| I3    | REBAR25  | B550B    | 4   | 200    | 0.0  | 0.7      |
| Total |          |          |     | 13.0   |      | 838.7    |

Finish Class  
Standard

Surface treatment info: Thickness/start point-> length No.

OPSVEJST EMNE

weld a = 4

| PHASE | QUANTITY |
|-------|----------|
| 1     | 1        |

|                     |                                      |   |                      |             |                    |
|---------------------|--------------------------------------|---|----------------------|-------------|--------------------|
| * o 3 0 4 8 0 - 1 * |                                      |  <b>DS</b> Skalkonstruktion |                      | * A f 1 1 * |                    |
| PROJECT             | Akkasæter Lager- og vedlikeholdshall |   |                      | EXEC. CLASS | EXC 2              |
| MEMBER              | HSQ                                  |   | QUANTITY:            | 1           | PROJECT No 30480-1 |
| REVISION            |                                      | ISSUED: 03.11.2025                                                                                               | DRAFTER: BIM control | ZLL SST     | DRAWING No. f.11   |