
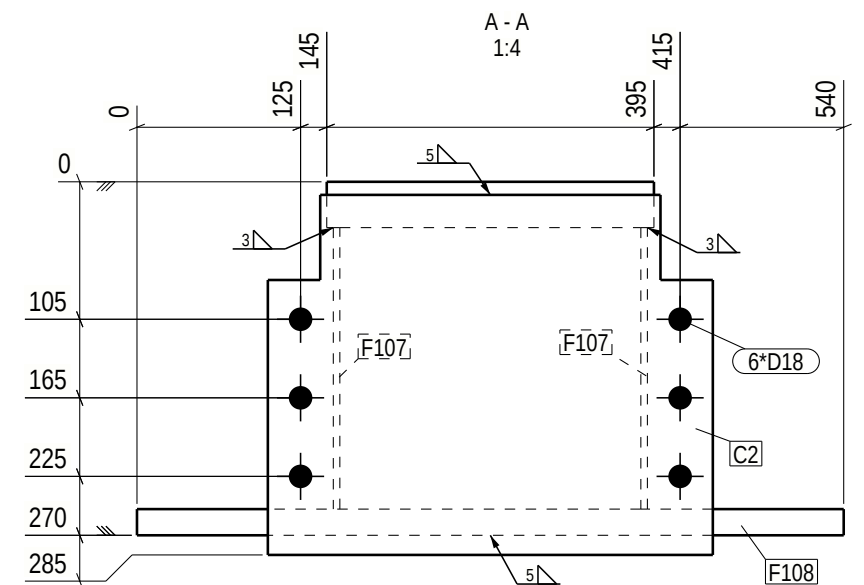
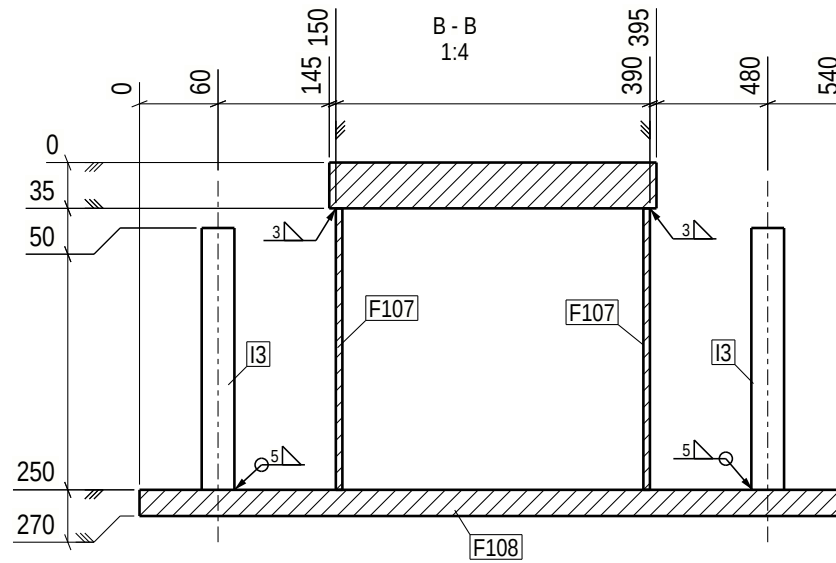
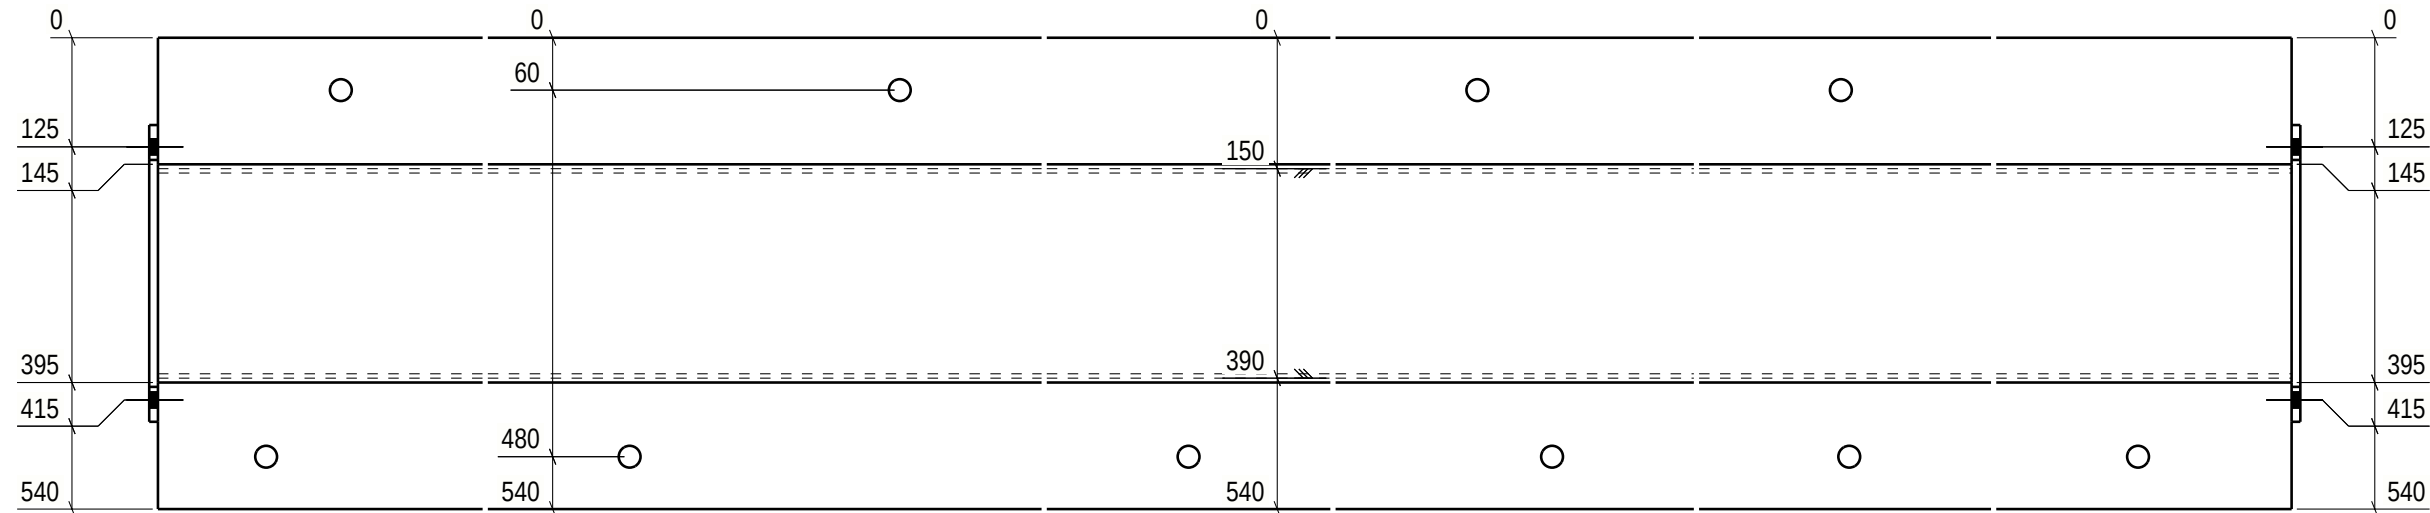


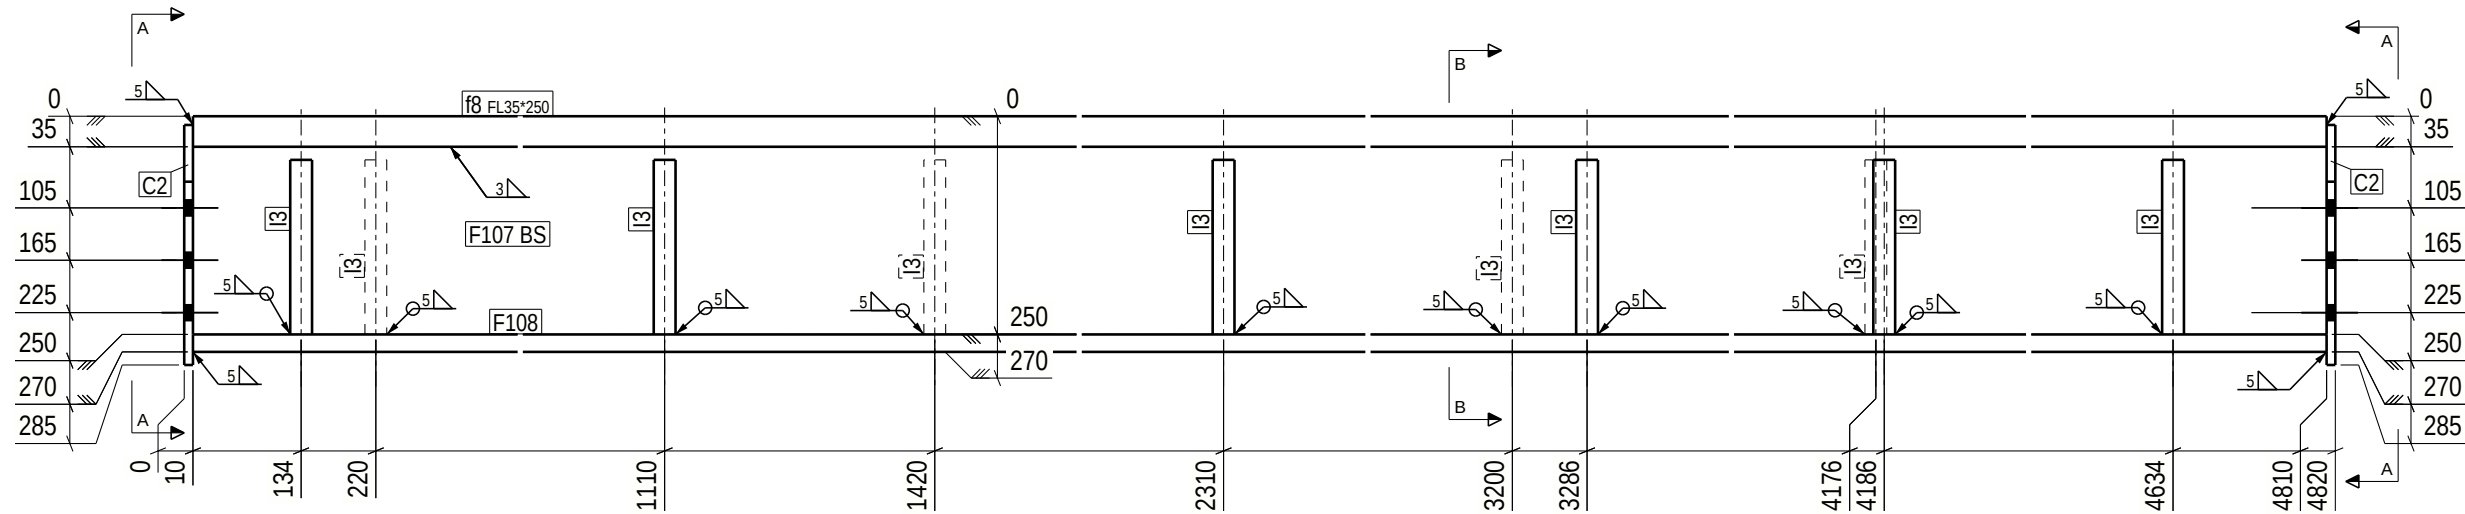

OPSVEJST EMNE

! NDT test:
Part thickness >30mm
f8

GENERAL NOTES: For your safety, check weight before handling:
0-5kg Light 5-15kg Normal 15+kg Heavy

ALL WELDS ARE 4 UNLESS NOTED ON DRAWING

MATERIAL LIST FOR ASSEMBLY MK'D f.8

Mark	Profile	Material	No.	Length	Area	Weight
f8	FL35*250	S355J2	1	4800	2.8	329.7 !!
C2	PL10*275	S355J2	2	340	0.2	6.9
F107	FL5*215	S355J2	2	4800	2.1	40.5 !!
F108	FL20*540	S355J2	1	4800	5.4	406.9 !!
I3	REBAR25	B550B	10	200	0.0	0.7
Total				12.9	838.9	

Finish Class
Standard

Surface treatment info:

Thickness/start point--> length

No.

weld a = 4

PHASE	QUANTITY
1	1

* o 3 0 4 8 0 - 1 * DS Skalkonstruktion * A f 8 *			
PROJECT	Akkasæter Lager- og vedlikeholdshall	EXEC. CLASS	EXC 2
MEMBER	HSQ	QUANTITY:	1 PROJECT No 30480-1
REVISION	ISSUED: 03.11.2025	DRAFTER: ZLL	DRAWING No. f.8
	BIM control: SST		