
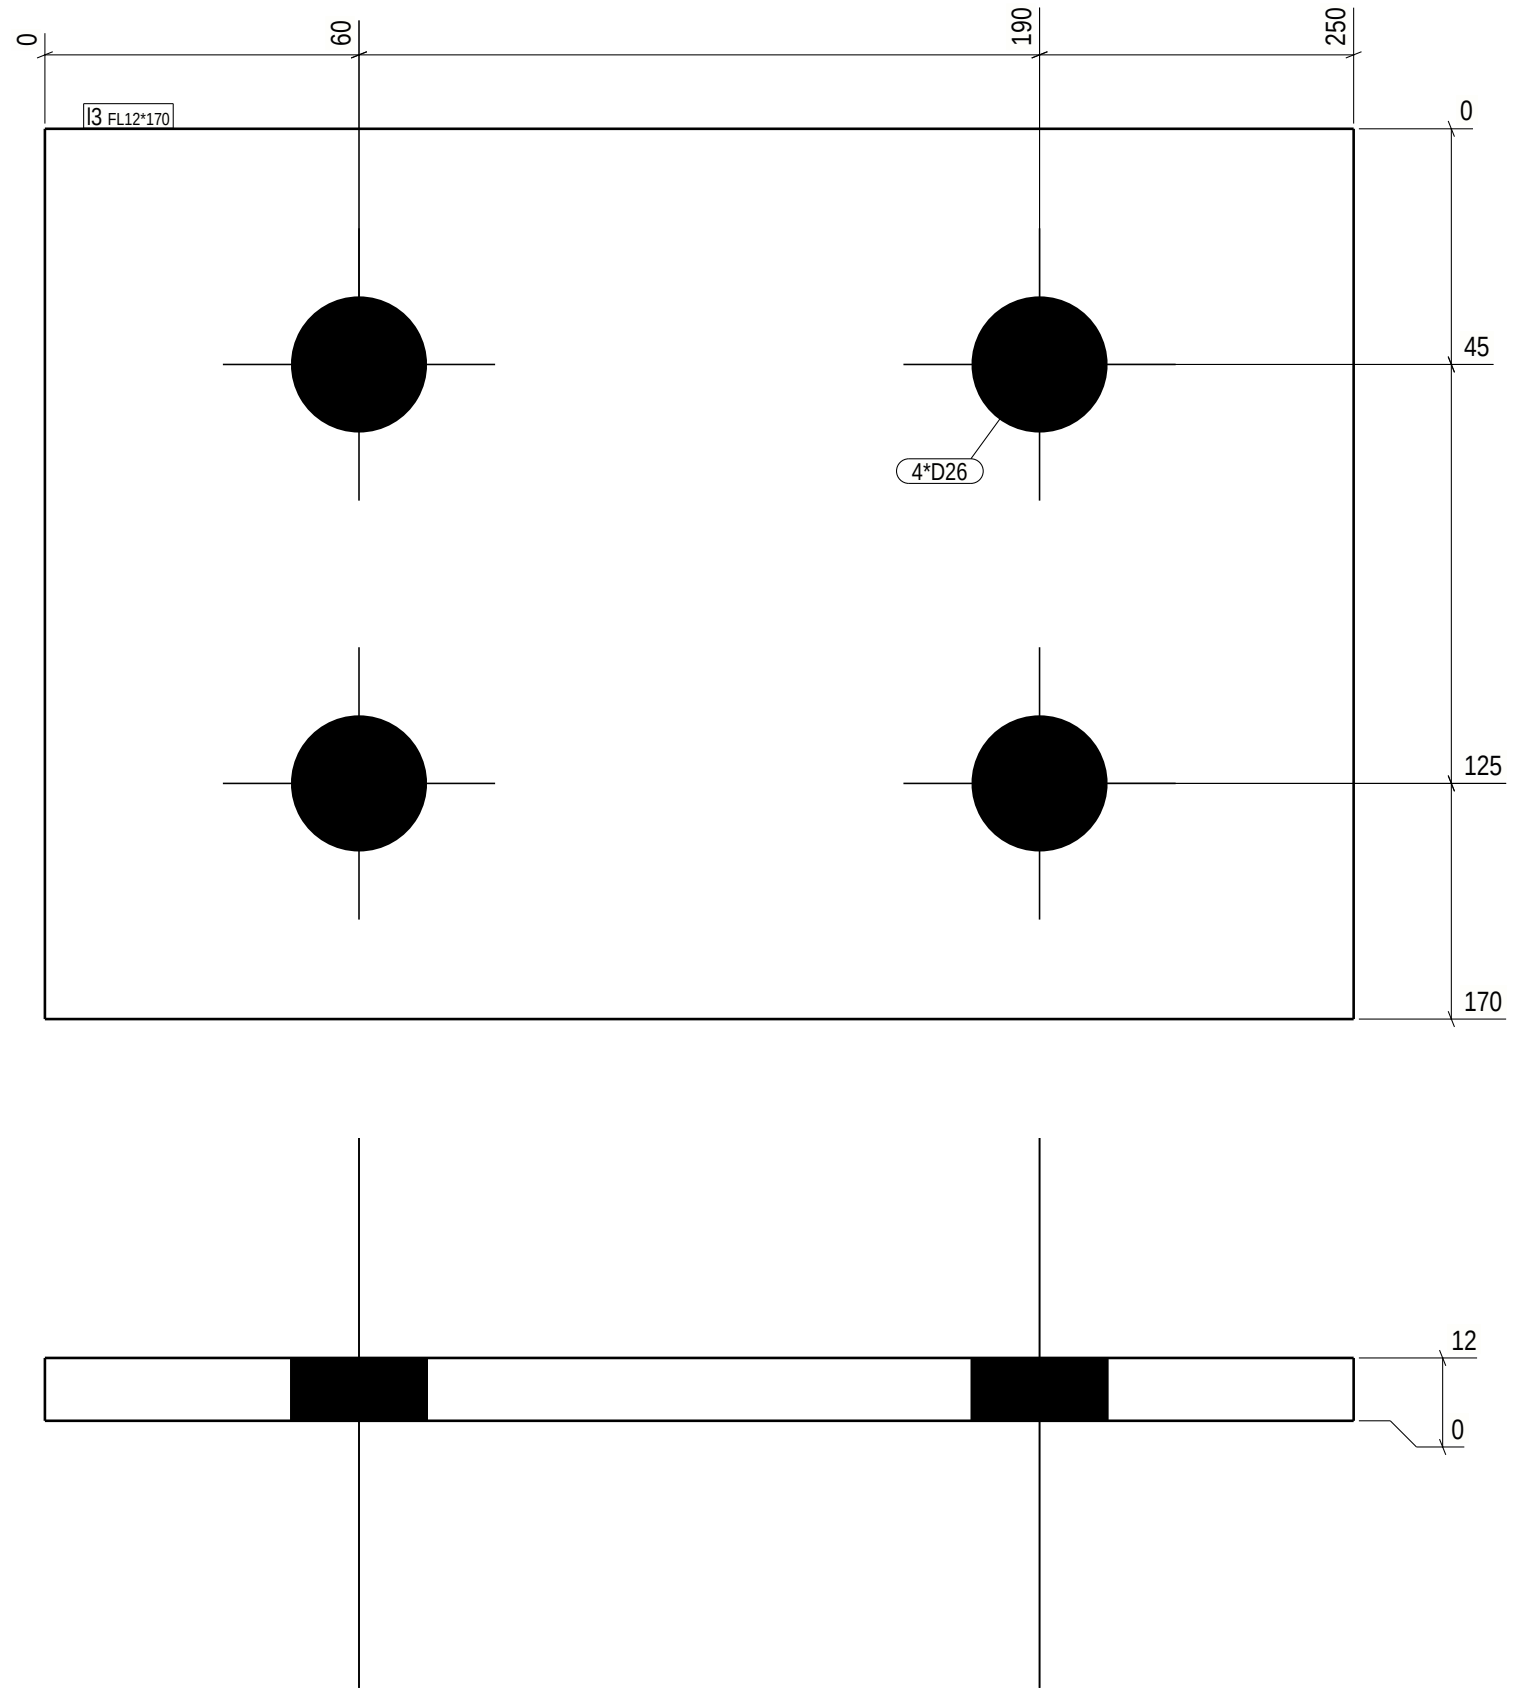


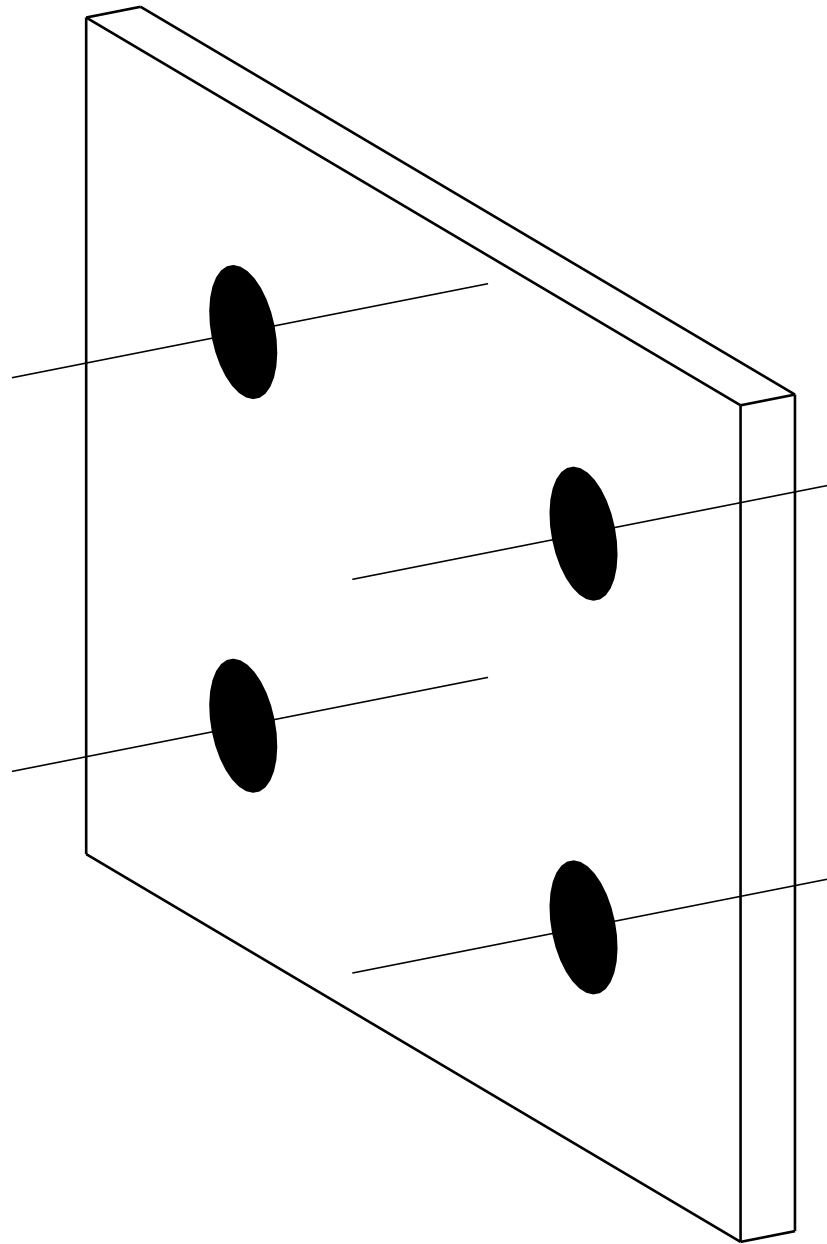

GENERAL NOTES: For your safety, check weight before handling:
0-5kg Light 5-15kg Normal 15+kg Heavy

ALL WELDS ARE 4 UNLESS NOTED ON DRAWING

MATERIAL LIST FOR ASSEMBLY MK'D I.3						
			32 No. Required			
Mark	Profile	Material	No.	Length	Area	Weight
I3	FL12*170	S355J2	1	250	0.1	4.0
Total					0.1	4.0

Finish Class
Standard

Surface treatment info: Thickness/start point--> length No.

weld a = 4

PHASE	QUANTITY
1	32

* o 3 0 4 8 0 - 1 * DS Stalkonstruktion * A I 3 *					
PROJECT	Akkasæter Lager- og vedlikeholdshall			EXEC. CLASS	EXC 2
MEMBER	Løsdele		QUANTITY:	32	PROJECT No 30480-1
REVISION		ISSUED: 03.11.2025	DRAFTER: ZLL	BIM control: SST	DRAWING No. I.3

Loose part
no welding