


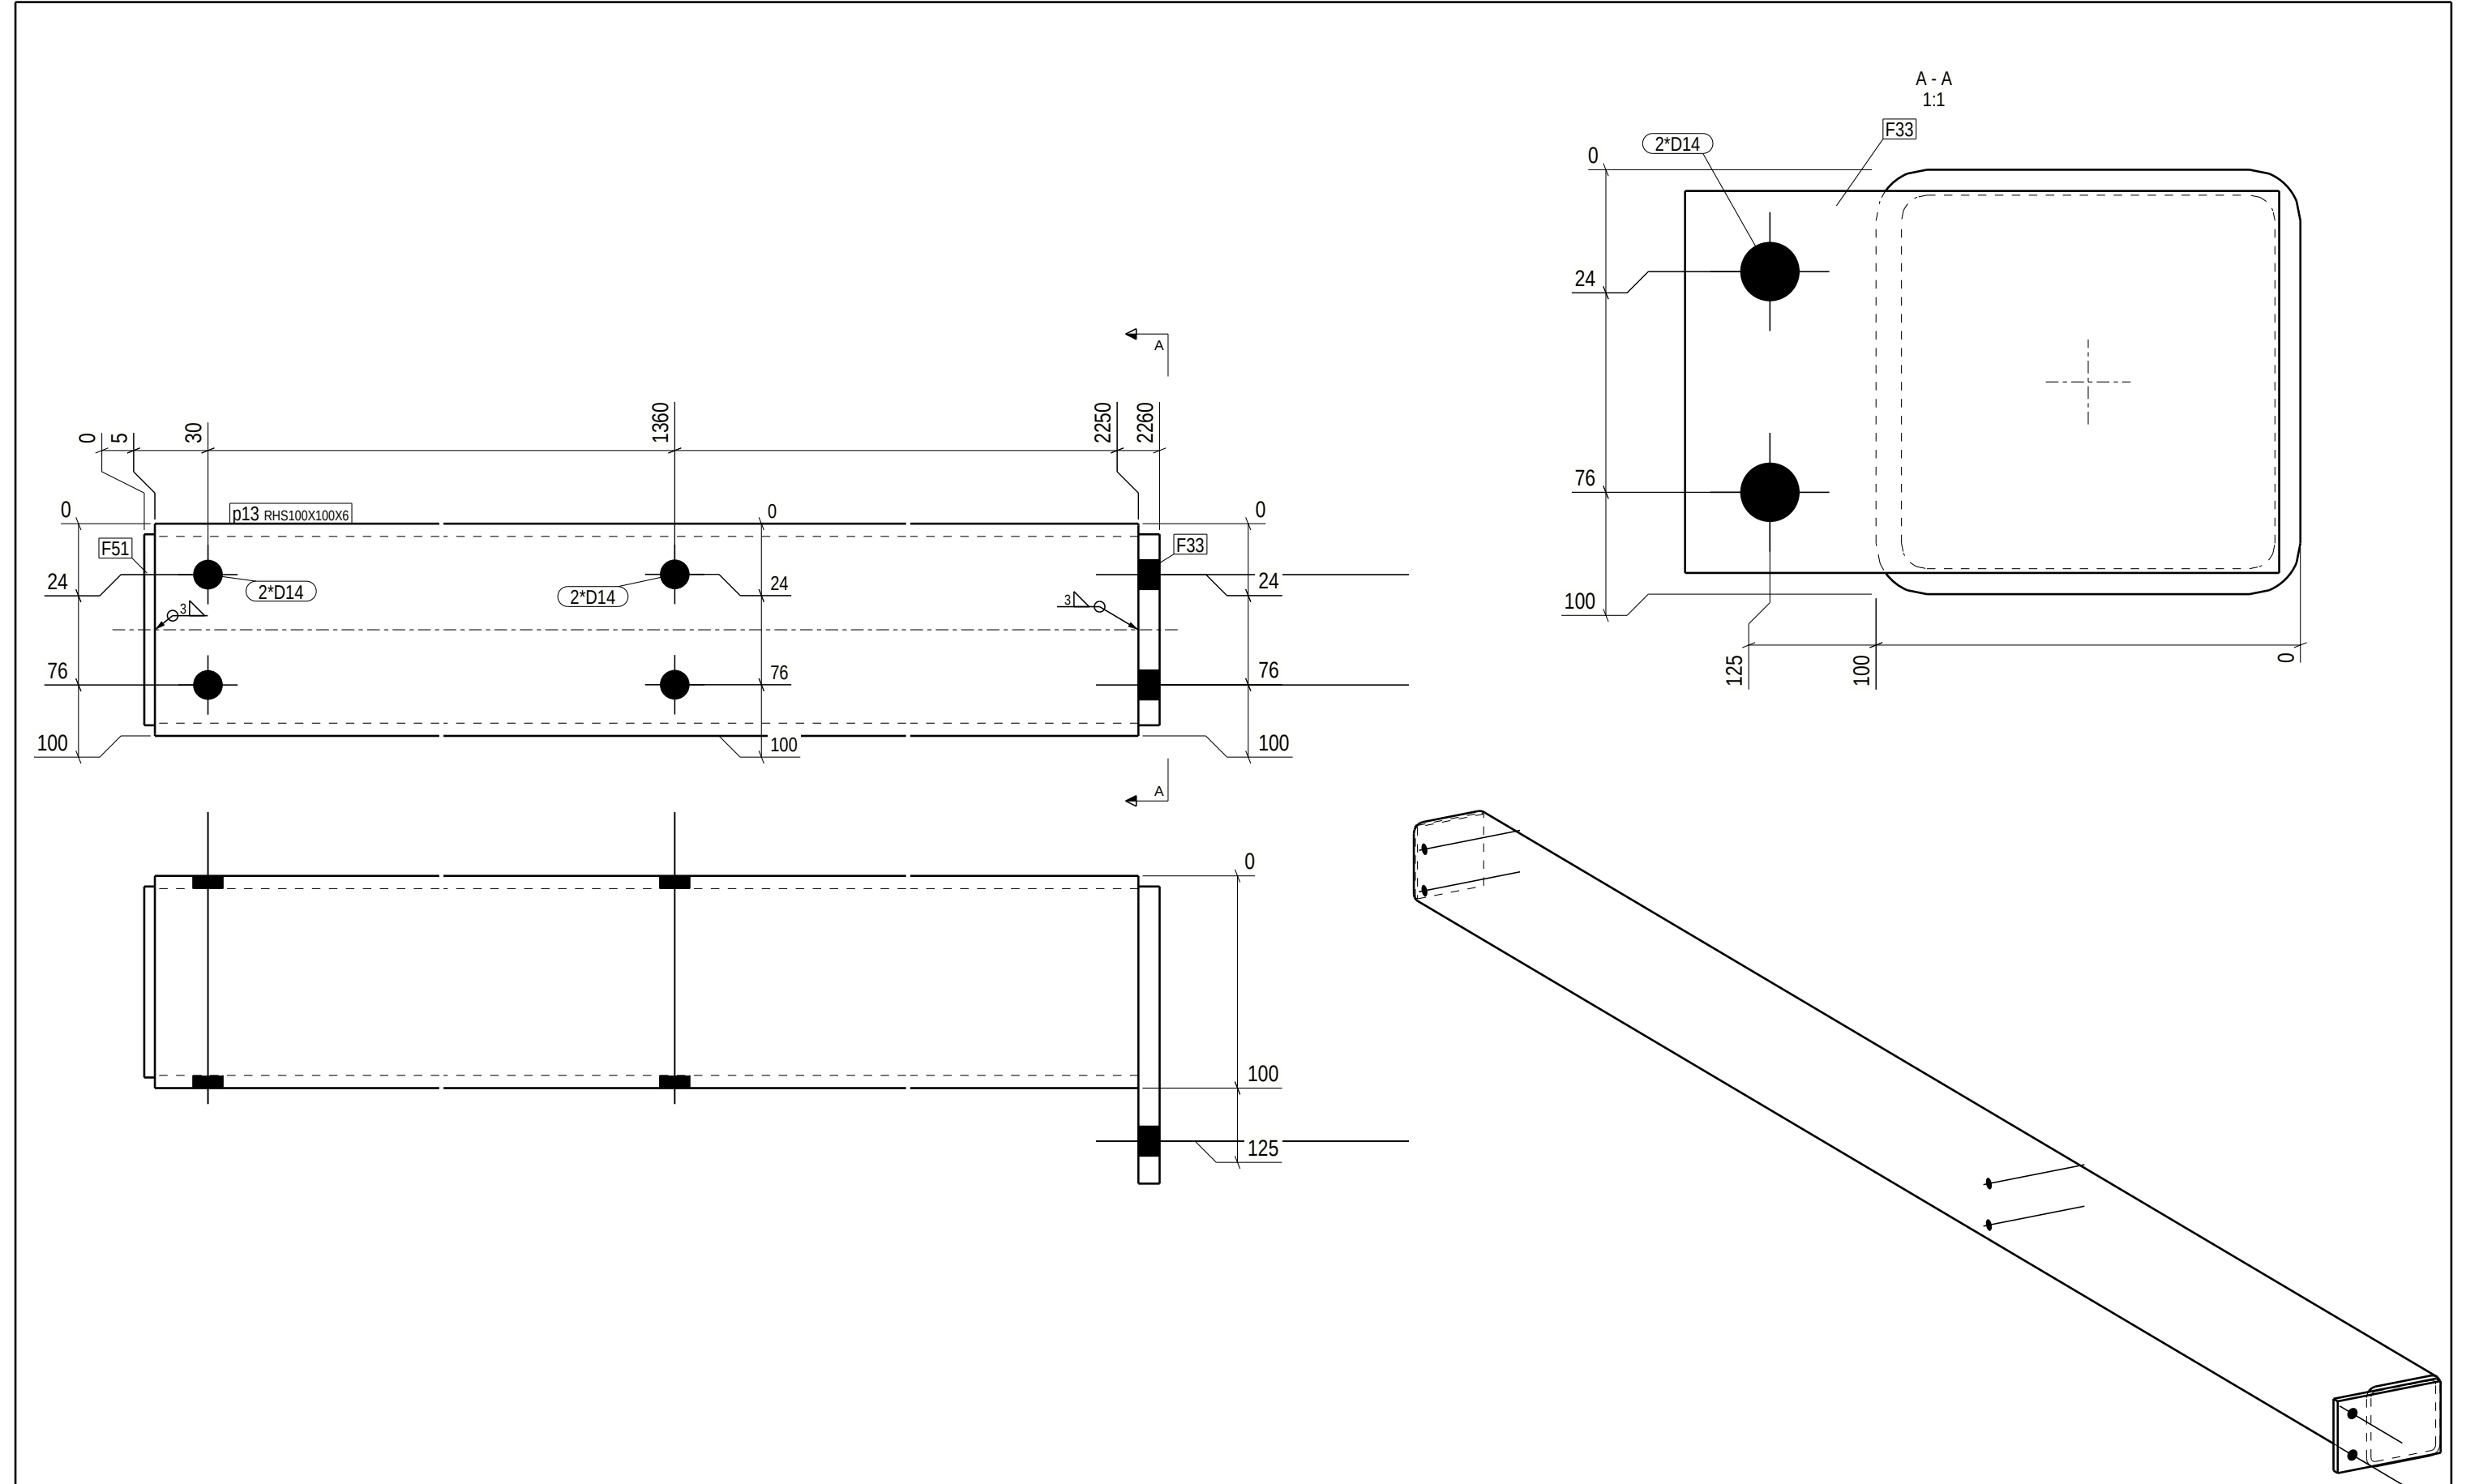

GENERAL NOTES:						
For your safety, check weight before handling:						
0-5kg Light 5-15kg Normal 15+kg Heavy						
ALL WELDS ARE 4 UNLESS NOTED ON DRAWING						
MATERIAL LIST FOR ASSEMBLY MK'D p.13						
1 No. Required						
Mark	Profile	Material	No.	Length	Area	Weight
p13	RHS100X100X6	S355J2H	1	2245	0.9	38.0 !!
F33	FL10*90	S355J2	1	140	0.0	1.0
F51	FL5*90	S355J2	1	90	0.0	0.3
Total					0.9	39.3

Finish Class
Standard

Surface treatment info:	Thickness/start point-> length	No.
-------------------------	--------------------------------	-----

weld a = 4

PHASE	QUANTITY
1	1

* o 3 0 4 8 0 - 1 * DS Steelkonstruktion * A p 1 3 *			
PROJECT	Akkasæter Lager- og vedlikeholdshall	EXEC. CLASS	EXC 2
MEMBER	Portomfatning	QUANTITY:	1
REVISION	ISSUED: 03.11.2025	DRAFTER: ZLL	PROJECT No 30480-1
	BIM control: SST		DRAWING No. p.13