
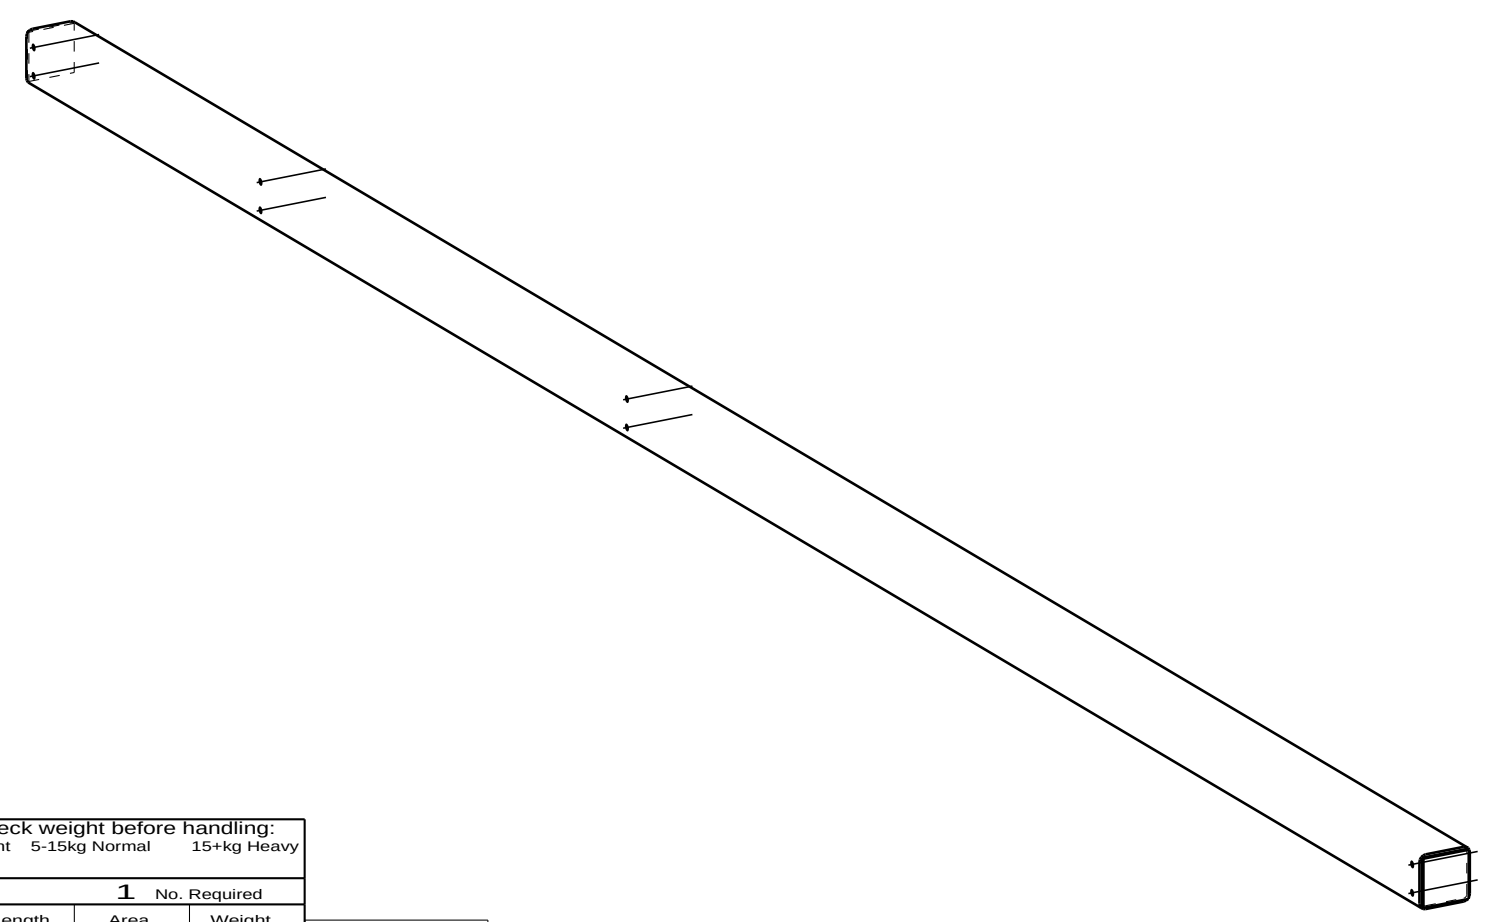
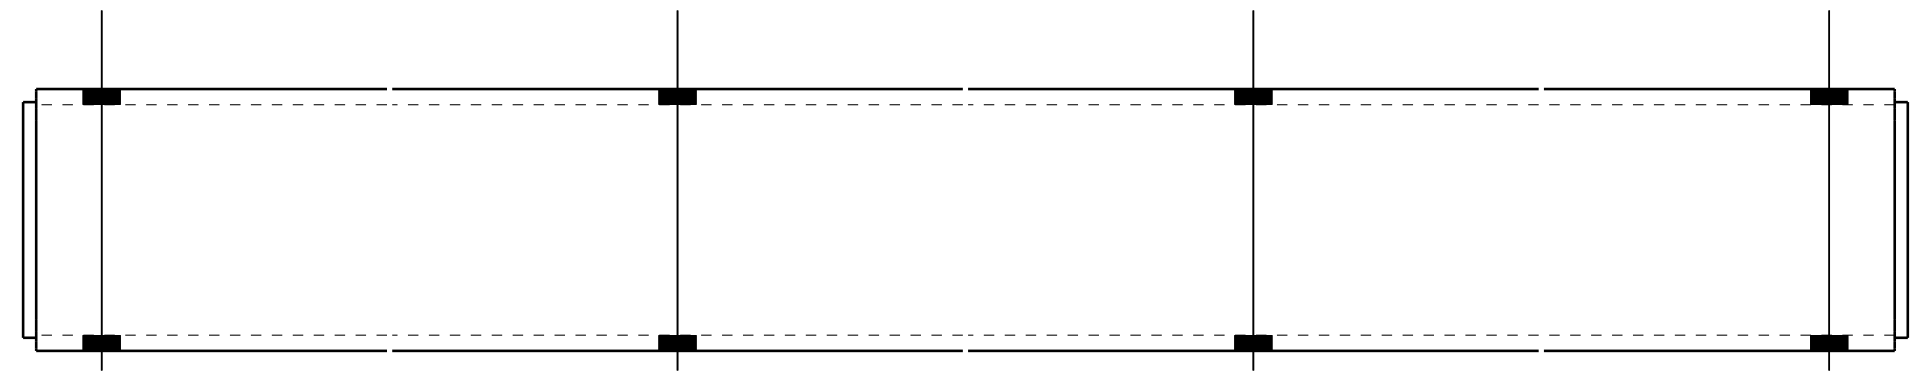


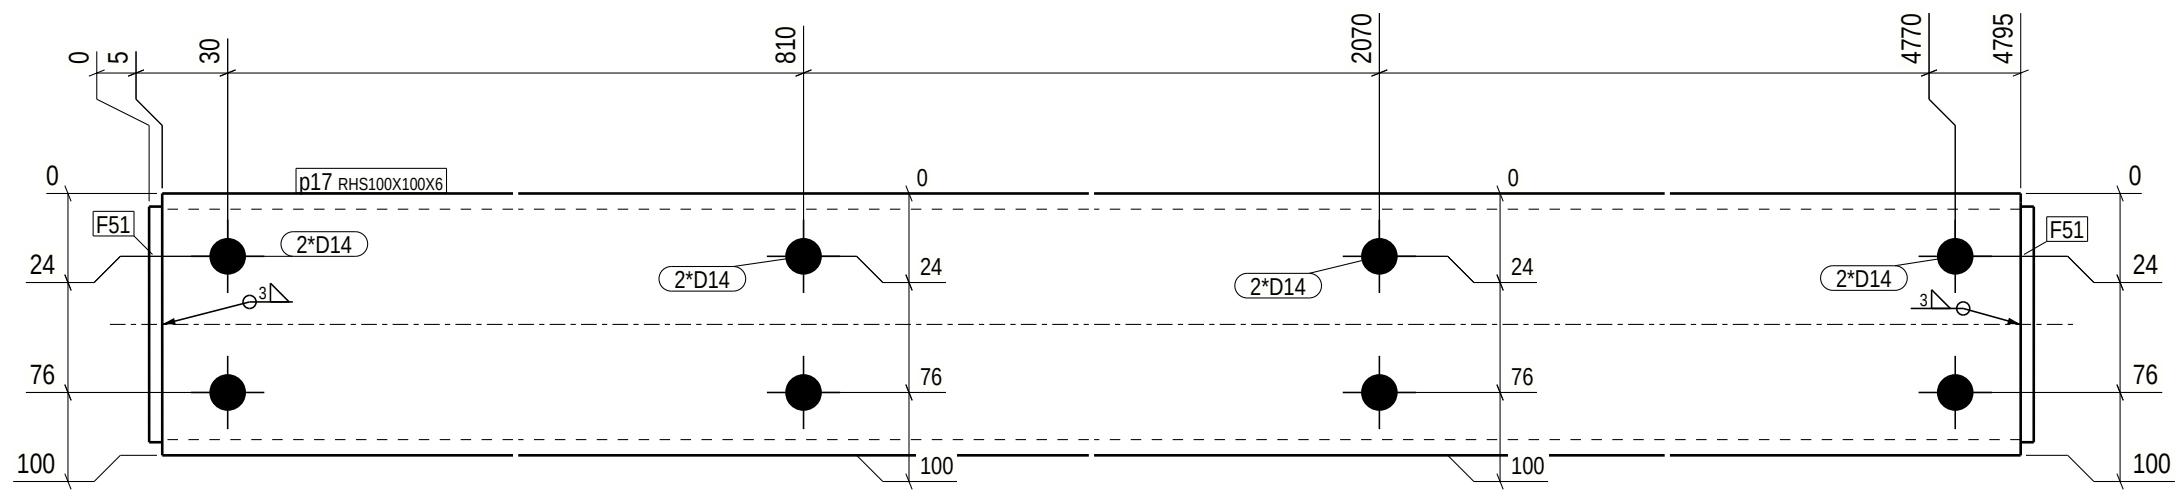

**GENERAL NOTES:** For your safety, check weight before handling:  
0-5kg Light 5-15kg Normal 15+kg Heavy

ALL WELDS ARE 4 UNLESS NOTED ON DRAWING

MATERIAL LIST FOR ASSEMBLY MK'D **p.17**

| Mark  | Profile      | Material | No. | Length | Area | Weight  |
|-------|--------------|----------|-----|--------|------|---------|
| p17   | RHS100X100X6 | S355J2H  | 1   | 4790   | 1.8  | 81.0 !! |
| F51   | FL5*90       | S355J2   | 2   | 90     | 0.0  | 0.3     |
| Total |              |          |     | 1.9    |      | 81.7    |

|                         |                                |     |
|-------------------------|--------------------------------|-----|
| Finish Class            | Standard                       |     |
| Surface treatment info: | Thickness/start point-> length | No. |

weld a = 4

| PHASE | QUANTITY |
|-------|----------|
| 1     | 1        |

|                                                      |                                      |                  |                    |
|------------------------------------------------------|--------------------------------------|------------------|--------------------|
| * o 3 0 4 8 0 - 1 * DS Stahlkonstruktion * A p 1 7 * |                                      |                  |                    |
| PROJECT                                              | Akkasæter Lager- og vedlikeholdshall | EXEC. CLASS      | EXC 2              |
| MEMBER                                               | Portomfatning                        | QUANTITY:        | 1                  |
| REVISION                                             | ISSUED: 03.11.2025                   | DRAFTER: ZLL     | PROJECT No 30480-1 |
|                                                      |                                      | BIM control: SST | DRAWING No. p.17   |