
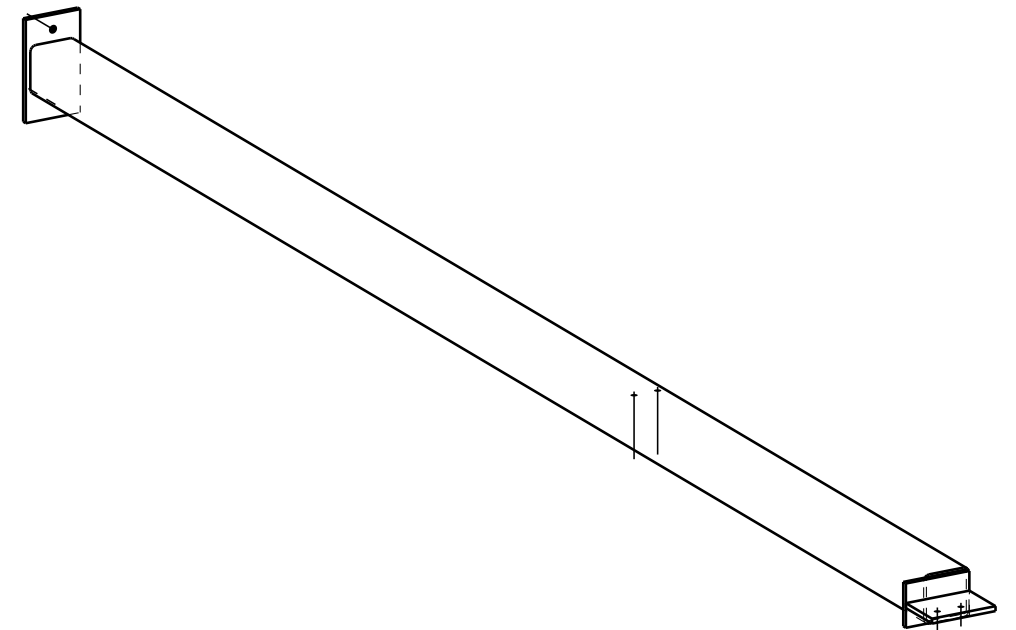
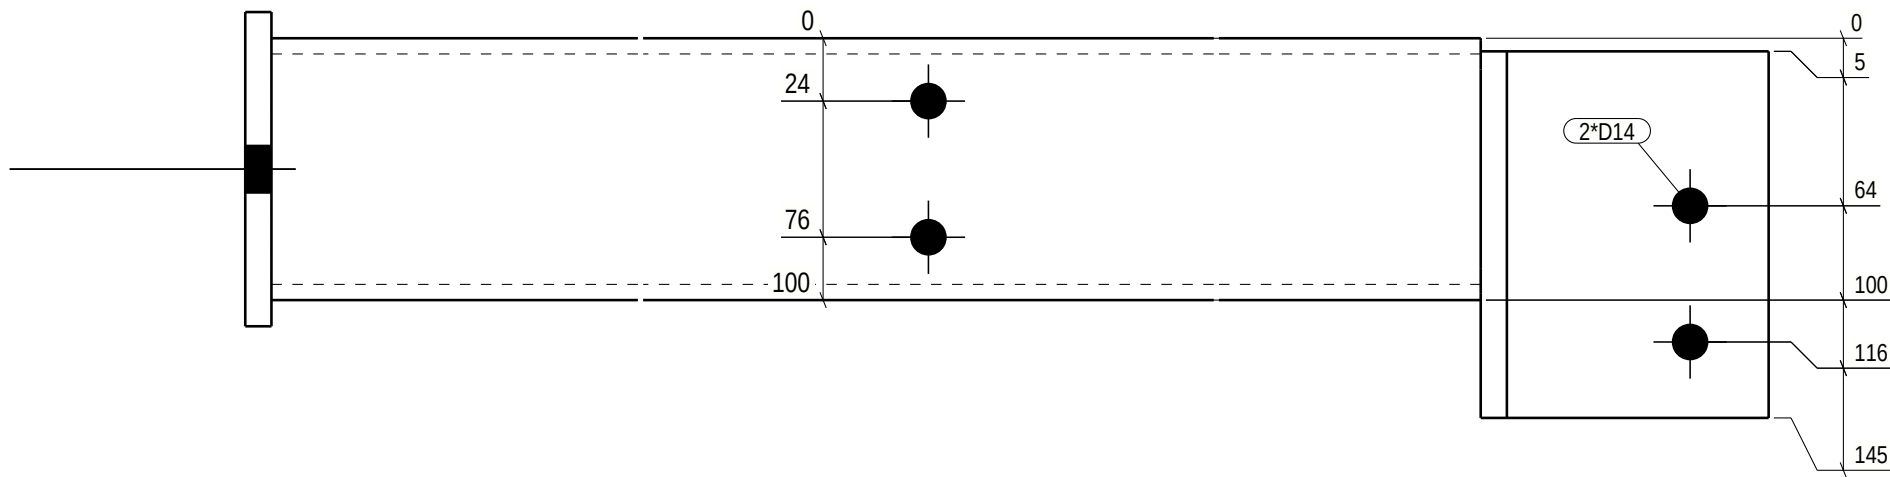
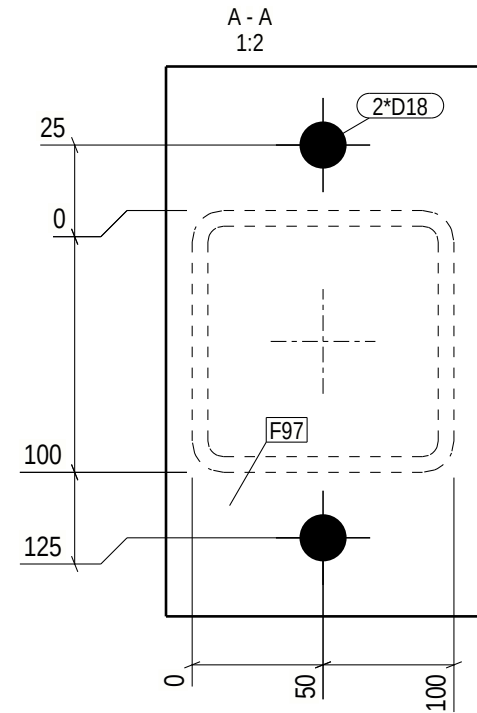


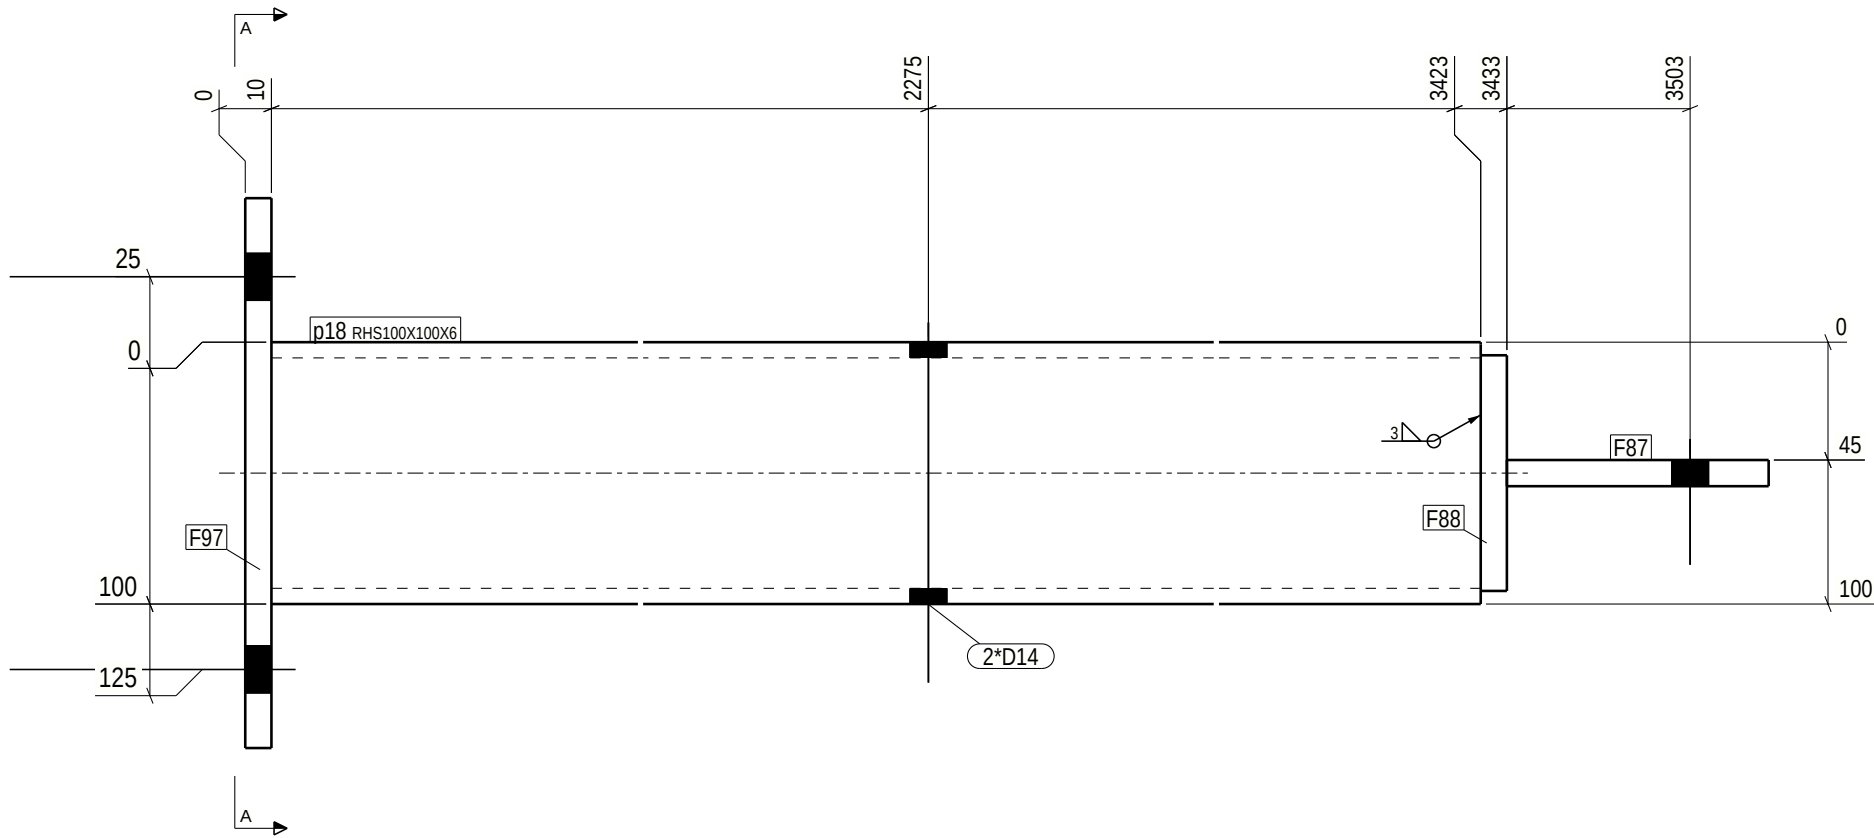

GENERAL NOTES: For your safety, check weight before handling:						
ALL WELDS ARE 4 UNLESS NOTED ON DRAWING						
MATERIAL LIST FOR ASSEMBLY MK'D p.18						
Mark	Profile	Material	No.	Length	Area	Weight
p18	RHS100X100X6	S355J2H	1	3413	1.3	57.7 !!
F87	FL10*100	S355J2	1	140	0.0	1.1
F88	FL10*90	S355J2	1	140	0.0	1.0
F97	FL10*120	S355J2	1	210	0.1	2.0
Total				1.4	61.8	

Finish Class
Standard

Surface treatment info:	Thickness/start point-> length	No.
-------------------------	--------------------------------	-----

weld a = 4

PHASE	QUANTITY
1	1

* o 3 0 4 8 0 - 1 * DS Stahlkonstruktion * A p 1 8 *			
PROJECT	Akkasæter Lager- og vedlikeholdshall	EXEC. CLASS	EXC 2
MEMBER	Portomfatning	QUANTITY:	1
REVISION	ISSUED: 03.11.2025	DRAFTER: ZLL	PROJECT No 30480-1
		BIM control: SST	DRAWING No. p.18