
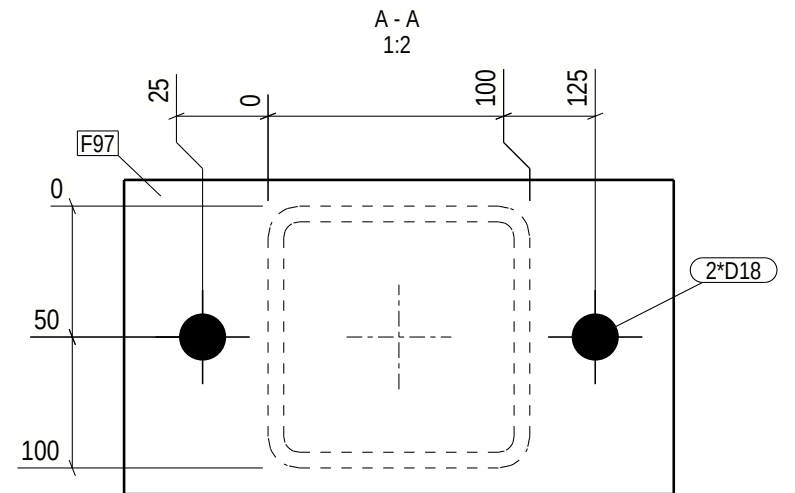
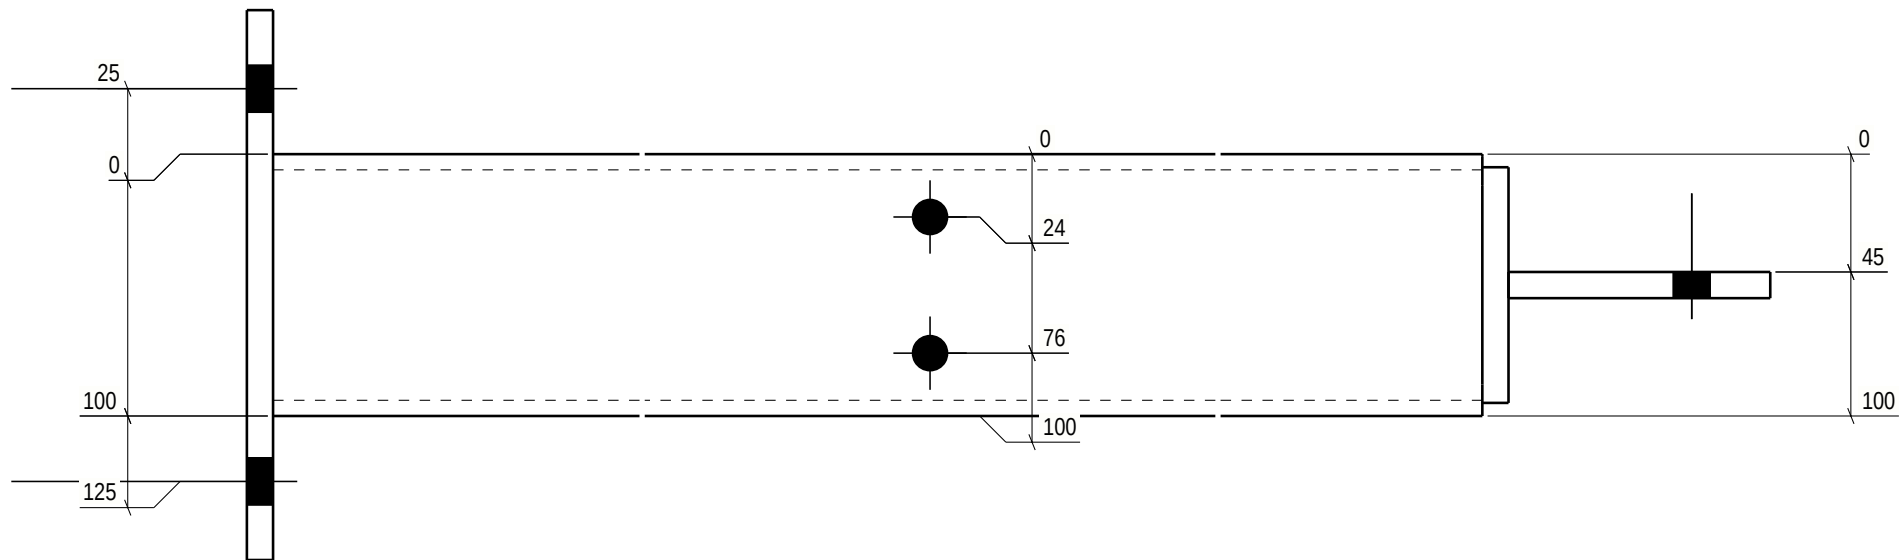


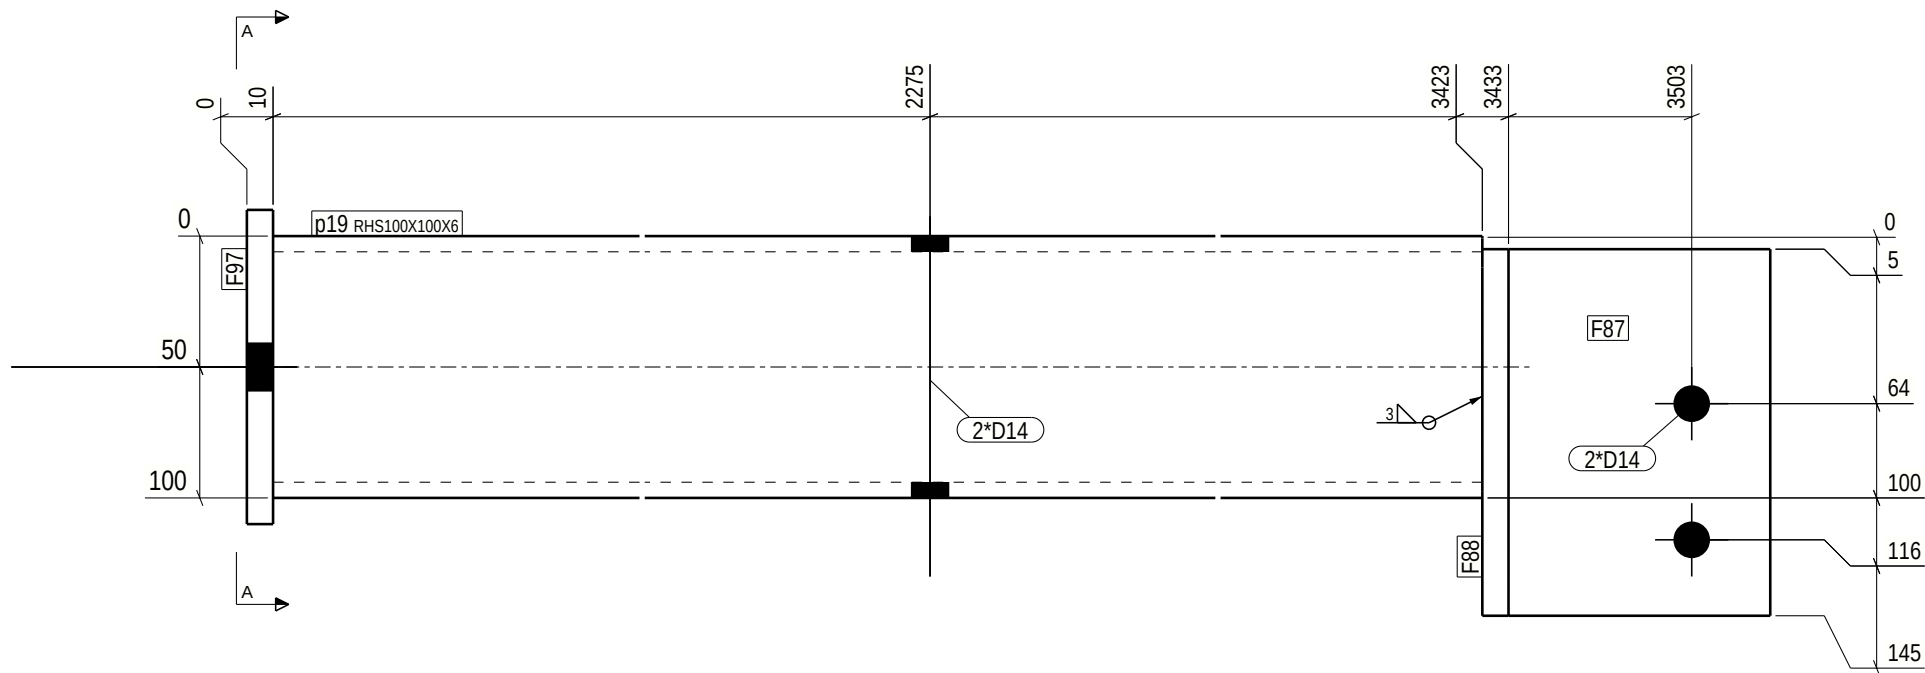

GENERAL NOTES: For your safety, check weight before handling:
0-5kg Light 5-15kg Normal 15+kg Heavy

ALL WELDS ARE 4 UNLESS NOTED ON DRAWING

MATERIAL LIST FOR ASSEMBLY MK'D p.19 1 No. Required

Mark	Profile	Material	No.	Length	Area	Weight
p19	RHS100X100X6	S355J2H	1	3413	1.3	57.7 !!
F87	FL10*100	S355J2	1	140	0.0	1.1
F88	FL10*90	S355J2	1	140	0.0	1.0
F97	FL10*120	S355J2	1	210	0.1	2.0
Total				1.4	61.8	

Finish Class
Standard

Surface treatment info: Thickness/start point-> length No.

weld a = 4

PHASE	QUANTITY
1	1

* o 3 0 4 8 0 - 1 * DS Steelkonstruktion * A p 1 9 *			
PROJECT	Akkasæter Lager- og vedlikeholdshall	EXEC. CLASS	EXC 2
MEMBER	Portomfatning	QUANTITY:	1 PROJECT No 30480-1
REVISION	ISSUED: 03.11.2025	DRAFTER: ZLL SST	DRAWING No. p.19