
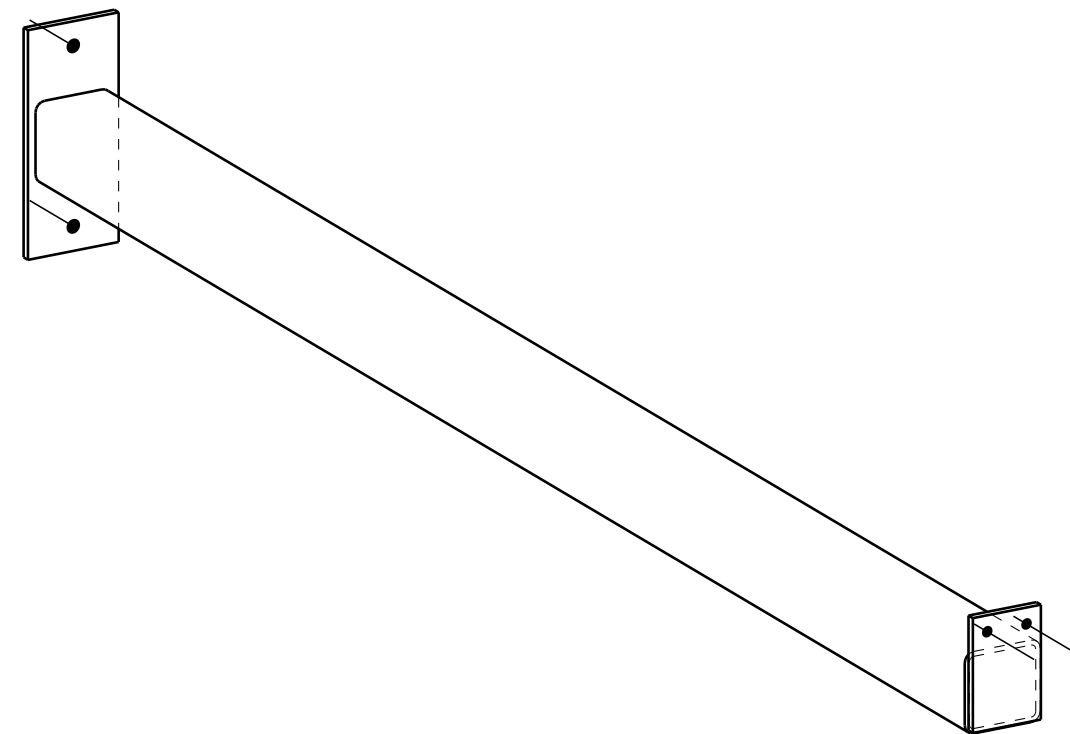
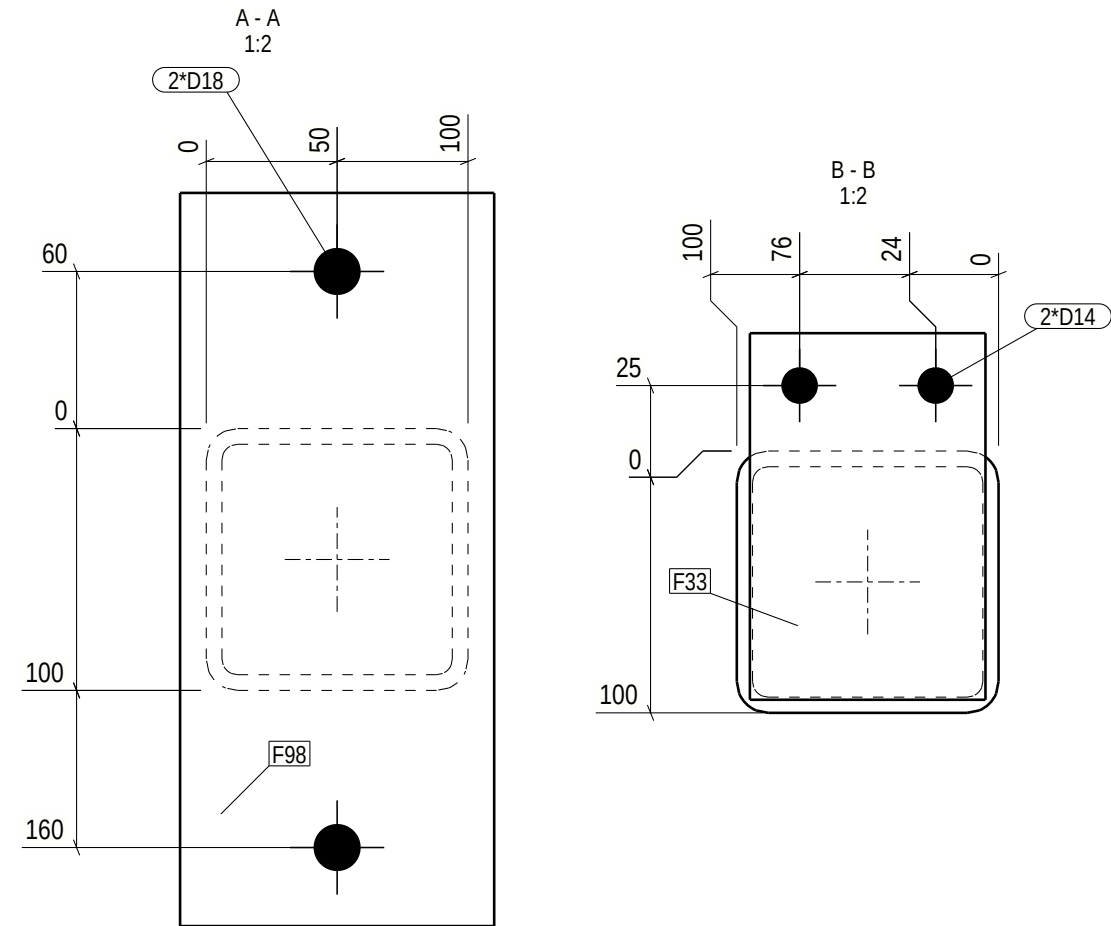


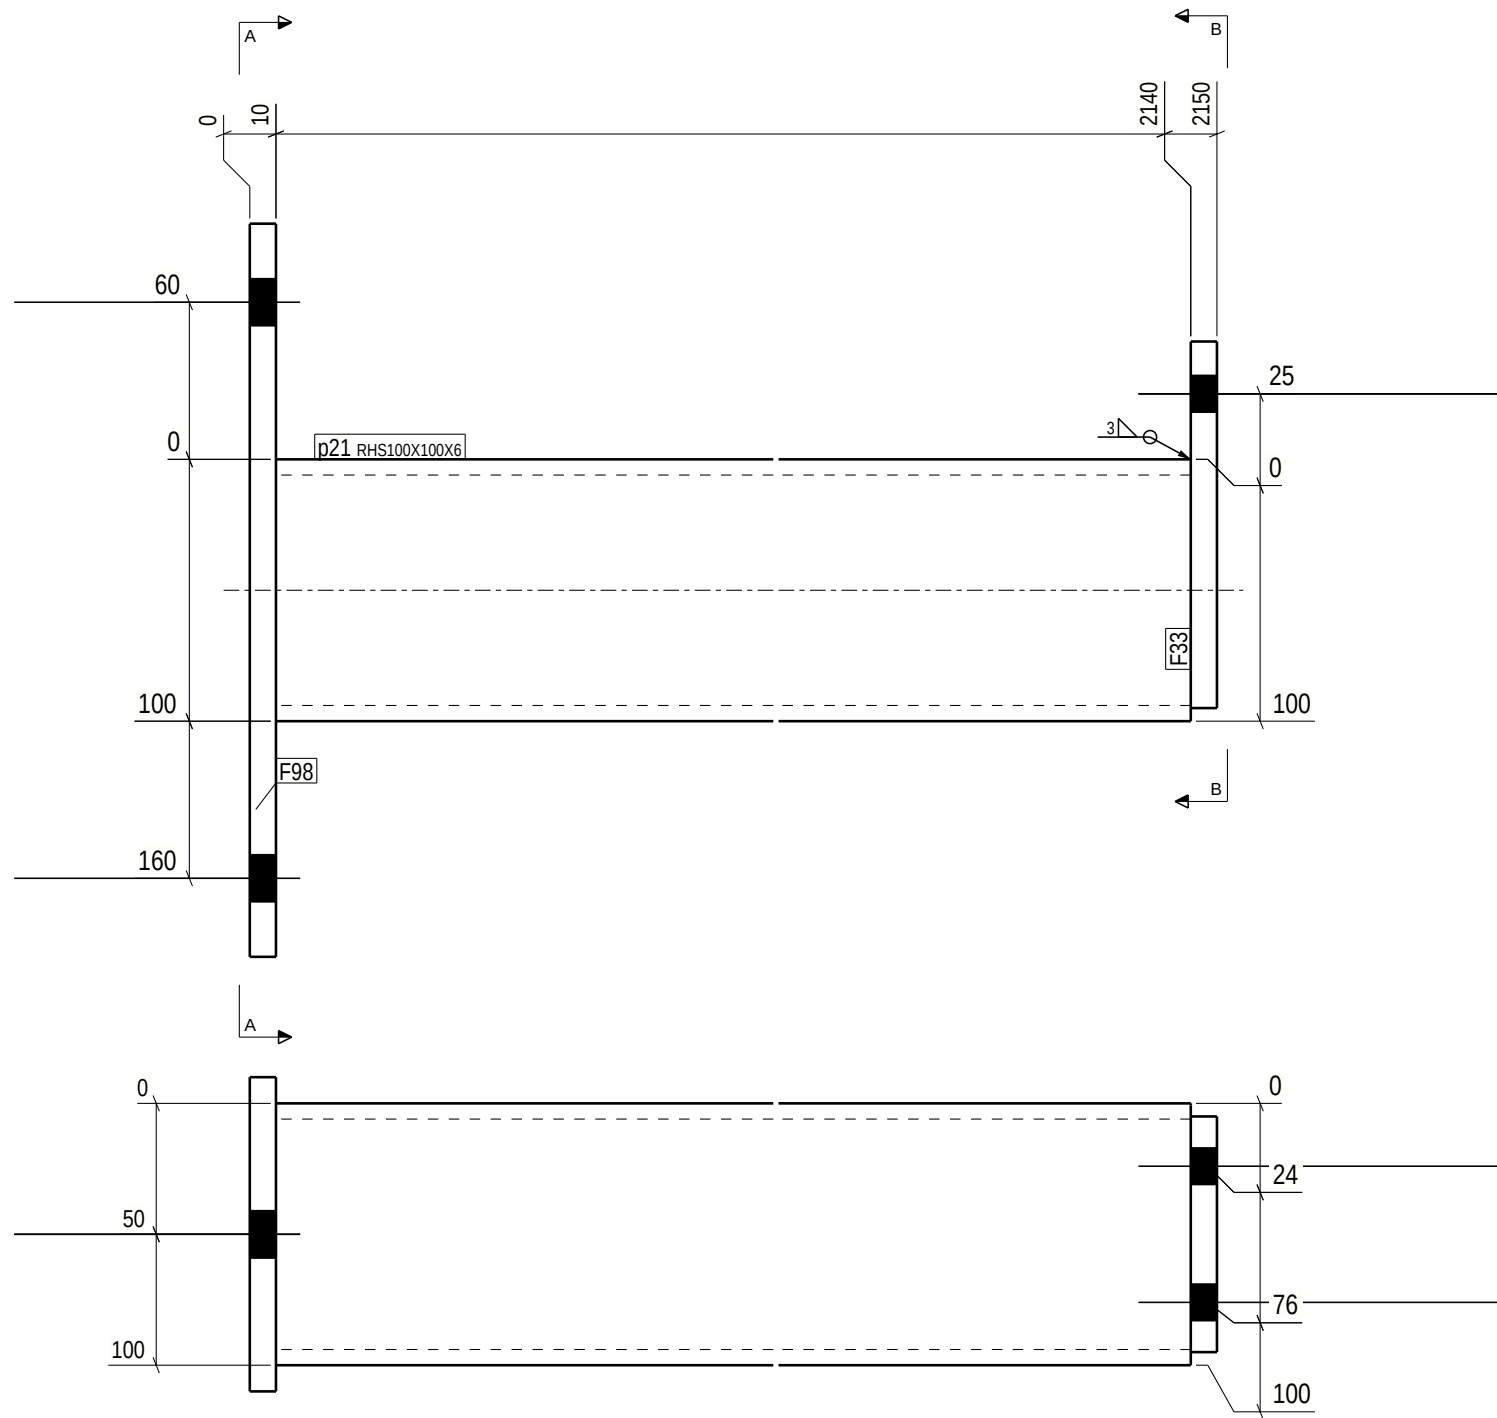

GENERAL NOTES:						
For your safety, check weight before handling:						
ALL WELDS ARE 4 UNLESS NOTED ON DRAWING						
MATERIAL LIST FOR ASSEMBLY MK'D p.21						
Mark	Profile	Material	No.	Length	Area	Weight
p21	RHS100X100X6	S355J2H	1	2130	0.8	36.0 !!
F33	FL10*90	S355J2	1	140	0.0	1.0
F98	FL10*120	S355J2	1	280	0.1	2.6
Total					0.9	39.7

Finish Class
Standard

Surface treatment info:	Thickness/start point-> length	No.
-------------------------	--------------------------------	-----

weld a = 4

PHASE	QUANTITY
1	3

* o 3 0 4 8 0 - 1 * DS Steelkonstruktion * A p 2 1 *					
PROJECT	Akkasæter Lager- og vedlikeholdshall			EXEC. CLASS	EXC 2
MEMBER	Portomfatning		QUANTITY:	3	PROJECT No 30480-1
REVISION		ISSUED: 03.11.2025	DRAFTER: ZLL	BIM control: SST	DRAWING No. p.21