
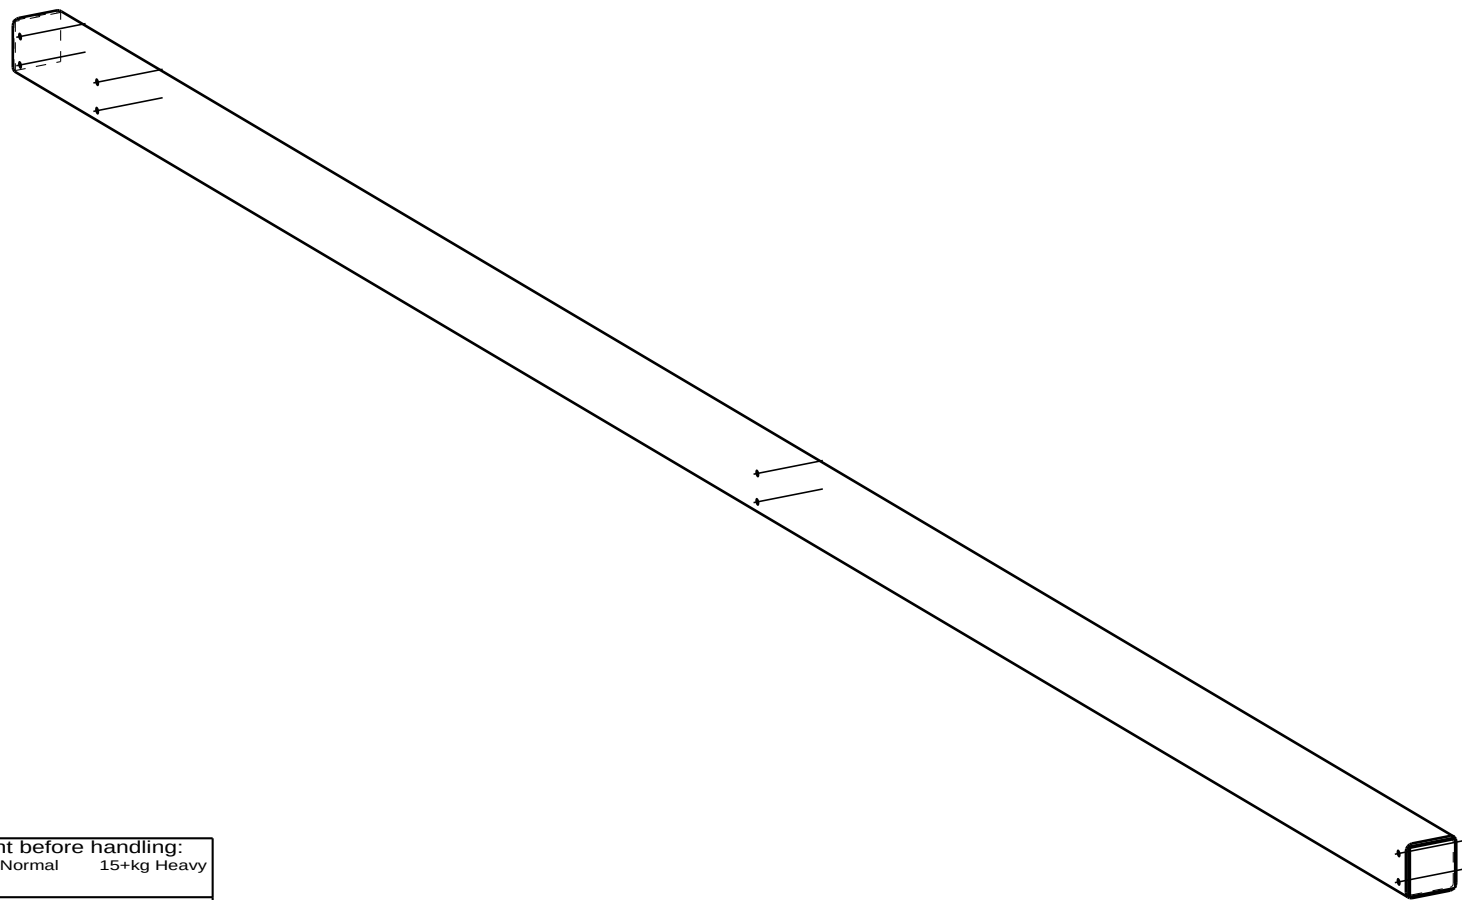
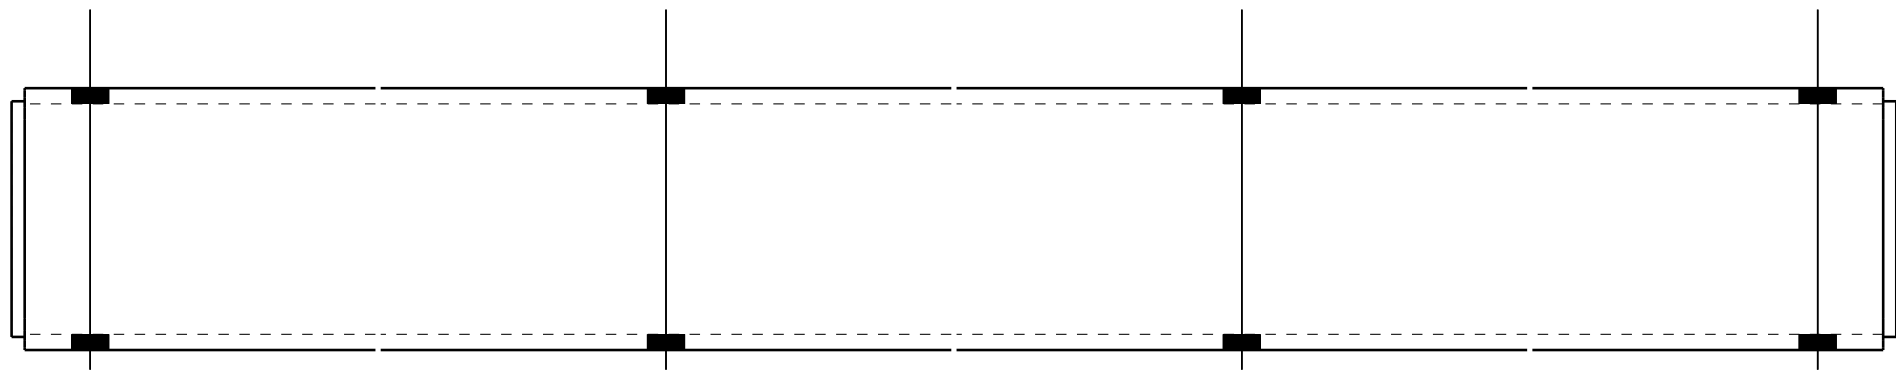


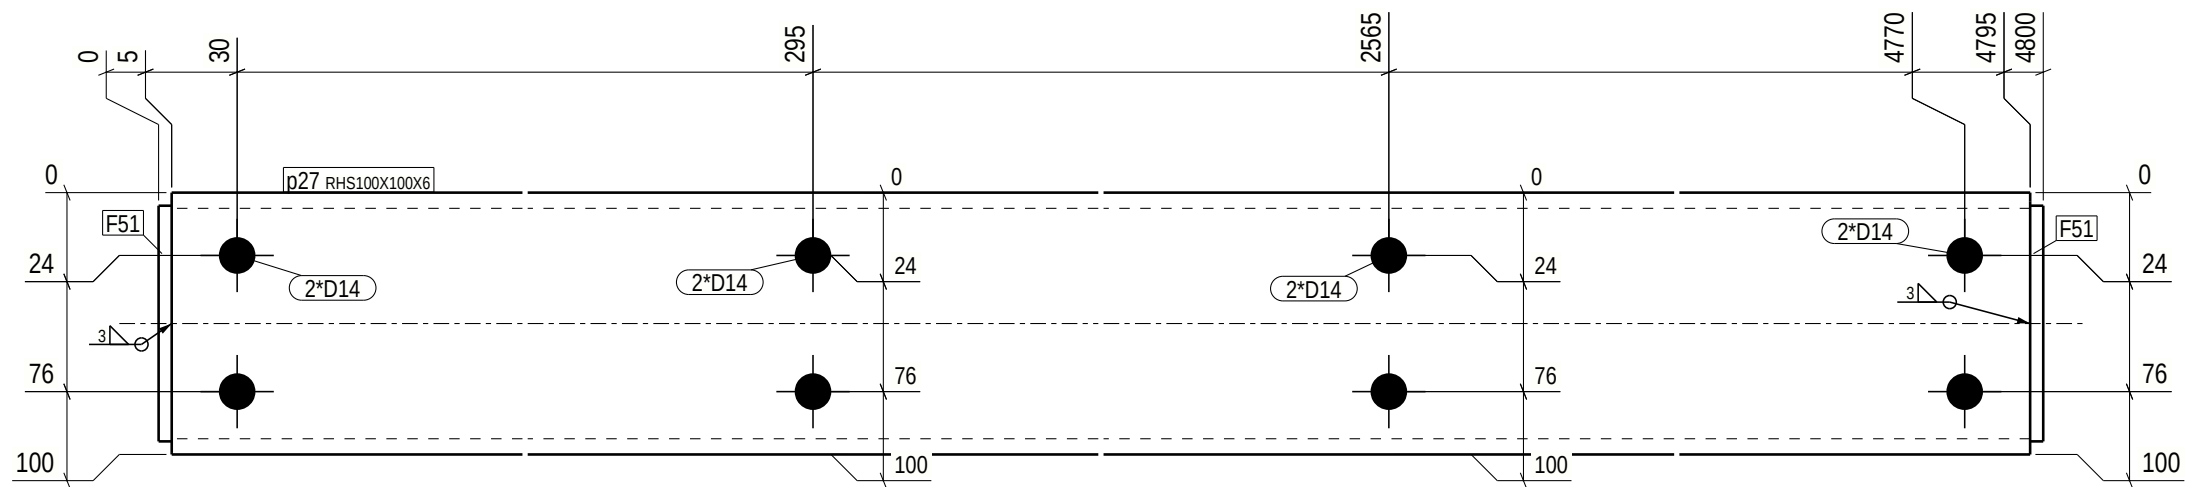

GENERAL NOTES:						
For your safety, check weight before handling:						
0-5kg Light 5-15kg Normal 15+kg Heavy						
ALL WELDS ARE 4 UNLESS NOTED ON DRAWING						
MATERIAL LIST FOR ASSEMBLY MK'D p.27						
Mark	Profile	Material	No.	Length	Area	Weight
p27	RHS100X100X6	S355J2H	1	4790	1.8	81.0 !!
F51	FL5*90	S355J2	2	90	0.0	0.3
Total				1.9	81.7	

Finish Class
Standard

Surface treatment info:	Thickness/start point--> length	No.
-------------------------	---------------------------------	-----

weld a = 4

PHASE	QUANTITY
1	4

* o 3 0 4 8 0 - 1 *			
DS Steelkonstruktion			
* A p 2 7 *			
PROJECT	Akkasæter Lager- og vedlikeholdshall	EXEC. CLASS	EXC 2
MEMBER	Portomfatning	QUANTITY:	4
REVISION	ISSUED: 03.11.2025	DRAFTER: ZLL	PROJECT No 30480-1
		BIM control: SST	DRAWING No. p.27