
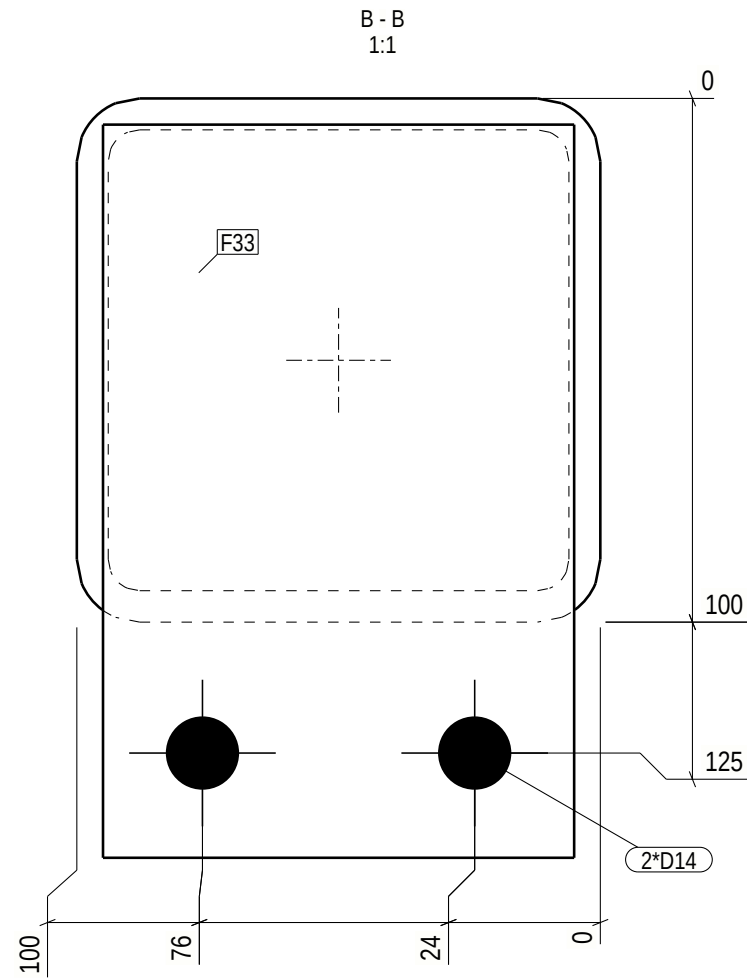


Tekla Structures

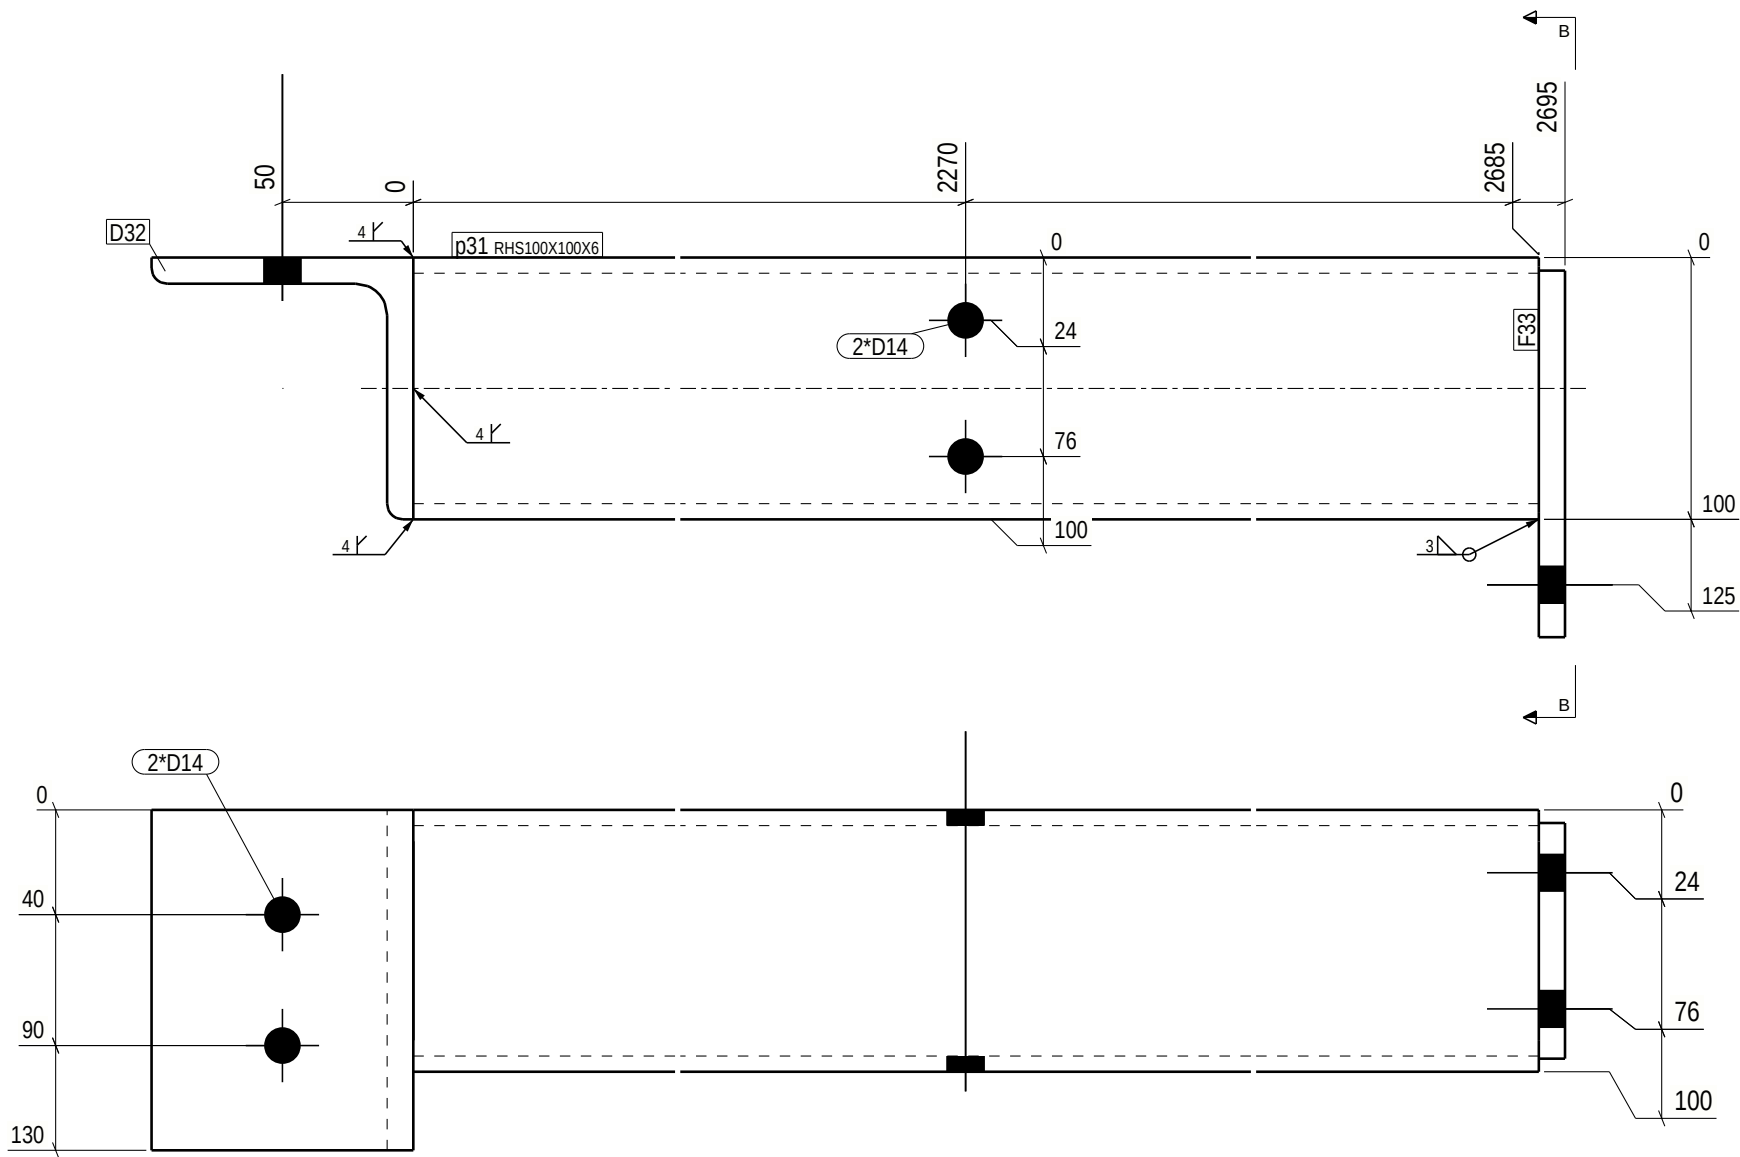

GENERAL NOTES:						
For your safety, check weight before handling:						
ALL WELDS ARE 4 UNLESS NOTED ON DRAWING						
MATERIAL LIST FOR ASSEMBLY MK'D p.31						
Mark	Profile	Material	No.	Length	Area	Weight
p31	RHS100X100X6	S355J2H	1	2685	1.0	45.4 !!
D32	L100*10	S355J2	1	130	0.1	2.0
F33	FL10*90	S355J2	1	140	0.0	1.0
Total				1.1		48.4

Finish Class
Standard

Surface treatment info:	Thickness/start point-> length	No.
-------------------------	--------------------------------	-----

weld a = 4

PHASE	QUANTITY
1	1

* o 3 0 4 8 0 - 1 * DS Skalkonstruktion * A p 3 1 *			
PROJECT	Akkasæter Lager- og vedlikeholdshall	EXEC. CLASS	EXC 2
MEMBER	Portomfatning	QUANTITY:	1
REVISION	ISSUED: 05.11.2025	DRAFTER: ZLL	PROJECT No 30480-1
		BIM control: SST	DRAWING No. p.31