
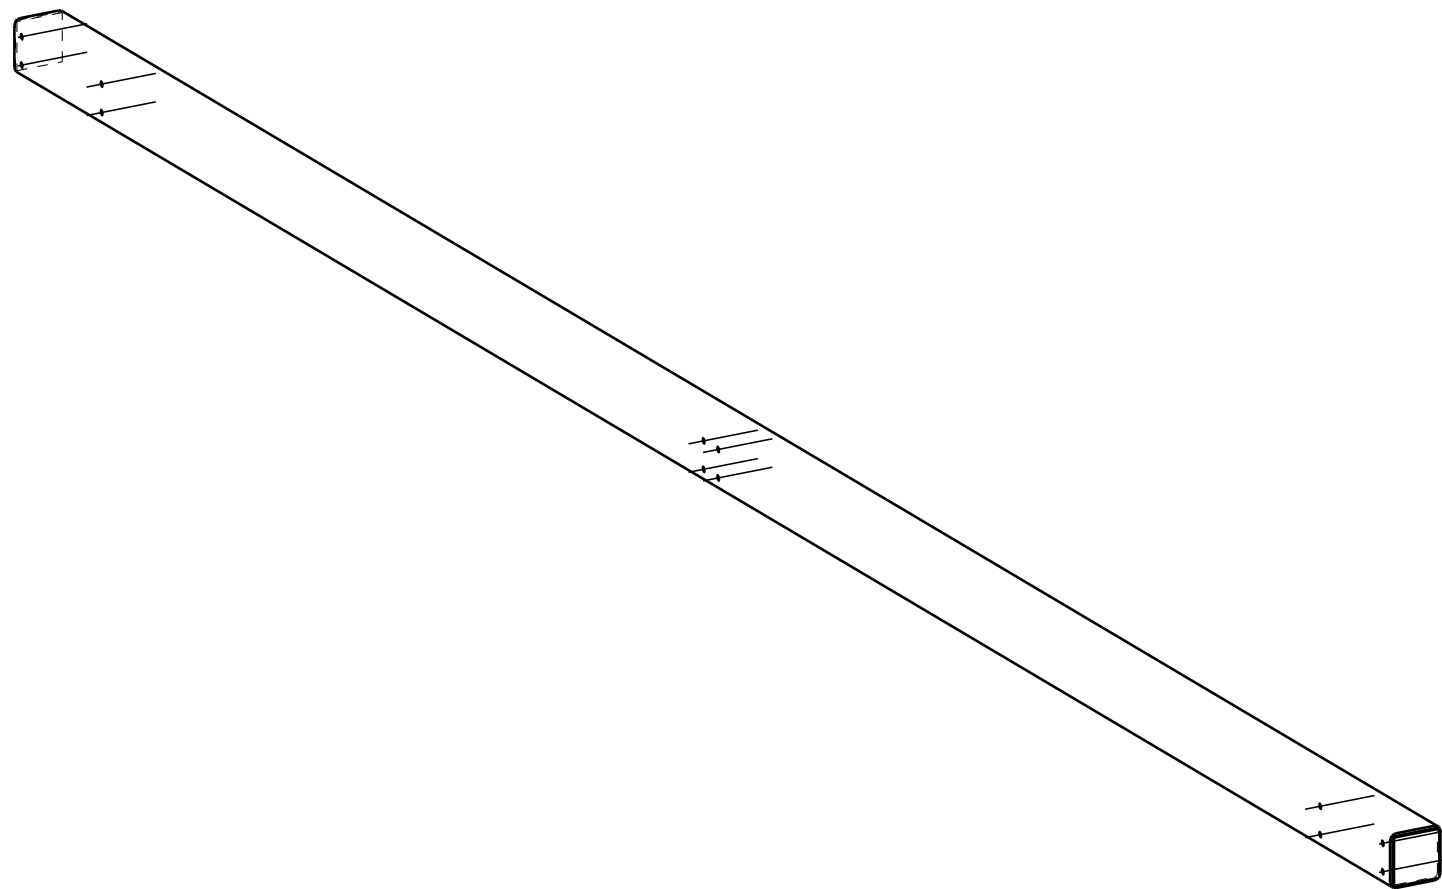


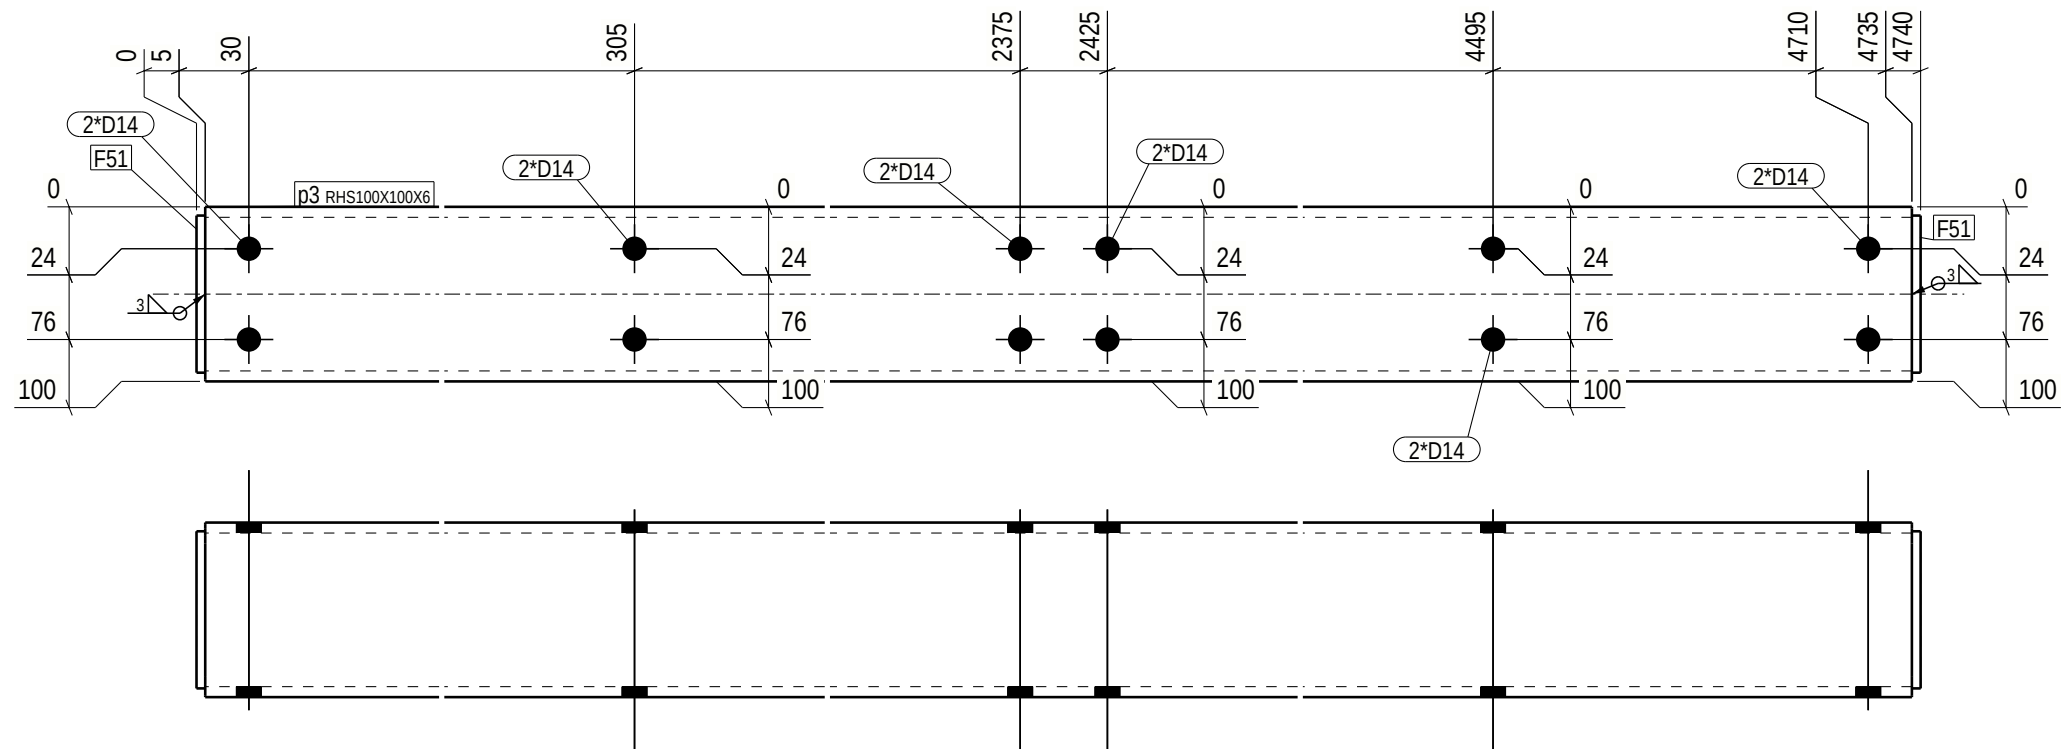

GENERAL NOTES: For your safety, check weight before handling:						
ALL WELDS ARE 4 UNLESS NOTED ON DRAWING						
MATERIAL LIST FOR ASSEMBLY MK'D p.3						
Mark	Profile	Material	No.	Length	Area	Weight
p3	RHS100X100X6	S355J2H	1	4730	1.8	80.0 !!
F51	FL5*90	S355J2	2	90	0.0	0.3
Total				1.9	80.6	

Finish Class
Standard

Surface treatment info:	Thickness/start point-> length	No.
-------------------------	--------------------------------	-----

weld a = 4

PHASE	QUANTITY
1	4

* o 3 0 4 8 0 - 1 * DS Stahlkonstruktion * A p 3 *			
PROJECT	Akkasæter Lager- og vedlikeholdshall	EXEC. CLASS	EXC 2
MEMBER	Portomfatning	QUANTITY:	4
REVISION	ISSUED: 03.11.2025	DRAFTER: ZLL	PROJECT No. 30480-1
		BIM control: SST	DRAWING No. p.3