


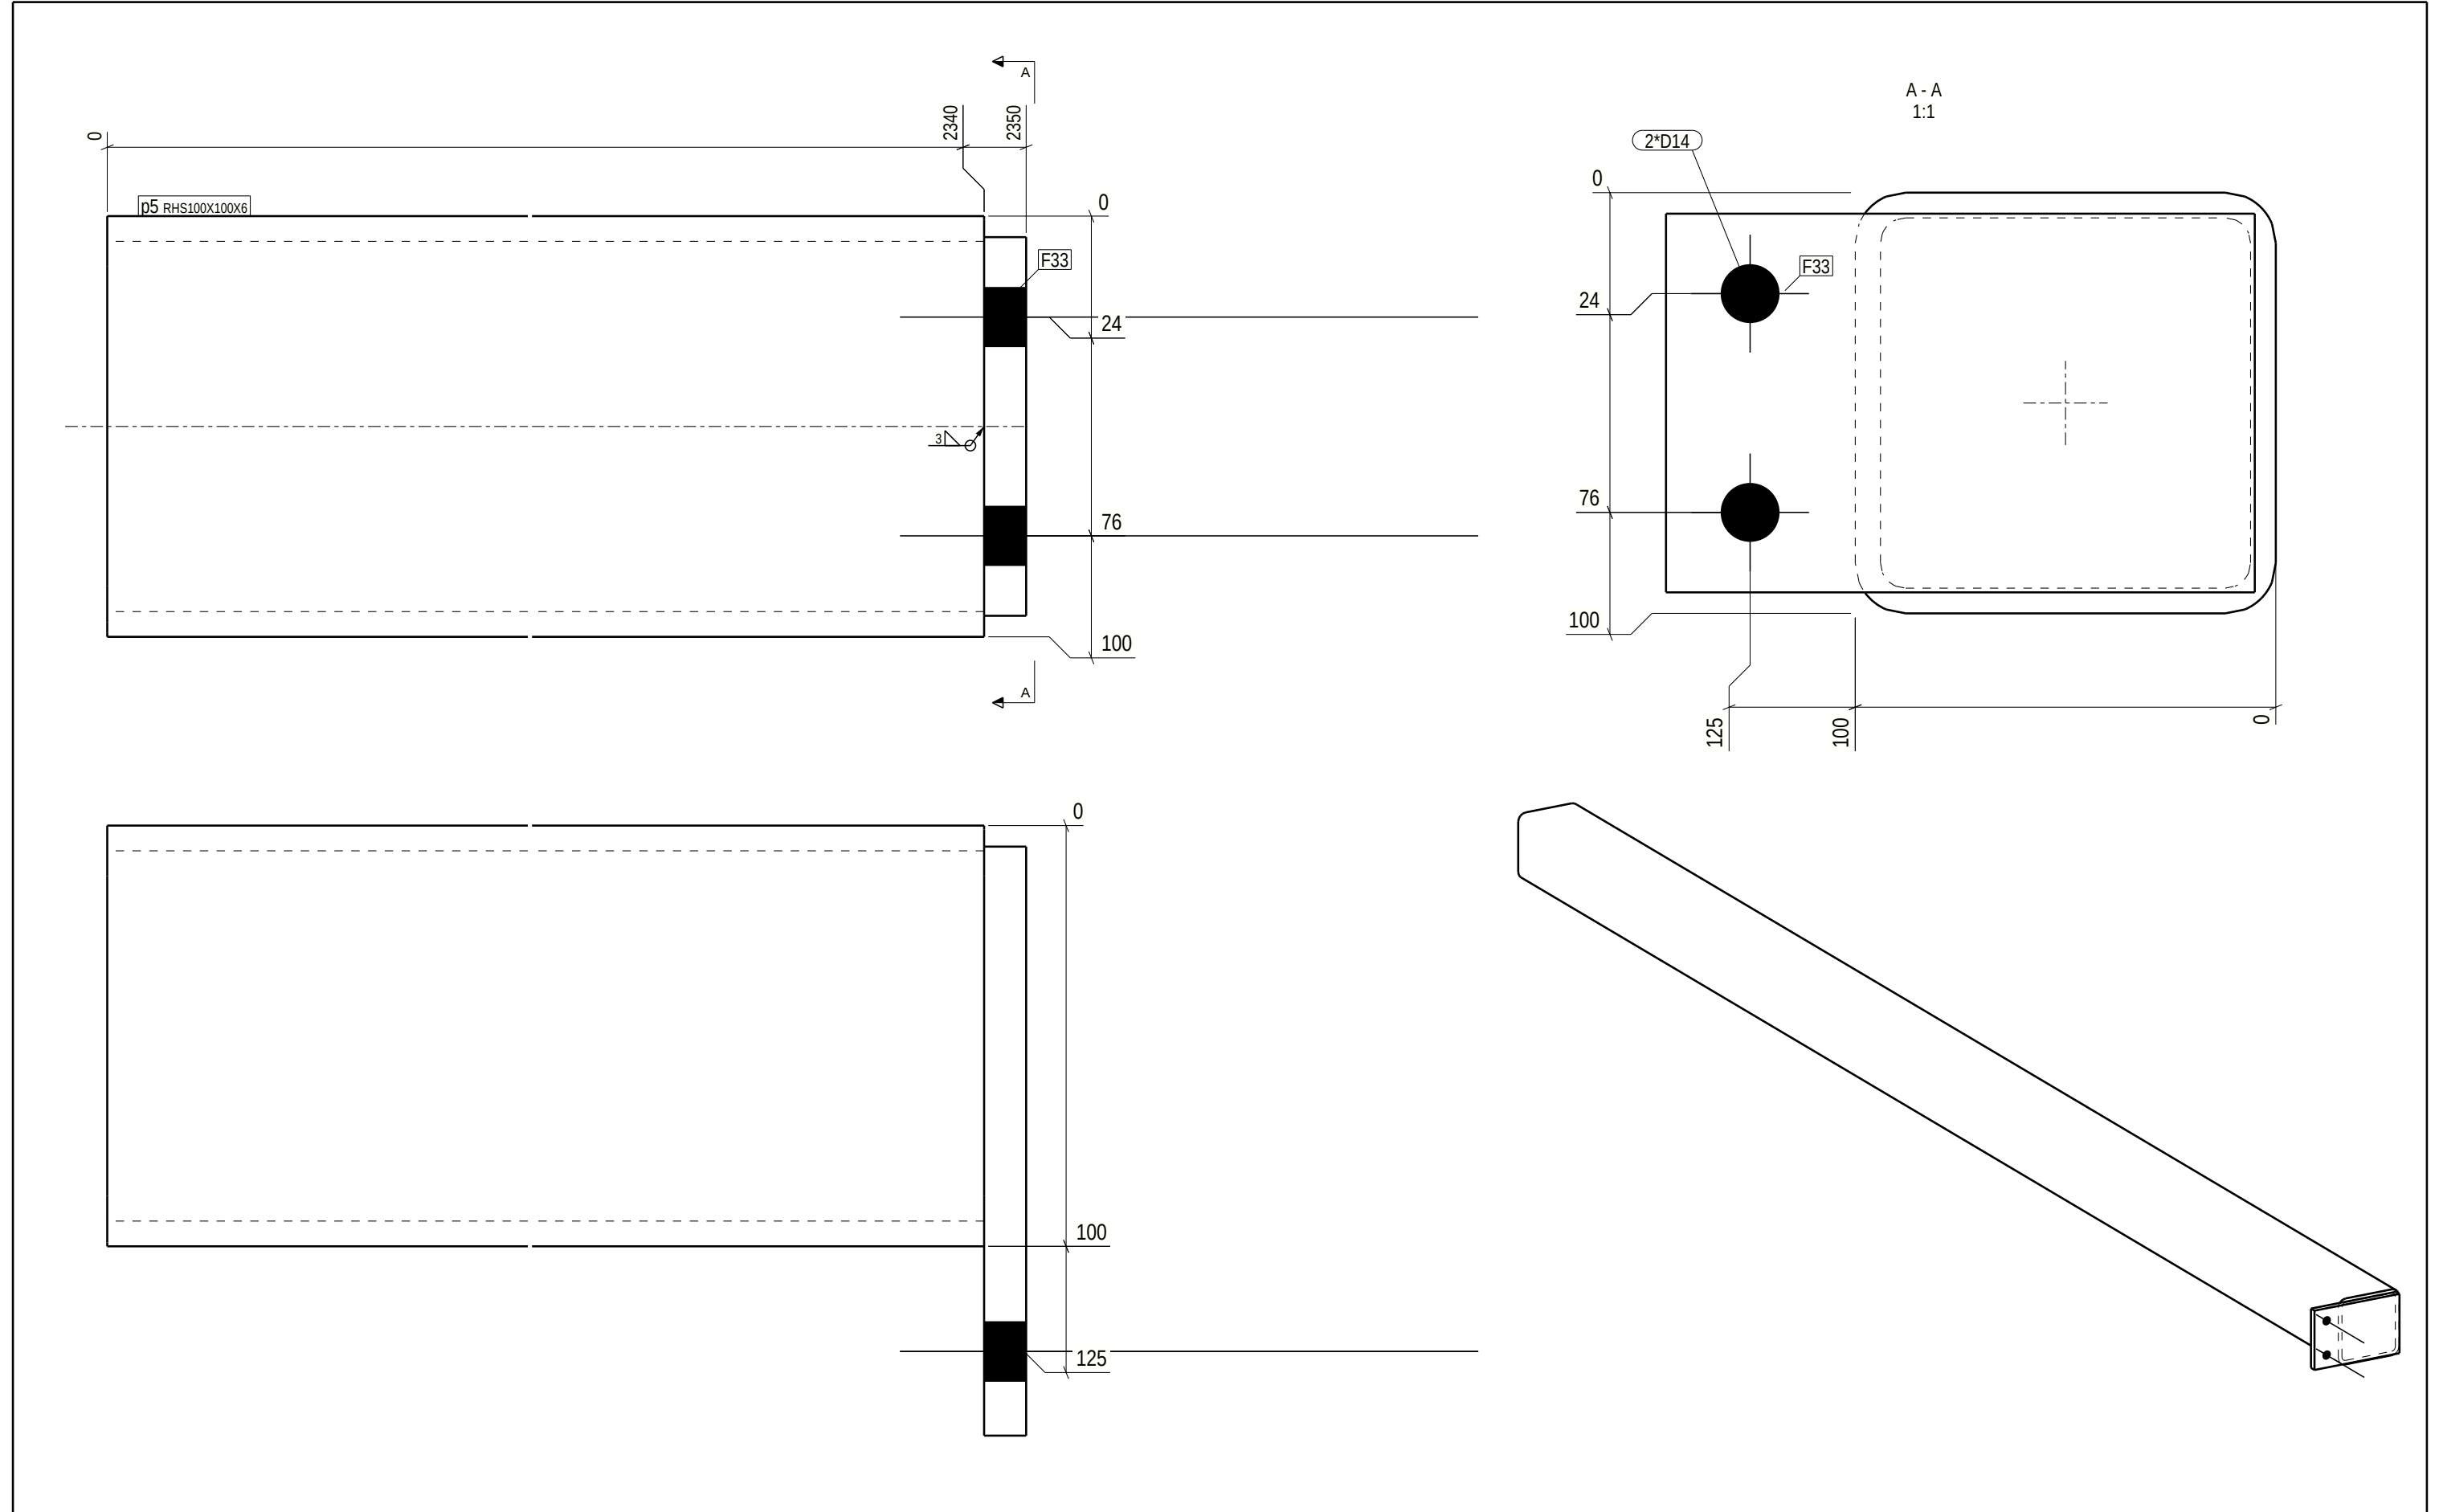

GENERAL NOTES:							For your safety, check weight before handling:						
							0-5kg Light 5-15kg Normal 15+kg Heavy						
ALL WELDS ARE 4							UNLESS NOTED ON DRAWING						
MATERIAL LIST FOR ASSEMBLY MK'D							p.5						
Mark	Profile	Material	No.	Length	Area	Weight	1 No. Required						
p5	RHS100X100X6	S355J2H	1	2340	0.9	39.6 !!							
F33	FL10*90	S355J2	1	140	0.0	1.0							
Total					0.9	40.6							
							Finish Class Standard						
Surface treatment info:							Thickness/start point-> length						
							No.						

PHASE	QUANTITY
1	1

weld a = 4

PROJECT	Akkasæter Lager- og vedlikeholdshall	EXEC. CLASS	EXC 2
MEMBER	Portomfatning	QUANTITY:	1
REVISION		ISSUED:	03.11.2025
		DRAFTER:	ZLL
		BIM control:	SST
PROJECT No		30480-1	
DRAWING No.		p.5	

* o 3 0 4 8 0 - 1 *

DS Stillkonstruksjon

* A p 5 *