
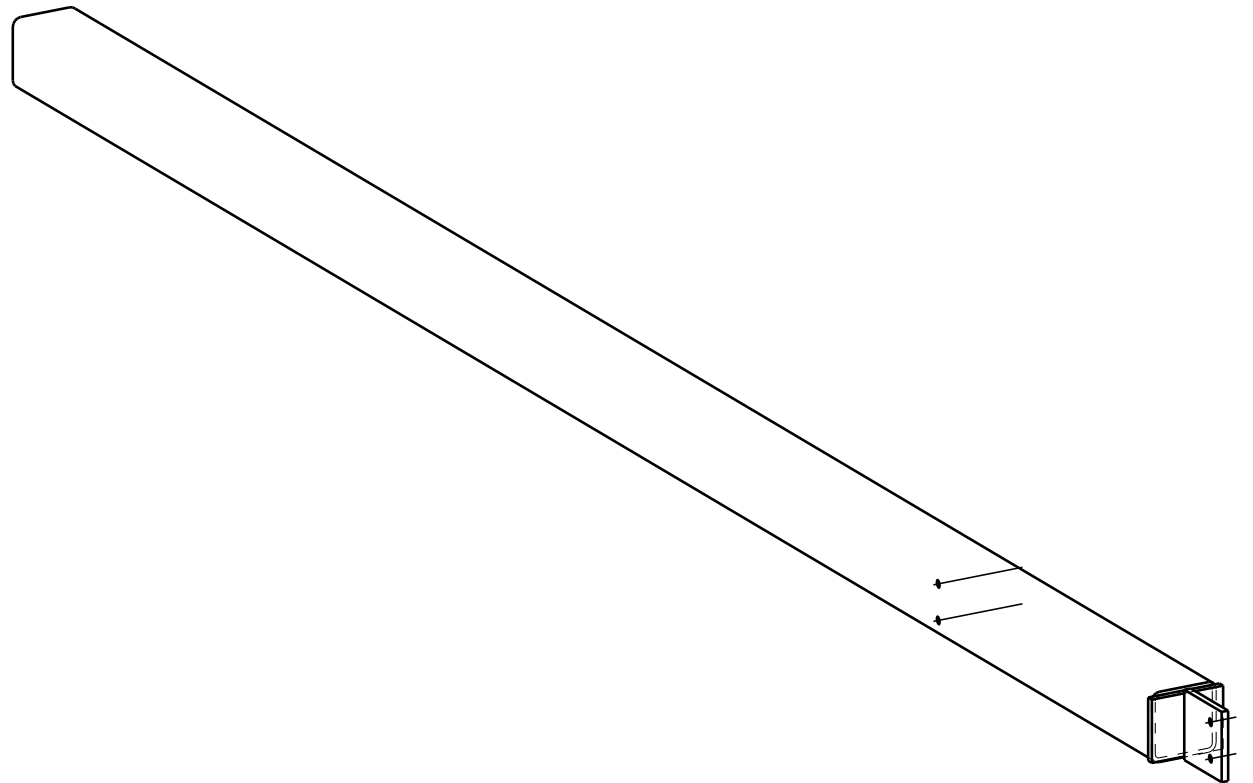


Tekla Structures

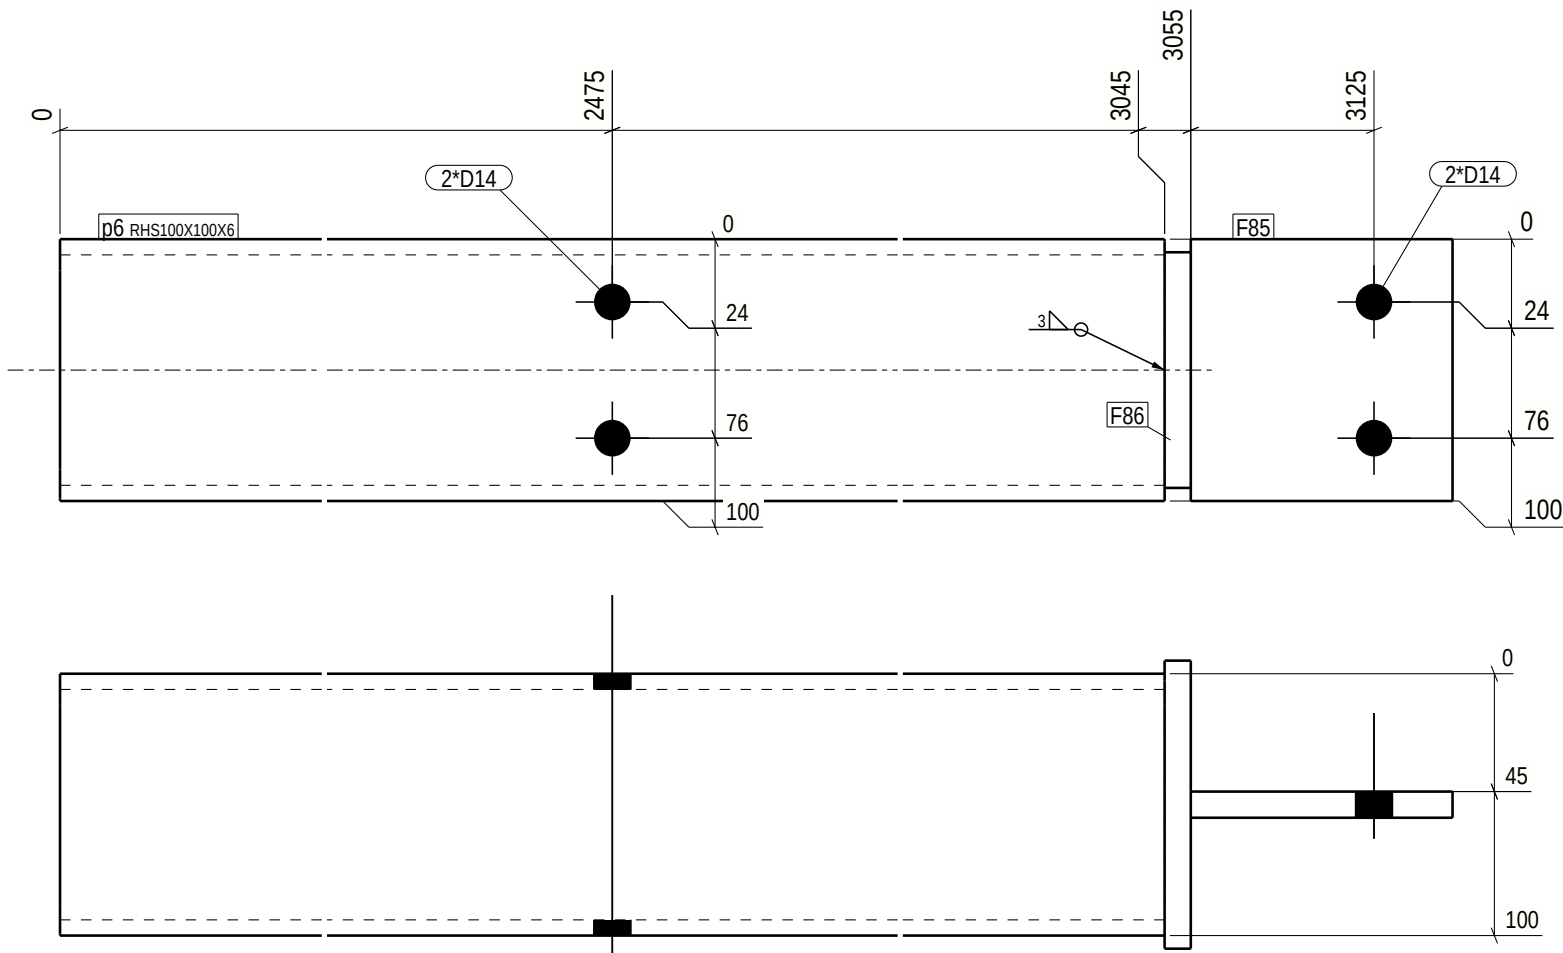

GENERAL NOTES:						
For your safety, check weight before handling:						
0-5kg Light 5-15kg Normal 15+kg Heavy						
ALL WELDS ARE 4 UNLESS NOTED ON DRAWING						
MATERIAL LIST FOR ASSEMBLY MK'D p.6						
1 No. Required						
Mark	Profile	Material	No.	Length	Area	Weight
p6	RHS100X100X6	S355J2H	1	3045	1.2	51.5 !!
F85	FL10*100	S355J2	1	100	0.0	0.8
F86	FL10*90	S355J2	1	110	0.0	0.8
Total				1.2	53.1	

Finish Class
Standard

Surface treatment info:	Thickness/start point-> length	No.
-------------------------	--------------------------------	-----

weld a = 4

PHASE	QUANTITY
1	1

* o 3 0 4 8 0 - 1 * DS Steelkonstruktion * A p 6 *					
PROJECT	Akkasæter Lager- og vedlikeholdshall			EXEC. CLASS	EXC 2
MEMBER	Portomfatning		QUANTITY:	1	PROJECT No 30480-1
REVISION		ISSUED: 03.11.2025	DRAFTER: ZLL	BIM control: SST	DRAWING No. p.6