


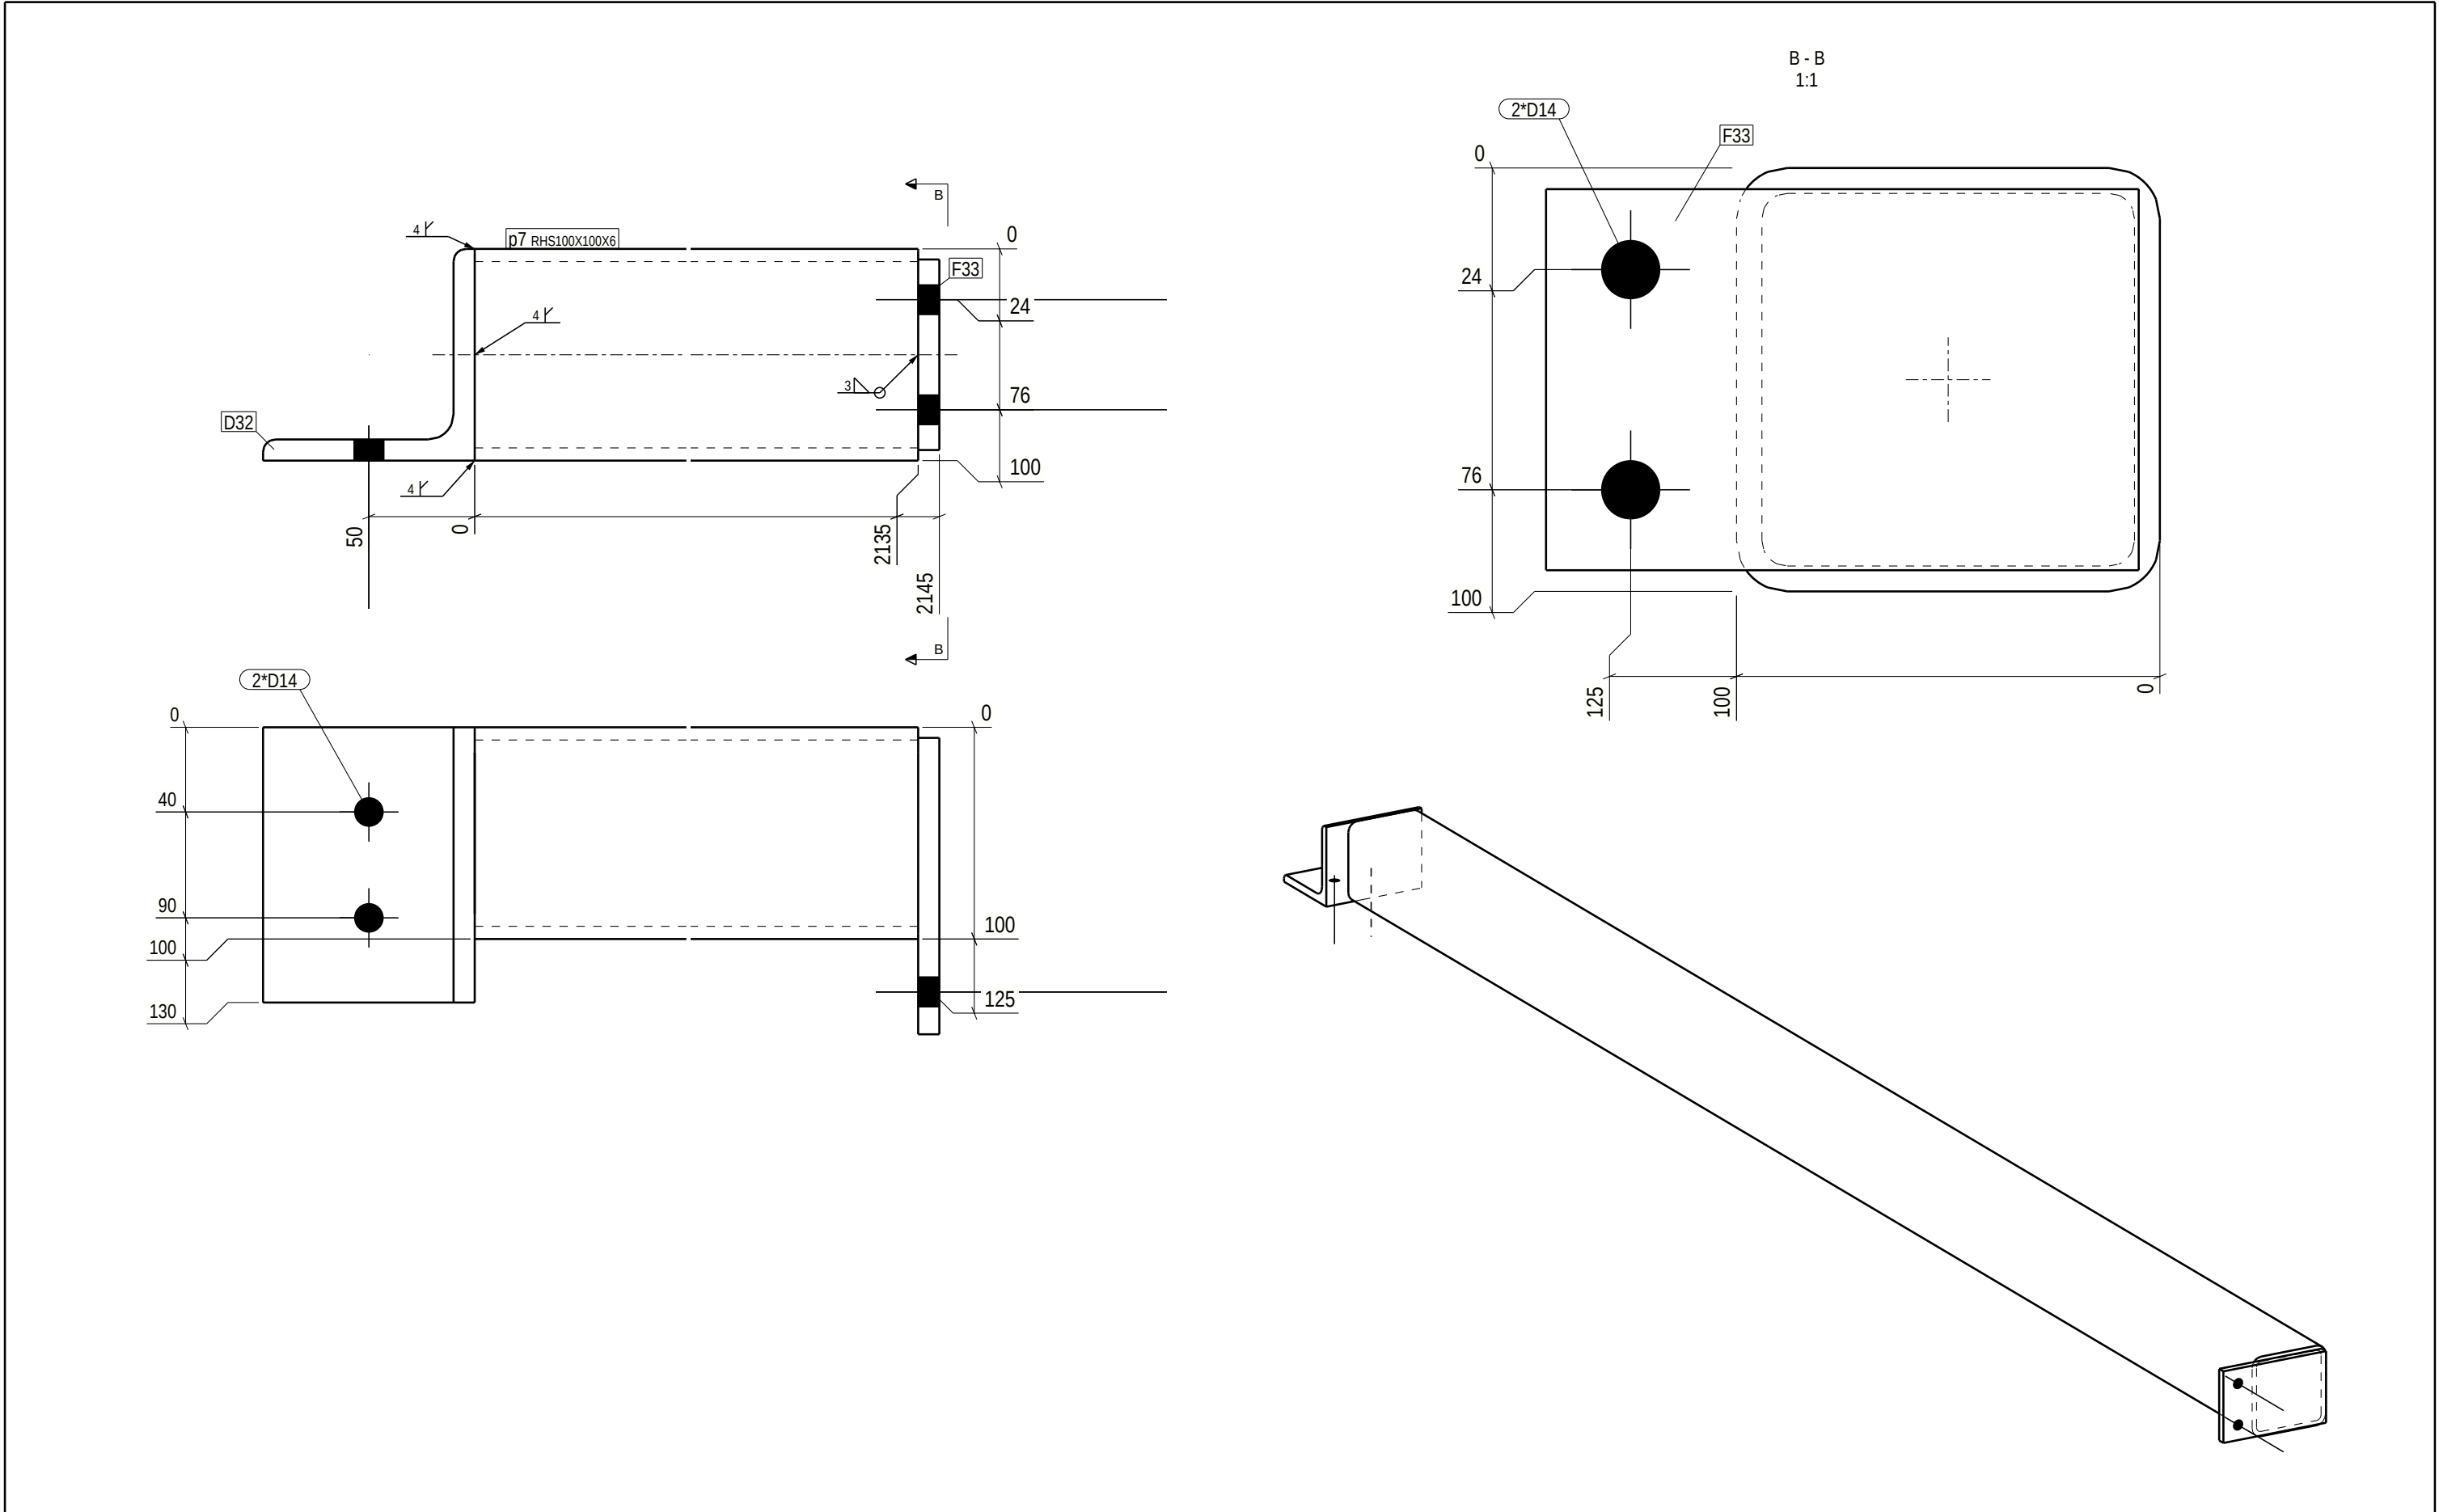

GENERAL NOTES:						
For your safety, check weight before handling:						
ALL WELDS ARE 4 UNLESS NOTED ON DRAWING						
MATERIAL LIST FOR ASSEMBLY MK'D p.7						
Mark	Profile	Material	No.	Length	Area	Weight
p7	RHS100X100X6	S355J2H	1	2135	0.8	36.1 !!
D32	L100*10	S355J2	1	130	0.1	2.0
F33	FL10*90	S355J2	1	140	0.0	1.0
Total					0.9	39.1

Finish Class
Standard

Surface treatment info:	Thickness/start point-> length	No.
-------------------------	--------------------------------	-----

weld a = 4

PHASE	QUANTITY
1	2

* o 3 0 4 8 0 - 1 * DS Steelkonstruktion * A p 7 *					
PROJECT	Akkasæter Lager- og vedlikeholdshall			EXEC. CLASS	EXC 2
MEMBER	Portomfatning	QUANTITY:	2	PROJECT No	30480-1
REVISION		ISSUED:	03.11.2025	DRAFTER:	ZLL
		BIM control:	SST	DRAWING No.	p.7