


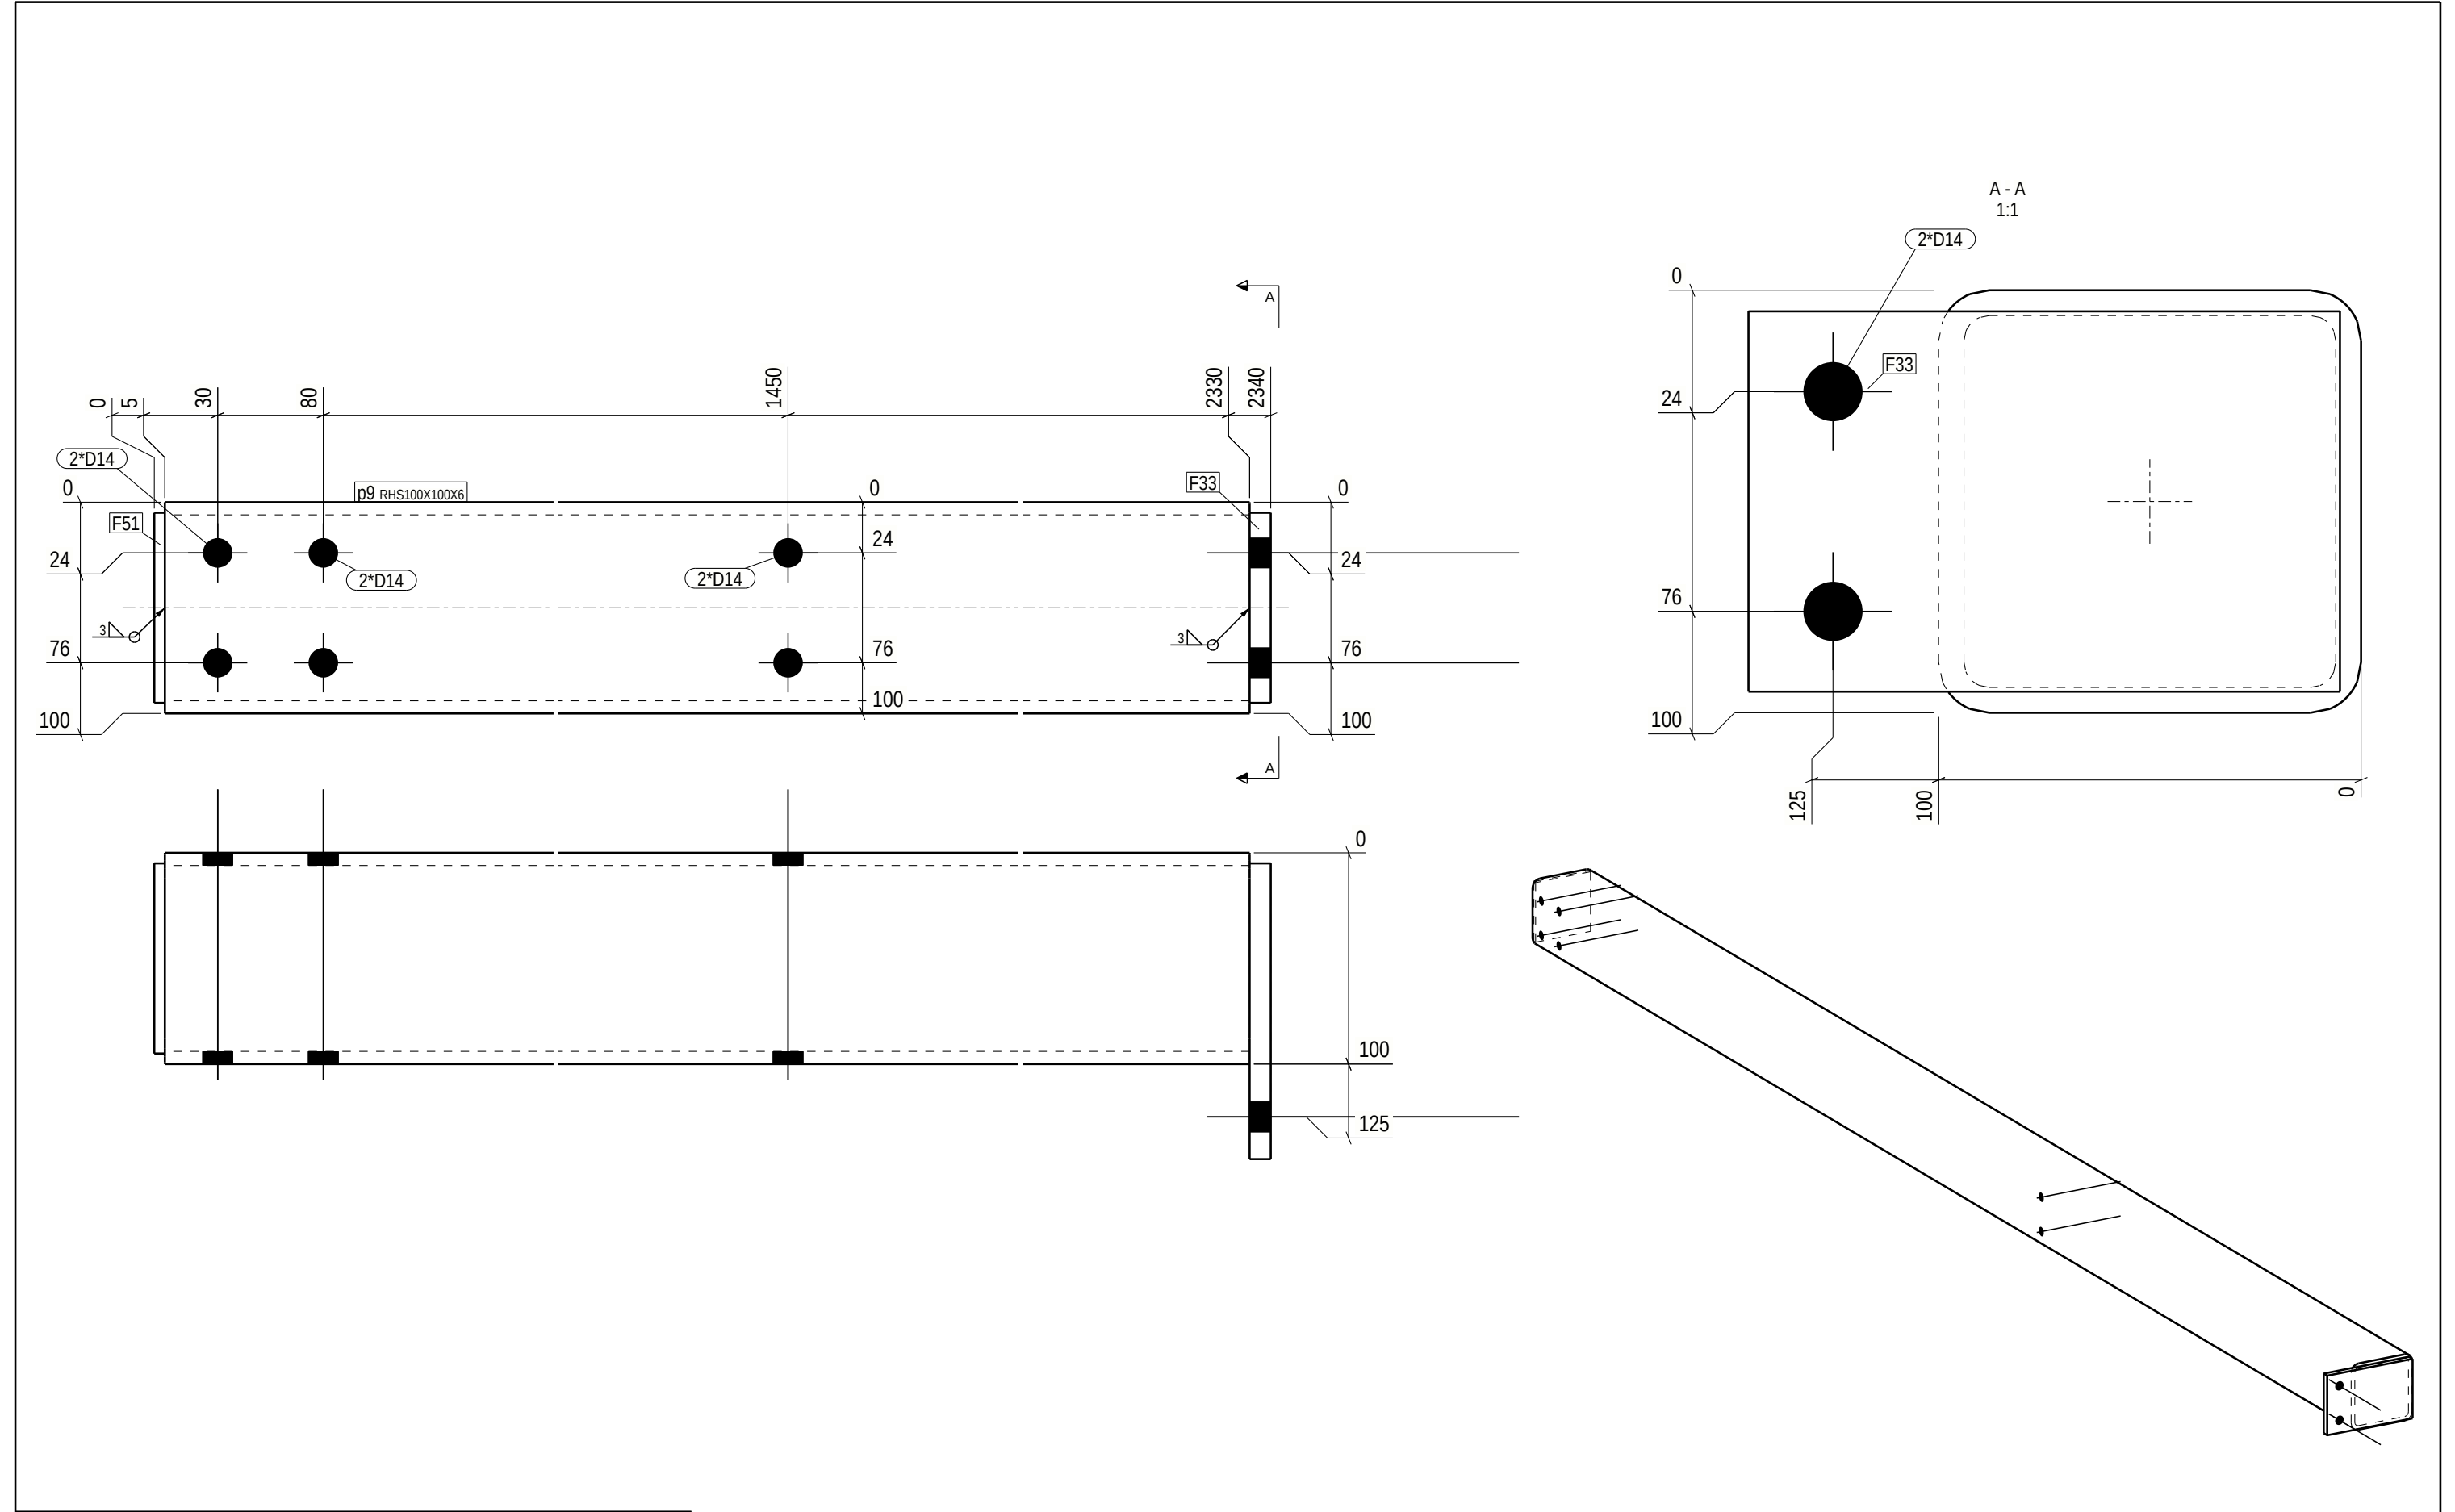

GENERAL NOTES:

For your safety, check weight before handling:
0-5kg Light 5-15kg Normal 15+kg Heavy

ALL WELDS ARE 4 UNLESS NOTED ON DRAWING

MATERIAL LIST FOR ASSEMBLY MK'D

1

No. Required

Mark	Profile	Material	No.	Length	Area	Weight
p9	RHS100X100X6	S355J2H	1	2325	0.9	39.3 !!
F33	FL10*90	S355J2	1	140	0.0	1.0
F51	FL5*90	S355J2	1	90	0.0	0.3
Total					0.9	40.6

Finish Class

Standard

Surface treatment info:

Thickness/start point-> length

No.

weld a = 4

PHASE

1

QUANTITY

1

* o 3 0 4 8 0 - 1 *

DS

Stahlkonstruktion

* A p 9 *

PROJECT

Akkasæter Lager- og vedlikeholdshall

EXEC. CLASS

EXC 2

MEMBER

Portomfatning

QUANTITY:

1

PROJECT No

30480-1

REVISION

ISSUED:

03.11.2025

DRAFTER:

ZLL

BIM control:

SST

DRAWING No.

p.9