
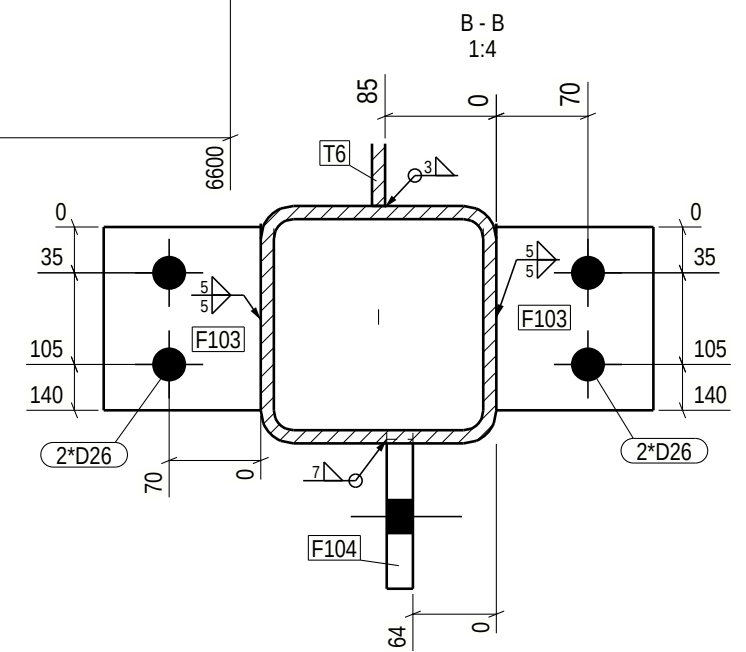
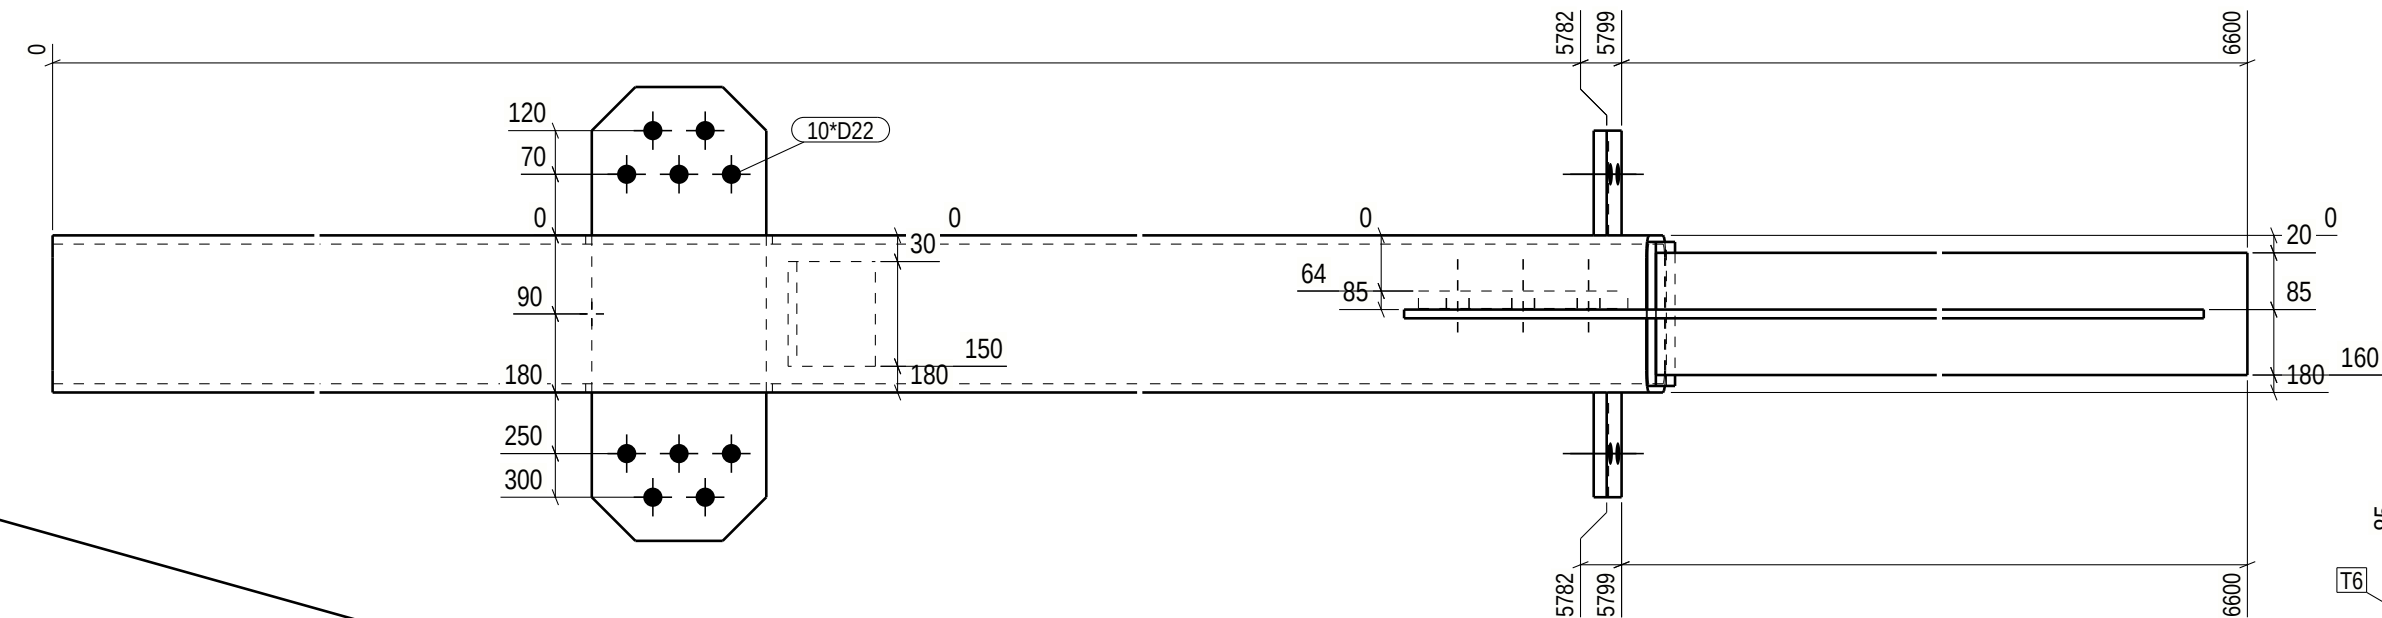


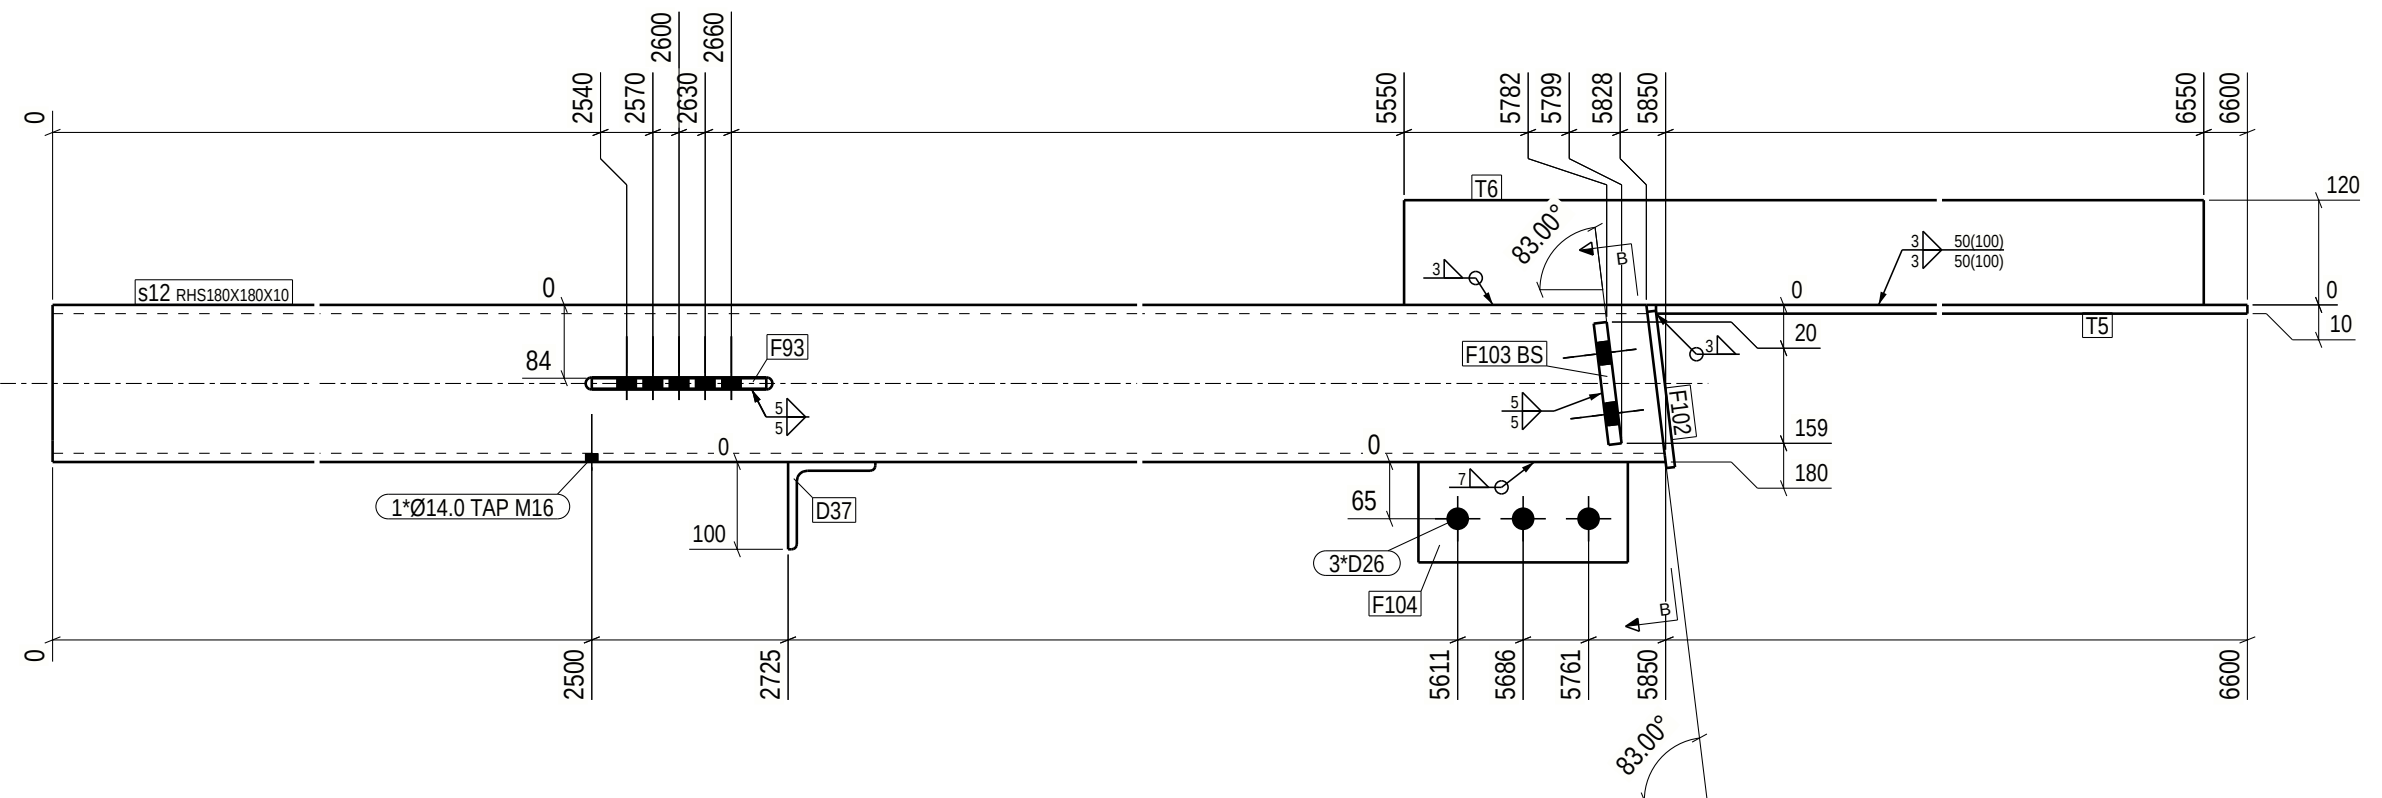

GENERAL NOTES: For your safety, check weight before handling:
2 Fls Light 5 15lb Normal 15 lbs Heavy

ALL WELDS ARE 4 UNLESS NOTED ON DRAWING

MATERIAL LIST FOR ASSEMBLY MK'D s.12					2 No. Required	
Mark	Profile	Material	No.	Length	Area	Weight
s12	RHS180X180X10	S355J2H	1	5850	4.0	294.0 !!
D37	L100*10	S355J2	1	120	0.0	1.8
F93	FL12*200	S355J2	1	520	0.2	9.3
F102	FL10*165	S355J2	1	180	0.1	2.3
F103	FL15*120	S355J2	2	140	0.0	2.0
F104	FL20*115	S355J2	1	240	0.1	4.3
T5	FL10*140	S355J2	1	761	0.2	8.4
T6	FL10*120	S355J2	1	1000	0.3	9.4
Total					5.0	333.5

Finish Class
Standard

Surface treatment info:

Thickness/start point--> length

No.	
-----	--

	weld a = 4 
---	--

PHASE	QUANTITY
1	2

* 030480 - 1 * **DS** Stahlkonstruktion * A s 1 2 *

PROJECT	Akkasæter Lager- og vedlikeholdshall			EXEC. CLASS	EXC 2
MEMBER	Sølje		QUANTITY:	2	PROJECT No 30480-1
REVISION		ISSUED: 03.11.2025	DRAFTER: ZLL BIM control SST	DRAWING No.	s.12