

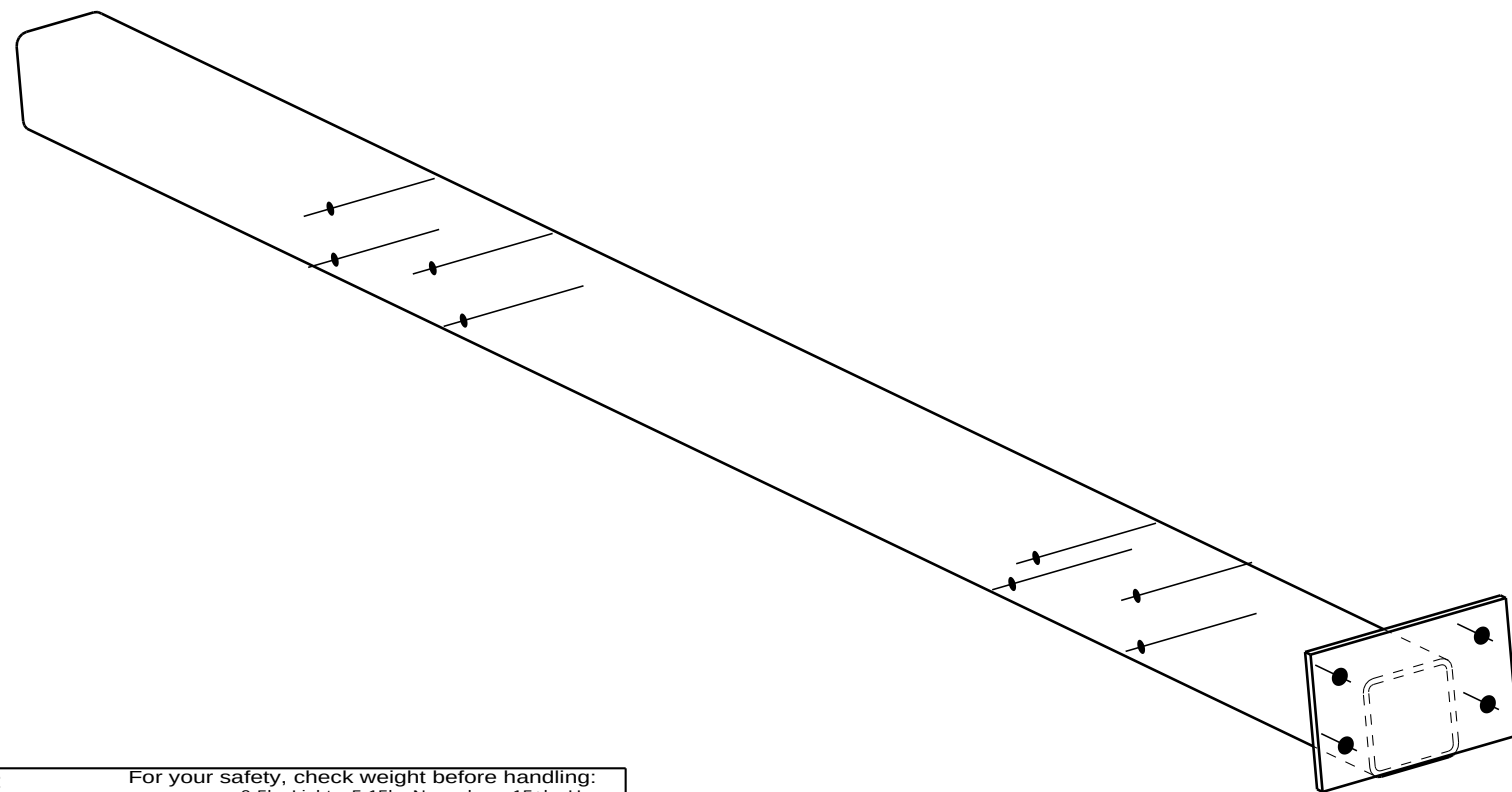
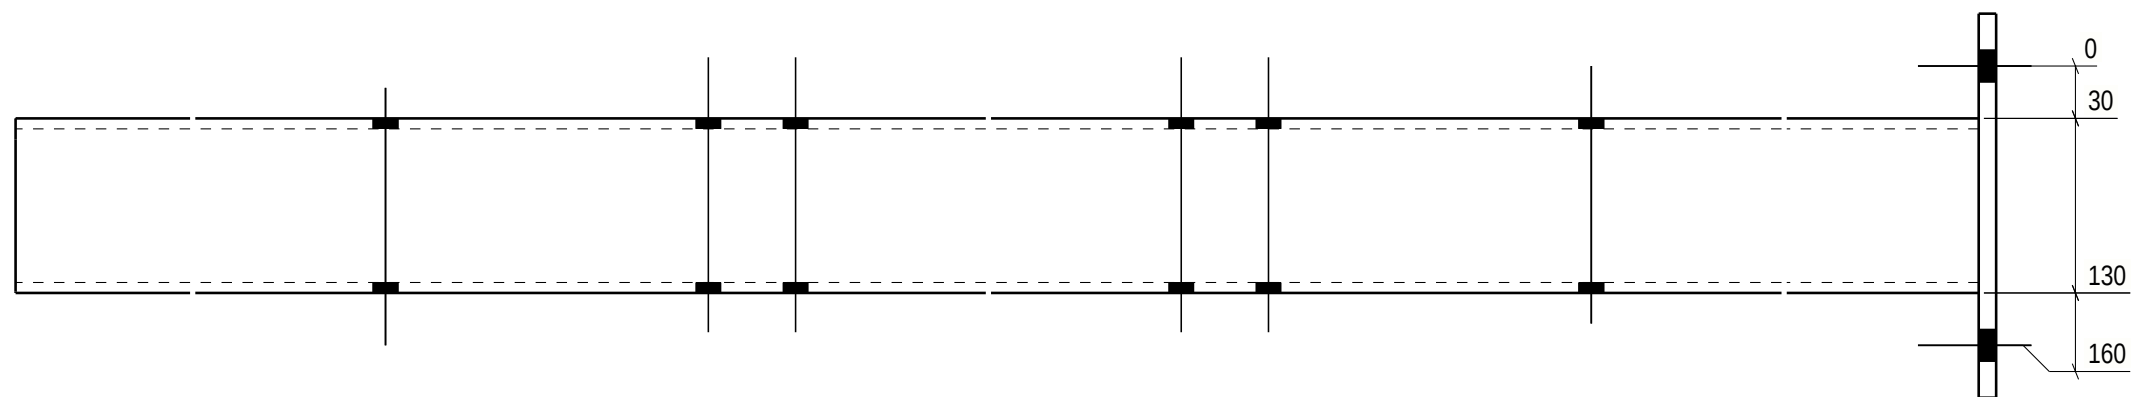


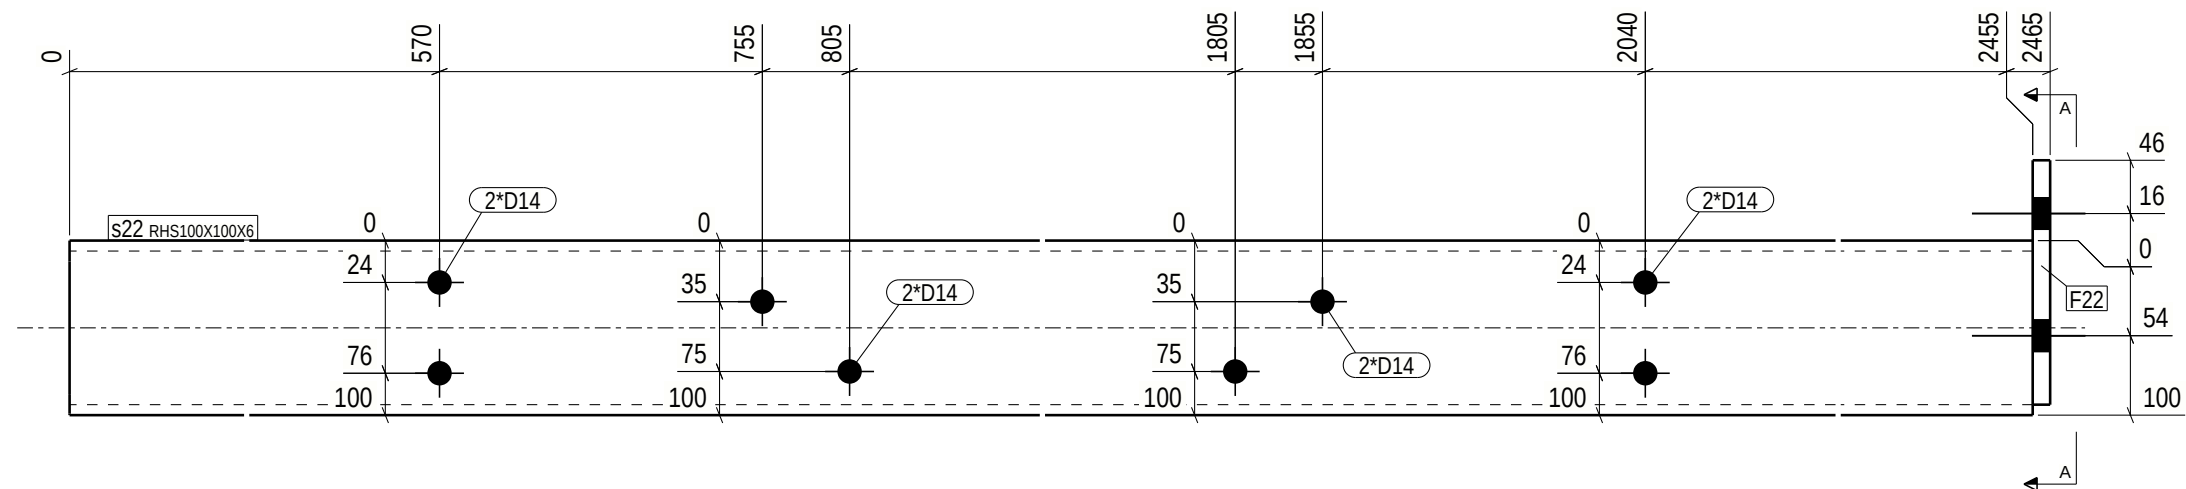

A - A  
1:2

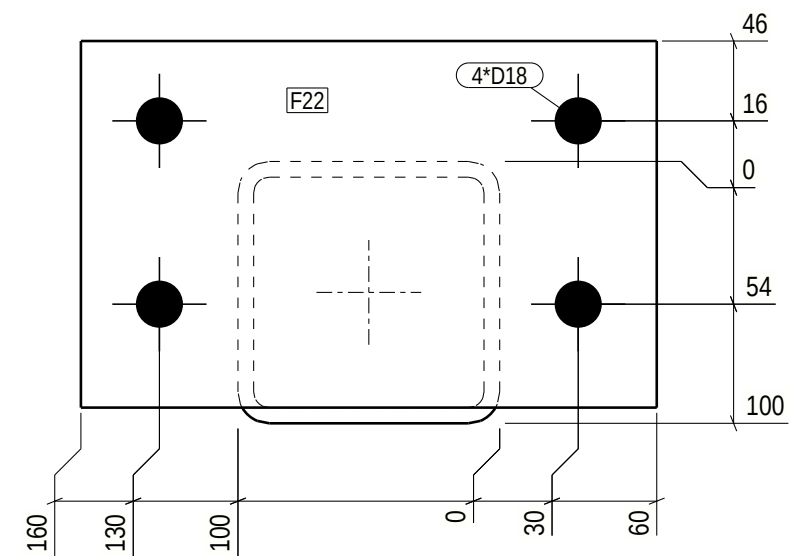

|                                                |              |          |     |        |      |         |
|------------------------------------------------|--------------|----------|-----|--------|------|---------|
| GENERAL NOTES:                                 |              |          |     |        |      |         |
| For your safety, check weight before handling: |              |          |     |        |      |         |
| 0-5kg Light 5-15kg Normal 15+kg Heavy          |              |          |     |        |      |         |
| ALL WELDS ARE 4 UNLESS NOTED ON DRAWING        |              |          |     |        |      |         |
| MATERIAL LIST FOR ASSEMBLY MK'D s.22           |              |          |     |        |      |         |
| Mark                                           | Profile      | Material | No. | Length | Area | Weight  |
| s22                                            | RHS100X100X6 | S355J2H  | 1   | 2455   | 0.9  | 41.5 !! |
| F22                                            | FL10*140     | S355J2   | 1   | 220    | 0.1  | 2.4     |
| Total                                          |              |          |     | 1.0    | 43.9 |         |

Finish Class  
Standard

Surface treatment info: Thickness/start point-> length No.

weld a = 4

|       |          |
|-------|----------|
| PHASE | QUANTITY |
| 1     | 2        |

|                                                     |                                      |              |       |
|-----------------------------------------------------|--------------------------------------|--------------|-------|
| * o 3 0 4 8 0 - 1 * DS Skalkonstruktion * A s 2 2 * |                                      |              |       |
| PROJECT                                             | Akkasæter Lager- og vedlikeholdshall | EXEC. CLASS  | EXC 2 |
| MEMBER                                              | Søyle                                | QUANTITY:    | 2     |
| REVISION                                            | ISSUED: 03.11.2025                   | DRAFTER:     | ZLL   |
|                                                     |                                      | BIM control: | SST   |
| PROJECT No.                                         |                                      | 30480-1      |       |
| DRAWING No.                                         |                                      | s.22         |       |