
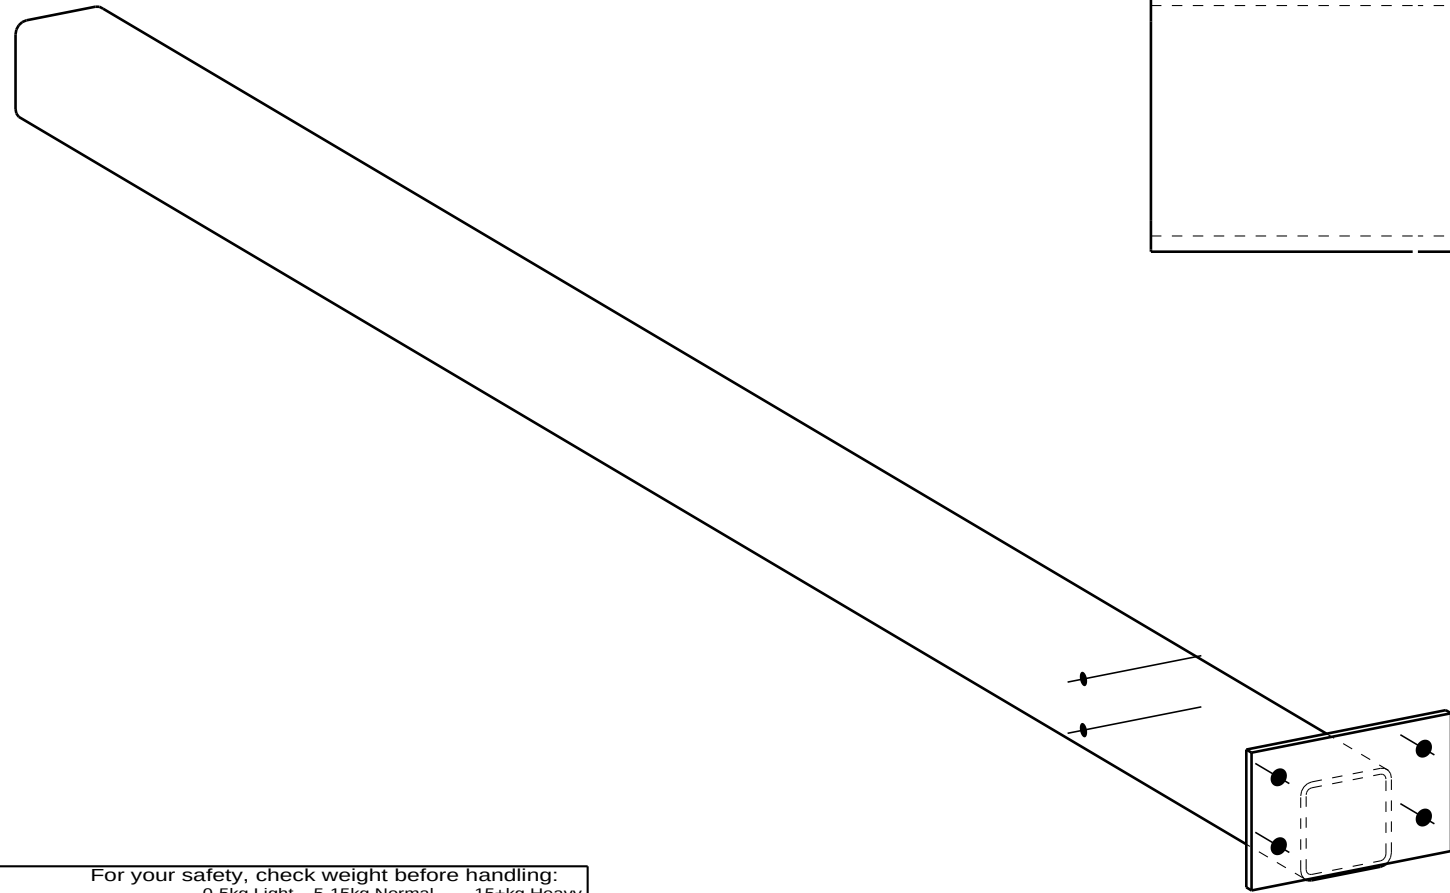
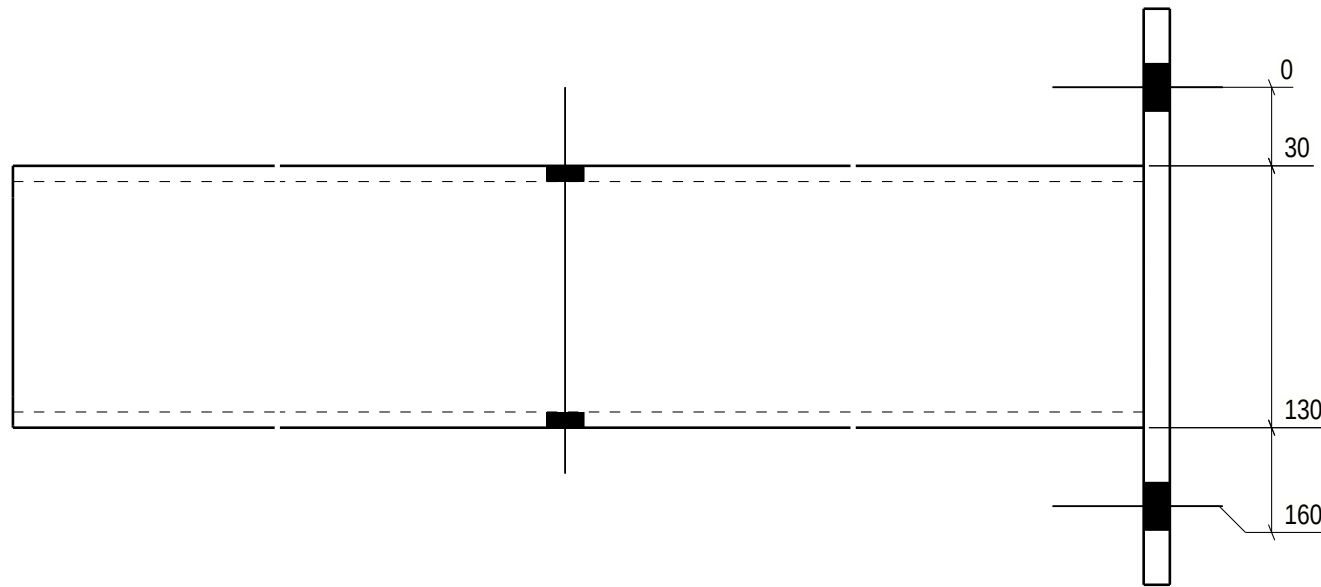
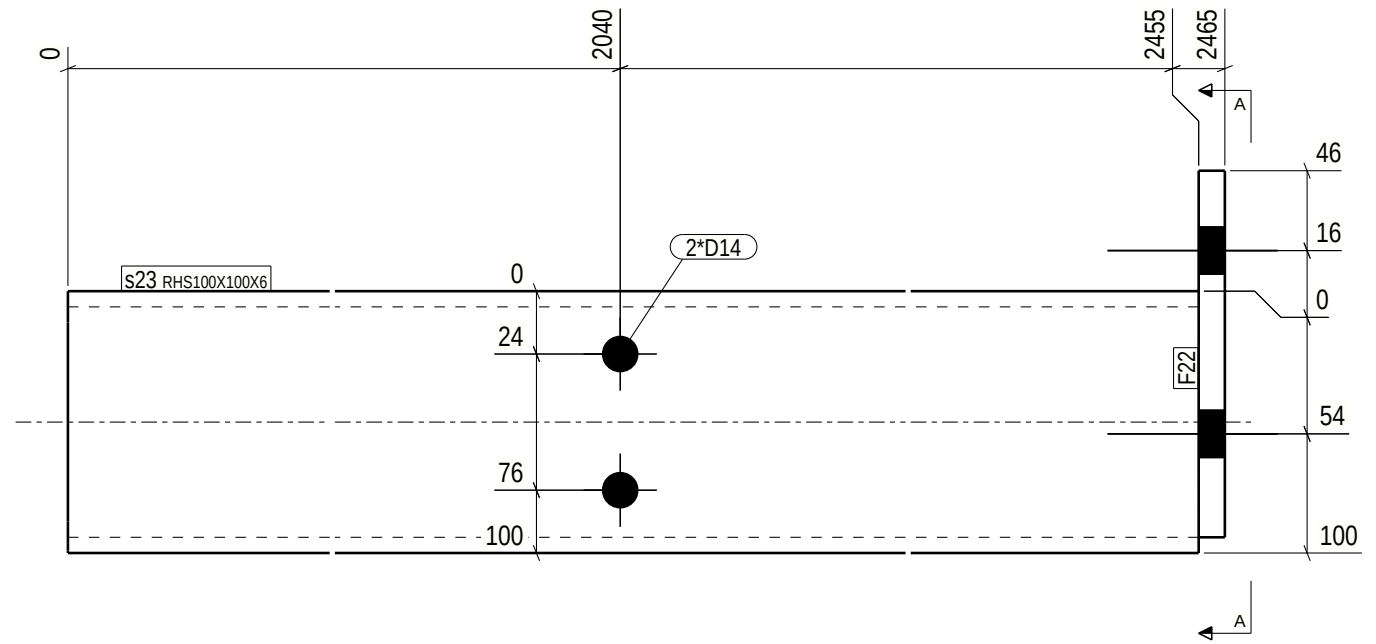


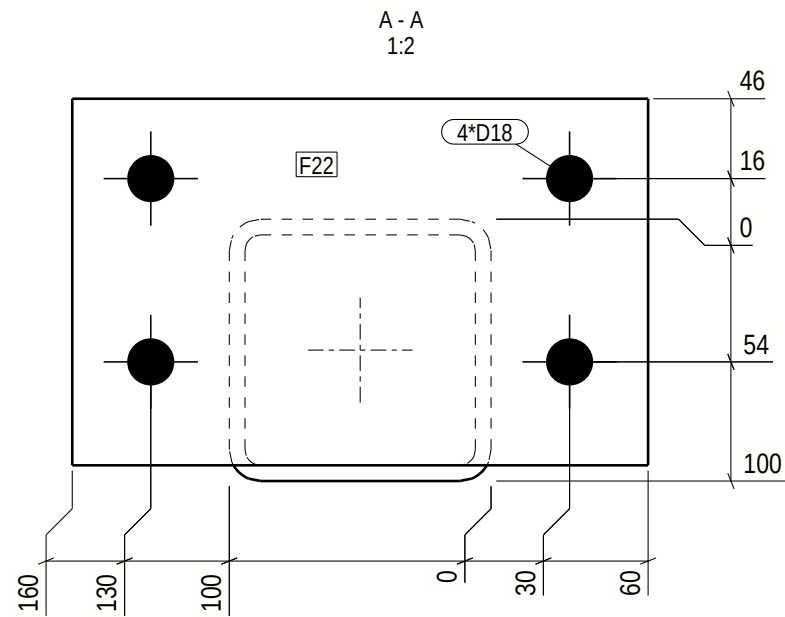

GENERAL NOTES: For your safety, check weight before handling:
0-5kg Light 5-15kg Normal 15+kg Heavy

ALL WELDS ARE 4 UNLESS NOTED ON DRAWING

MATERIAL LIST FOR ASSEMBLY MK'D **s.23**

Mark	Profile	Material	No.	Length	Area	Weight
s23	RHS100X100X6	S355J2H	1	2455	0.9	41.5 !!
F22	FL10*140	S355J2	1	220	0.1	2.4
Total				1.0	43.9	

Finish Class
Standard

Surface treatment info:	Thickness/start point--> length	No.
-------------------------	---------------------------------	-----

weld a = 4

PHASE	QUANTITY
1	2

* o 3 0 4 8 0 - 1 *  DS <i>Stalkonstruktion</i> * A s 2 3 *					
PROJECT	Akkasæter Lager- og vedlikeholdshall			EXEC. CLASS	EXC 2
MEMBER	Søyle	QUANTITY:	2	PROJECT No	30480-1
REVISION		ISSUED:	03.11.2025	DRAFTER: ZLL BIM control: SST	DRAWING No. s.23