
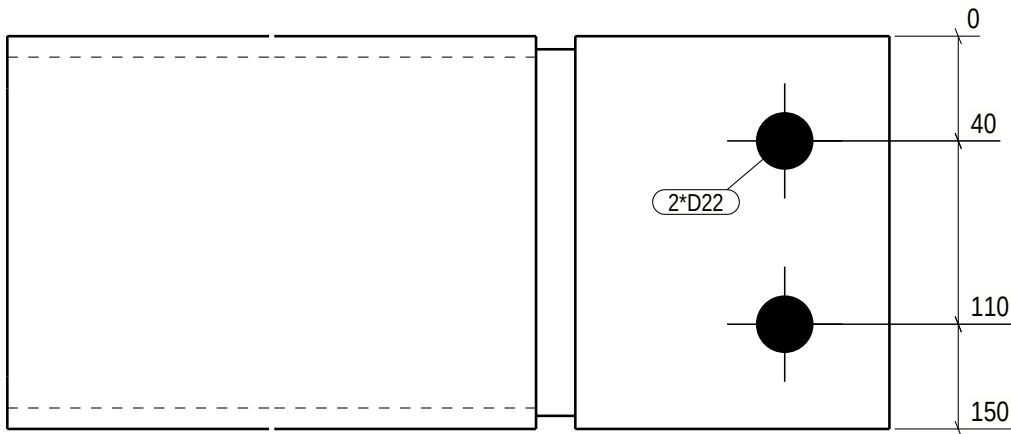
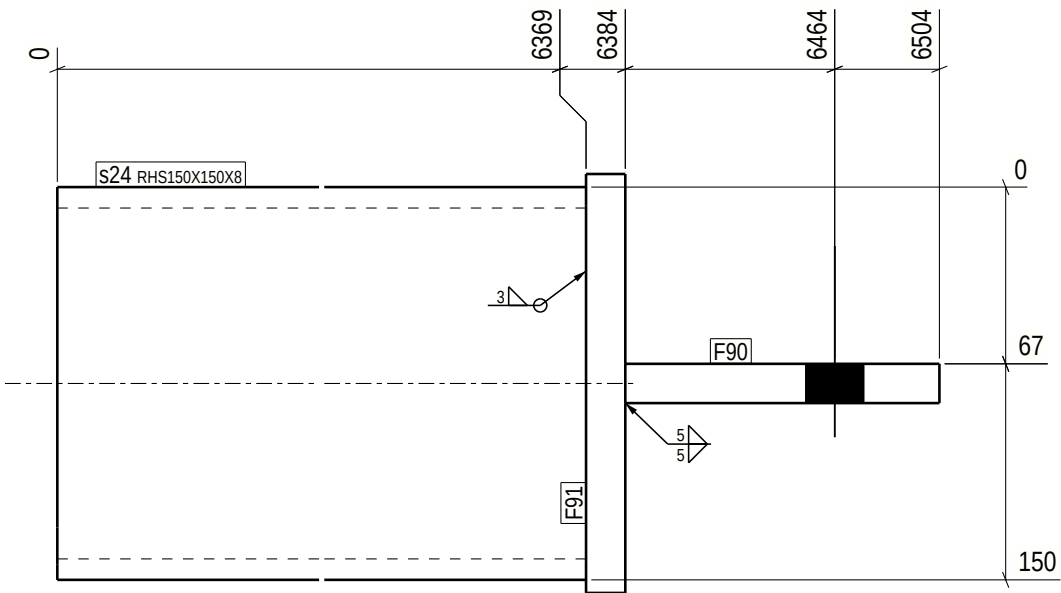


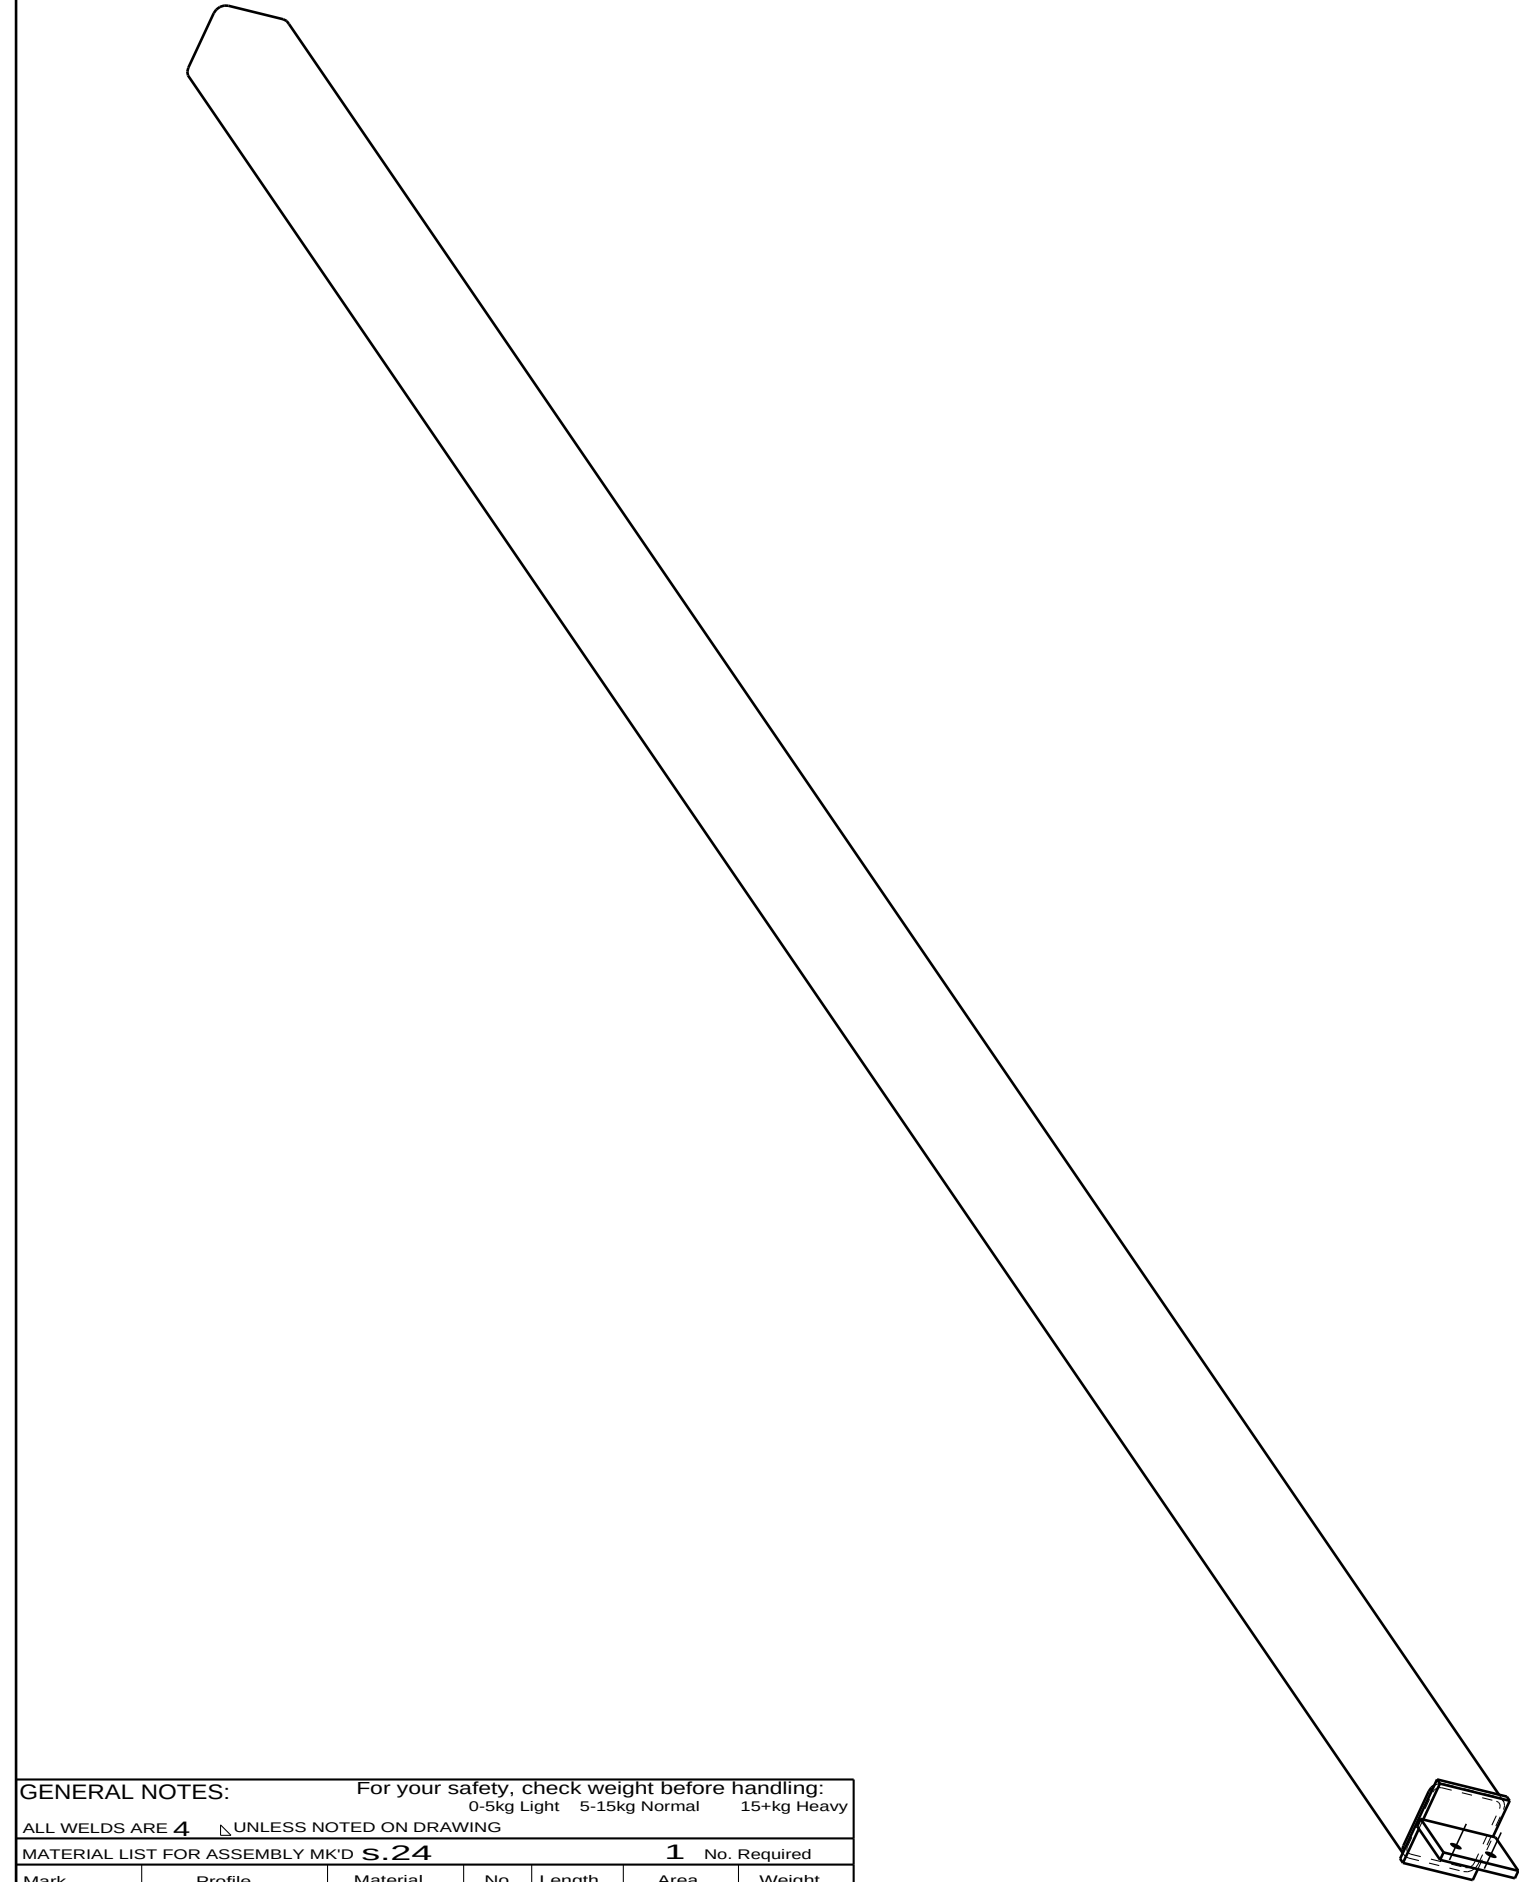

GENERAL NOTES: For your safety, check weight before handling:						
ALL WELDS ARE 4 UNLESS NOTED ON DRAWING						
MATERIAL LIST FOR ASSEMBLY MK'D s.24						
Mark	Profile	Material	No.	Length	Area	Weight
S24	RHS150X150X8	S355J2H	1	6369	3.6	215.2 !!
F90	FL15*120	S355J2	1	150	0.0	2.1
F91	FL15*140	S355J2	1	160	0.1	2.6
Total					3.7	219.9

Finish Class
Standard

Surface treatment info:	Thickness/start point-> length	No.
-------------------------	--------------------------------	-----

weld a = 4

PHASE	QUANTITY
1	1

* o 3 0 4 8 0 - 1 * DS Sankonstruktør * A s 2 4 *					
PROJECT	Akkasæter Lager- og vedlikeholdshall			EXEC. CLASS	EXC 2
MEMBER	Søyle		QUANTITY:	1	PROJECT No 30480-1
REVISION		ISSUED: 03.11.2025	DRAFTER: ZLL	BIM control: SST	DRAWING No. s.24