
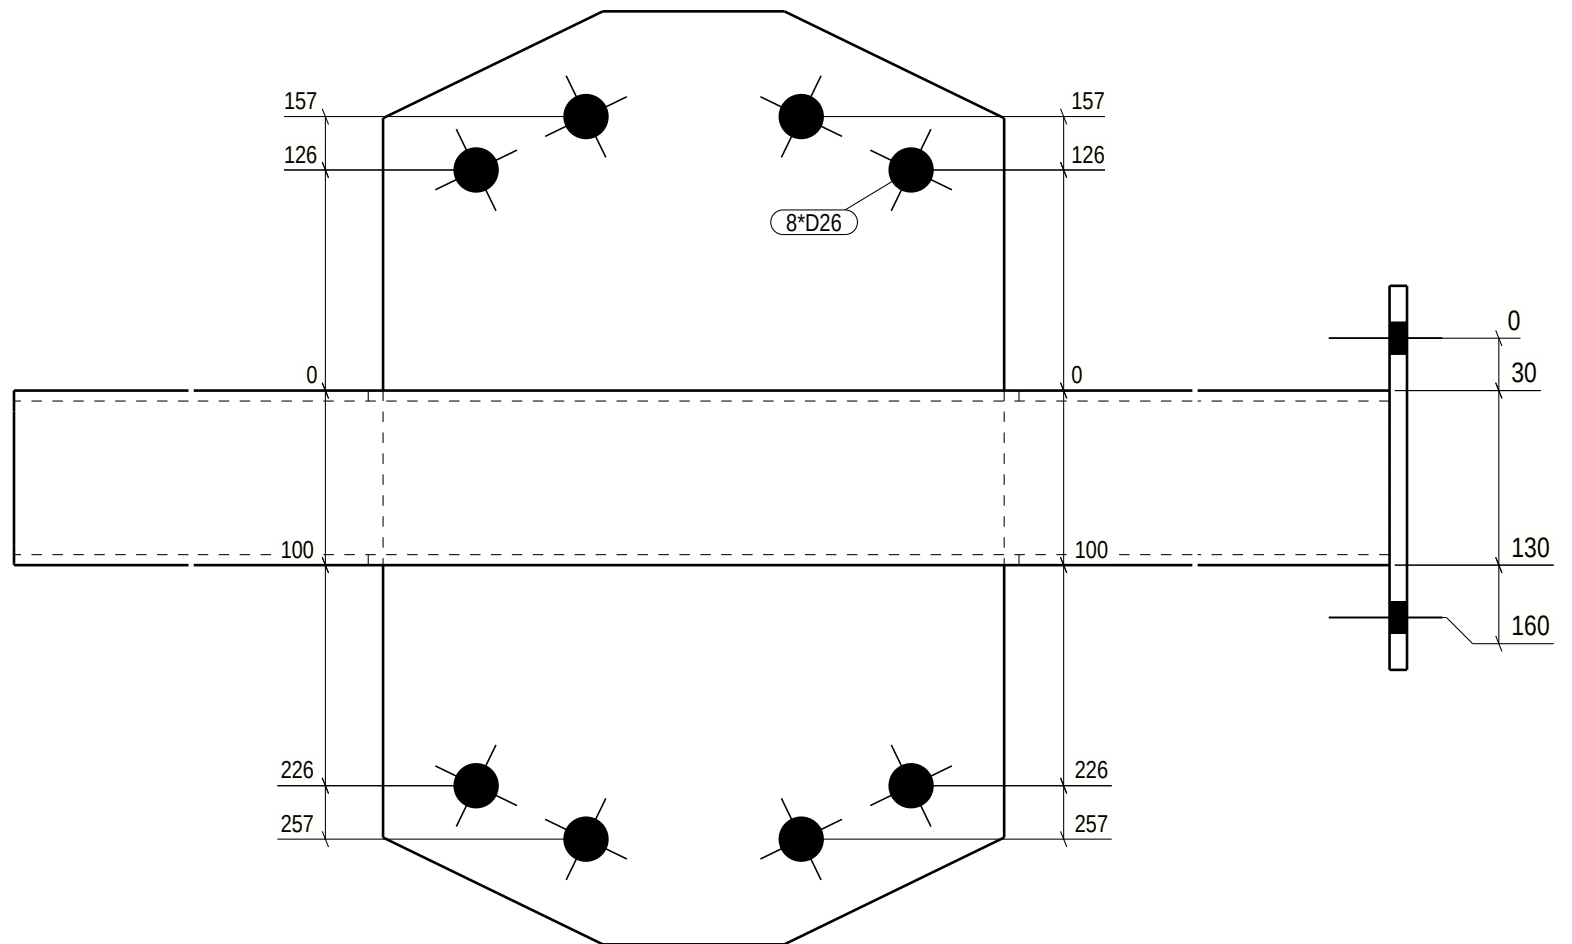
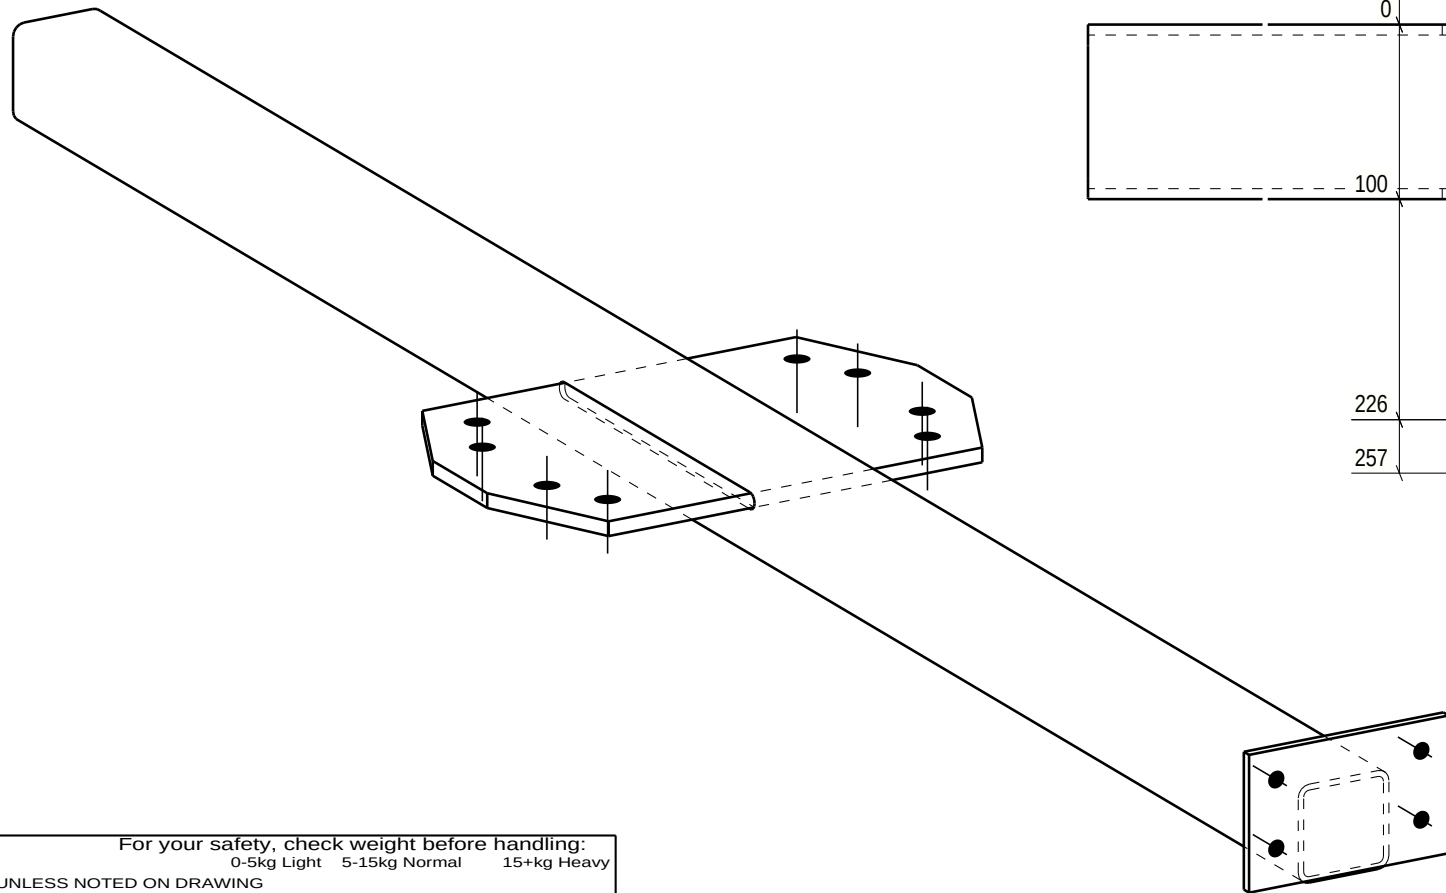
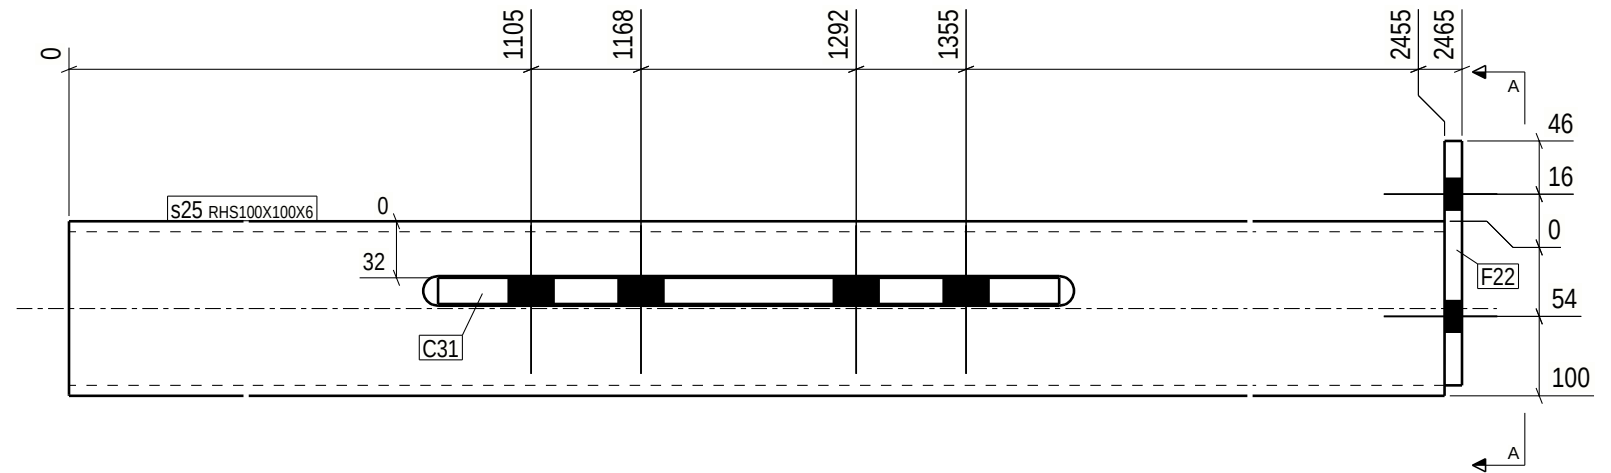


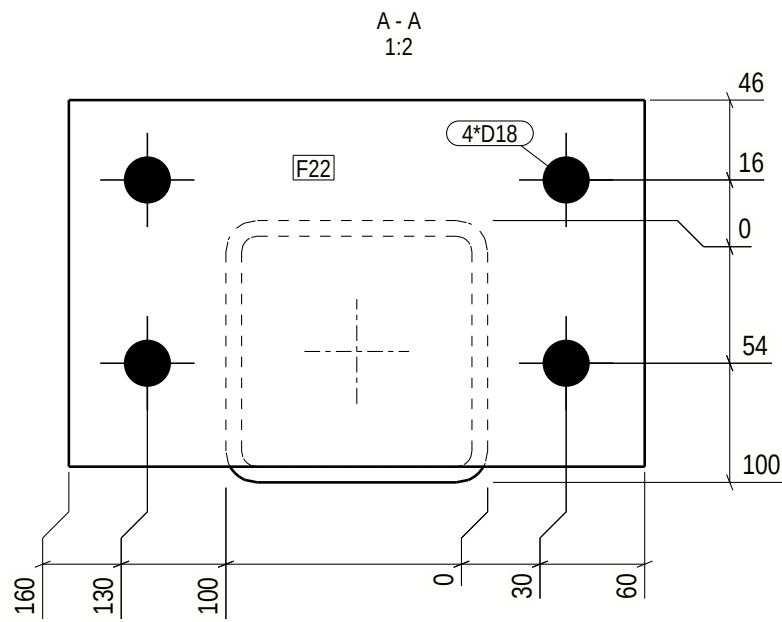

GENERAL NOTES: For your safety, check weight before handling:
0-5kg Light 5-15kg Normal 15+kg Heavy

ALL WELDS ARE 4 UNLESS NOTED ON DRAWING

MATERIAL LIST FOR ASSEMBLY MK'D **s.25**

Mark	Profile	Material	No.	Length	Area	Weight
S25	RHS100X100X6	S355J2H	1	2455	0.9	40.9 !!
C31	PL15*356	S355J2	1	534	0.4	20.6 !!
F22	FL10*140	S355J2	1	220	0.1	2.4
Total					1.4	63.9

Finish Class
Standard

Surface treatment info:	Thickness/start point-> length	No.
-------------------------	--------------------------------	-----

weld a = 4

PHASE	QUANTITY
1	1

* o 3 0 4 8 0 - 1 * DS <i>Stalkonstruktion</i> * A s 2 5 *			
PROJECT	Akkasæter Lager- og vedlikeholdshall	EXEC. CLASS	EXC 2
MEMBER	Søyle	QUANTITY:	1
REVISION	ISSUED: 03.11.2025	DRAFTER: ZLL	PROJECT No 30480-1
	BIM control: SST		DRAWING No. s.25