
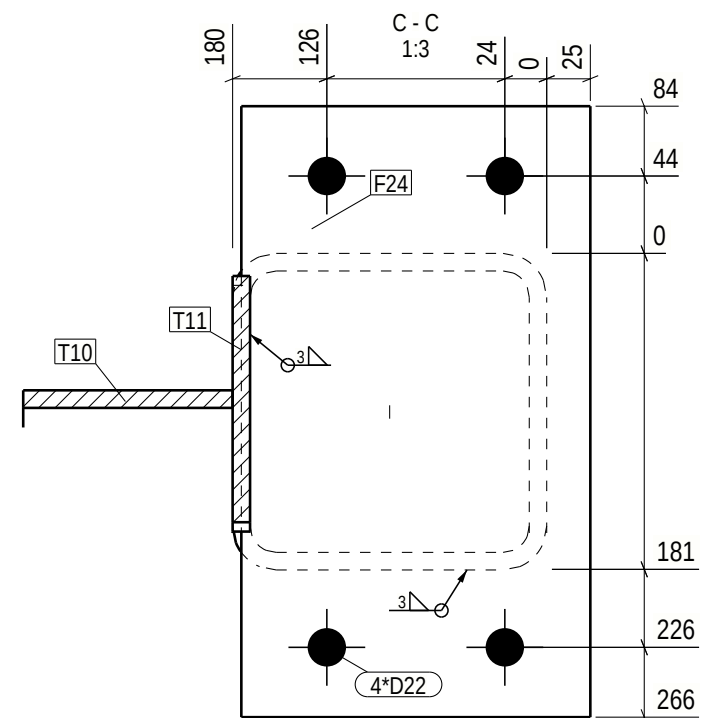
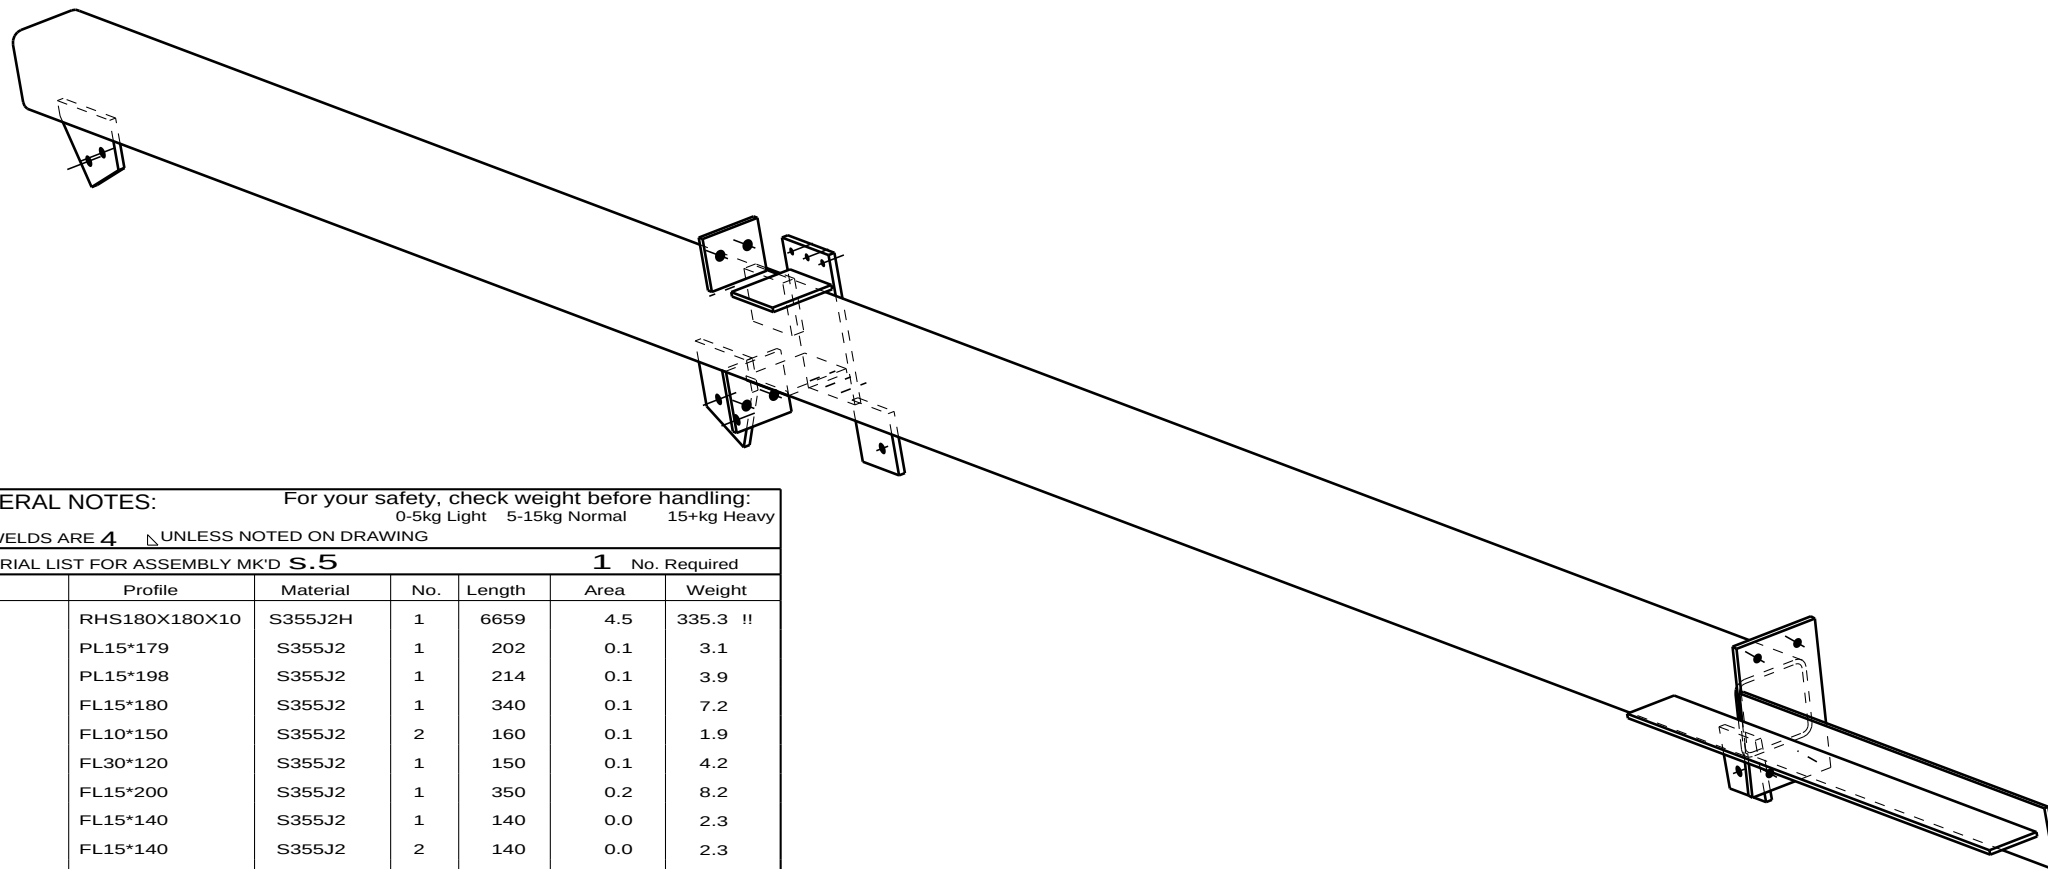


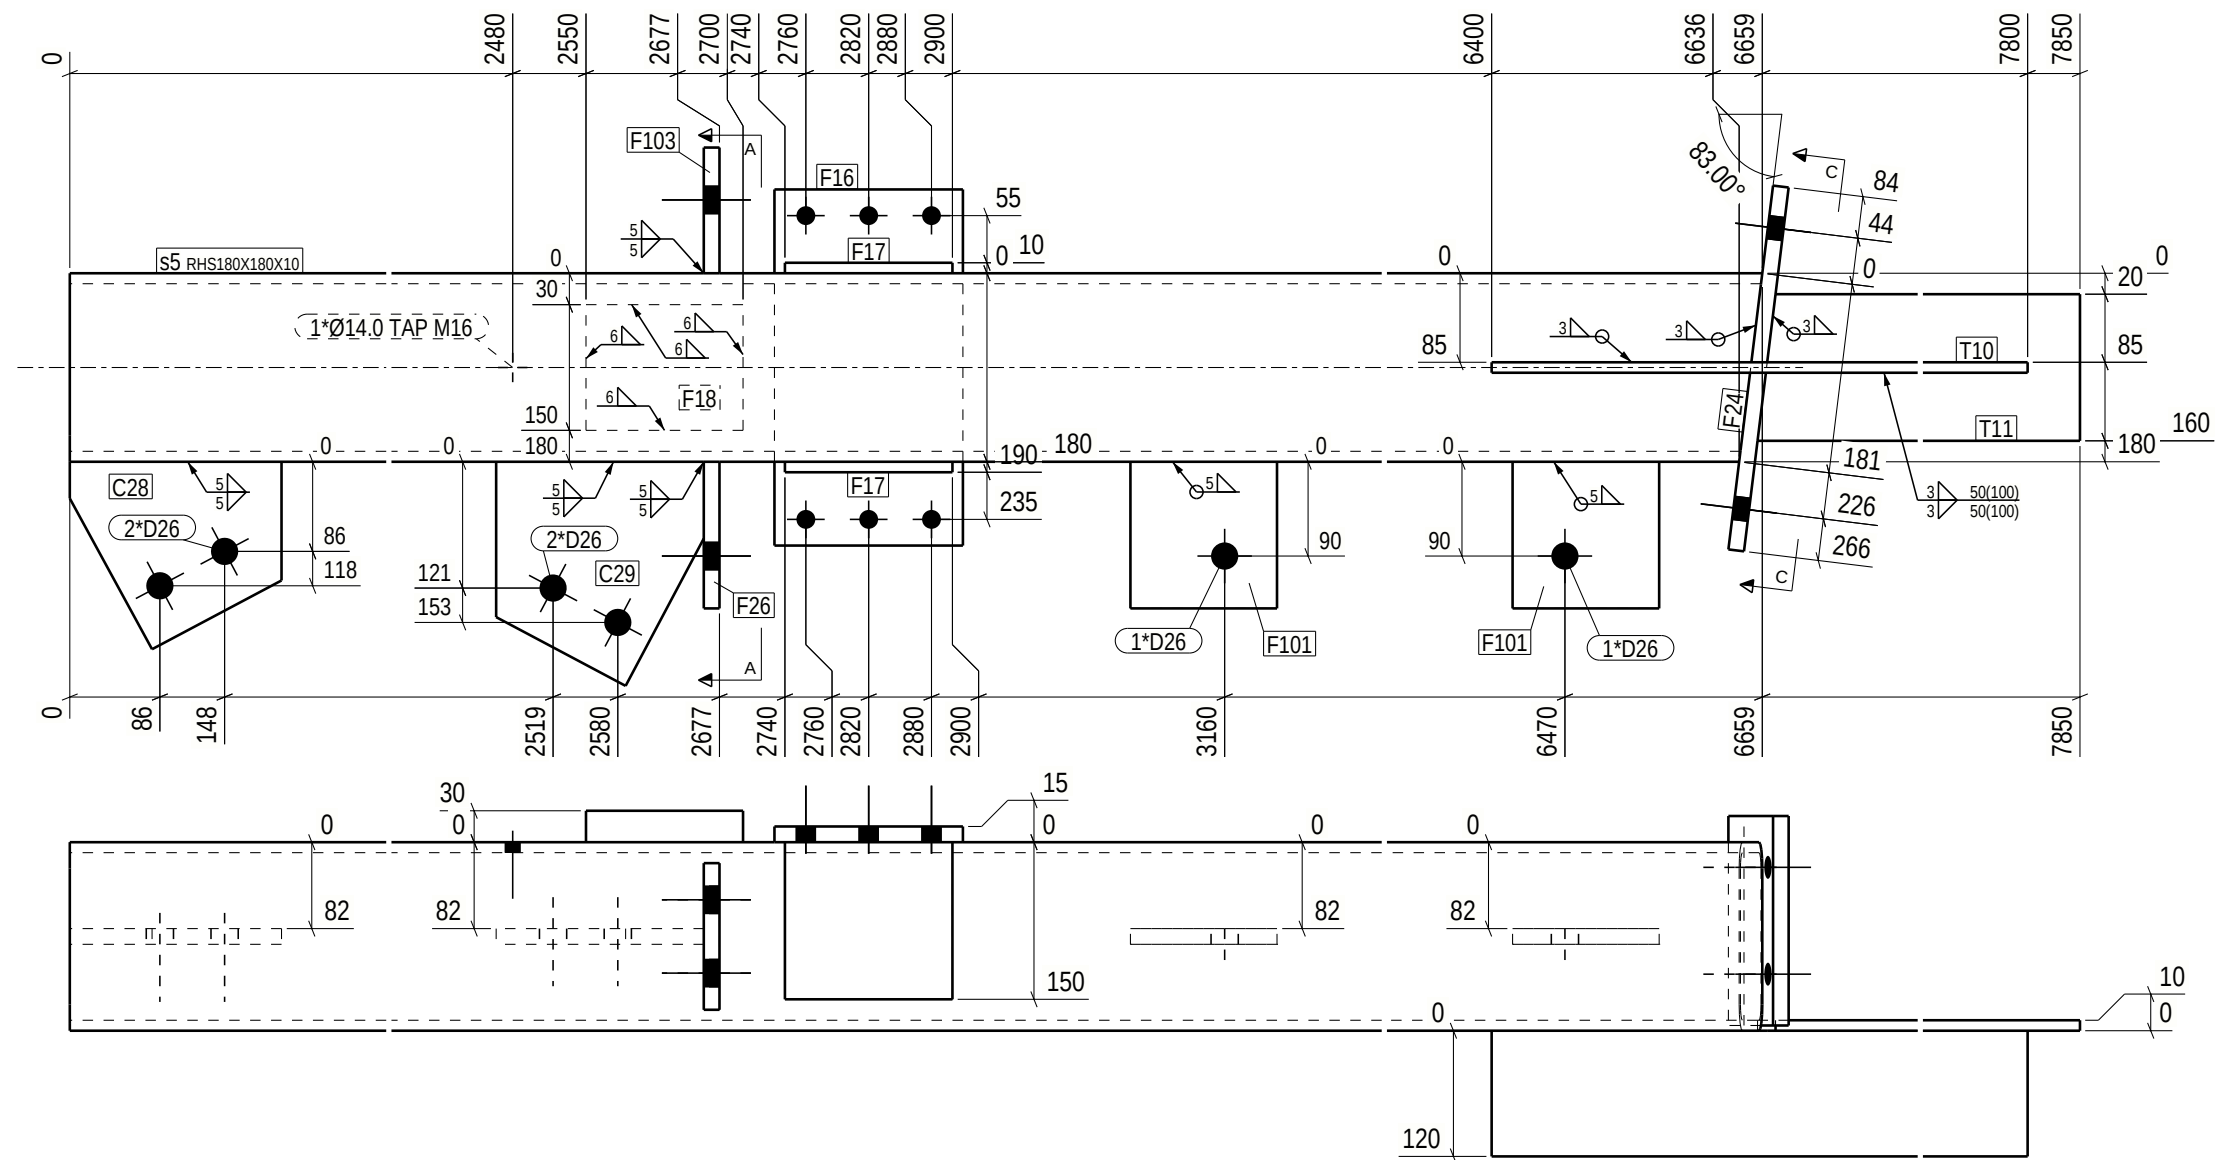

MATERIAL LIST FOR ASSEMBLY MK'D S.5					1 No. Required	
Mark	Profile	Material	No.	Length	Area	Weight
s5	RHS180X180X10	S355J2H	1	6659	4.5	335.3 !!
C28	PL15*179	S355J2	1	202	0.1	3.1
C29	PL15*198	S355J2	1	214	0.1	3.9
F16	FL15*180	S355J2	1	340	0.1	7.2
F17	FL10*150	S355J2	2	160	0.1	1.9
F18	FL30*120	S355J2	1	150	0.1	4.2
F24	FL15*200	S355J2	1	350	0.2	8.2
F26	FL15*140	S355J2	1	140	0.0	2.3
F101	FL15*140	S355J2	2	140	0.0	2.3
F103	FL15*120	S355J2	1	140	0.0	2.0
T10	FL10*120	S355J2	1	1400	0.4	13.2
T11	FL10*140	S355J2	1	1196	0.4	13.0
Total					6.1	400.9

Finish Class
Standard

Surface treatment info:	Thickness/start point--> length	No.
-------------------------	---------------------------------	-----

	weld a = 4 
---	--

PHASE	QUANTITY
1	1

* 030480 - 1 * **DS** Stalkonstruktion * A S 5 *

PROJECT	Akkasæter Lager- og vedlikeholdshall			EXEC. CLASS	EXC 2
MEMBER	Sølle		QUANTITY:	1	PROJECT No 30480-1
REVISION		ISSUED: 03.11.2025	DRAFTER: BIM control:	ZLL SST	DRAWING No. S.5