


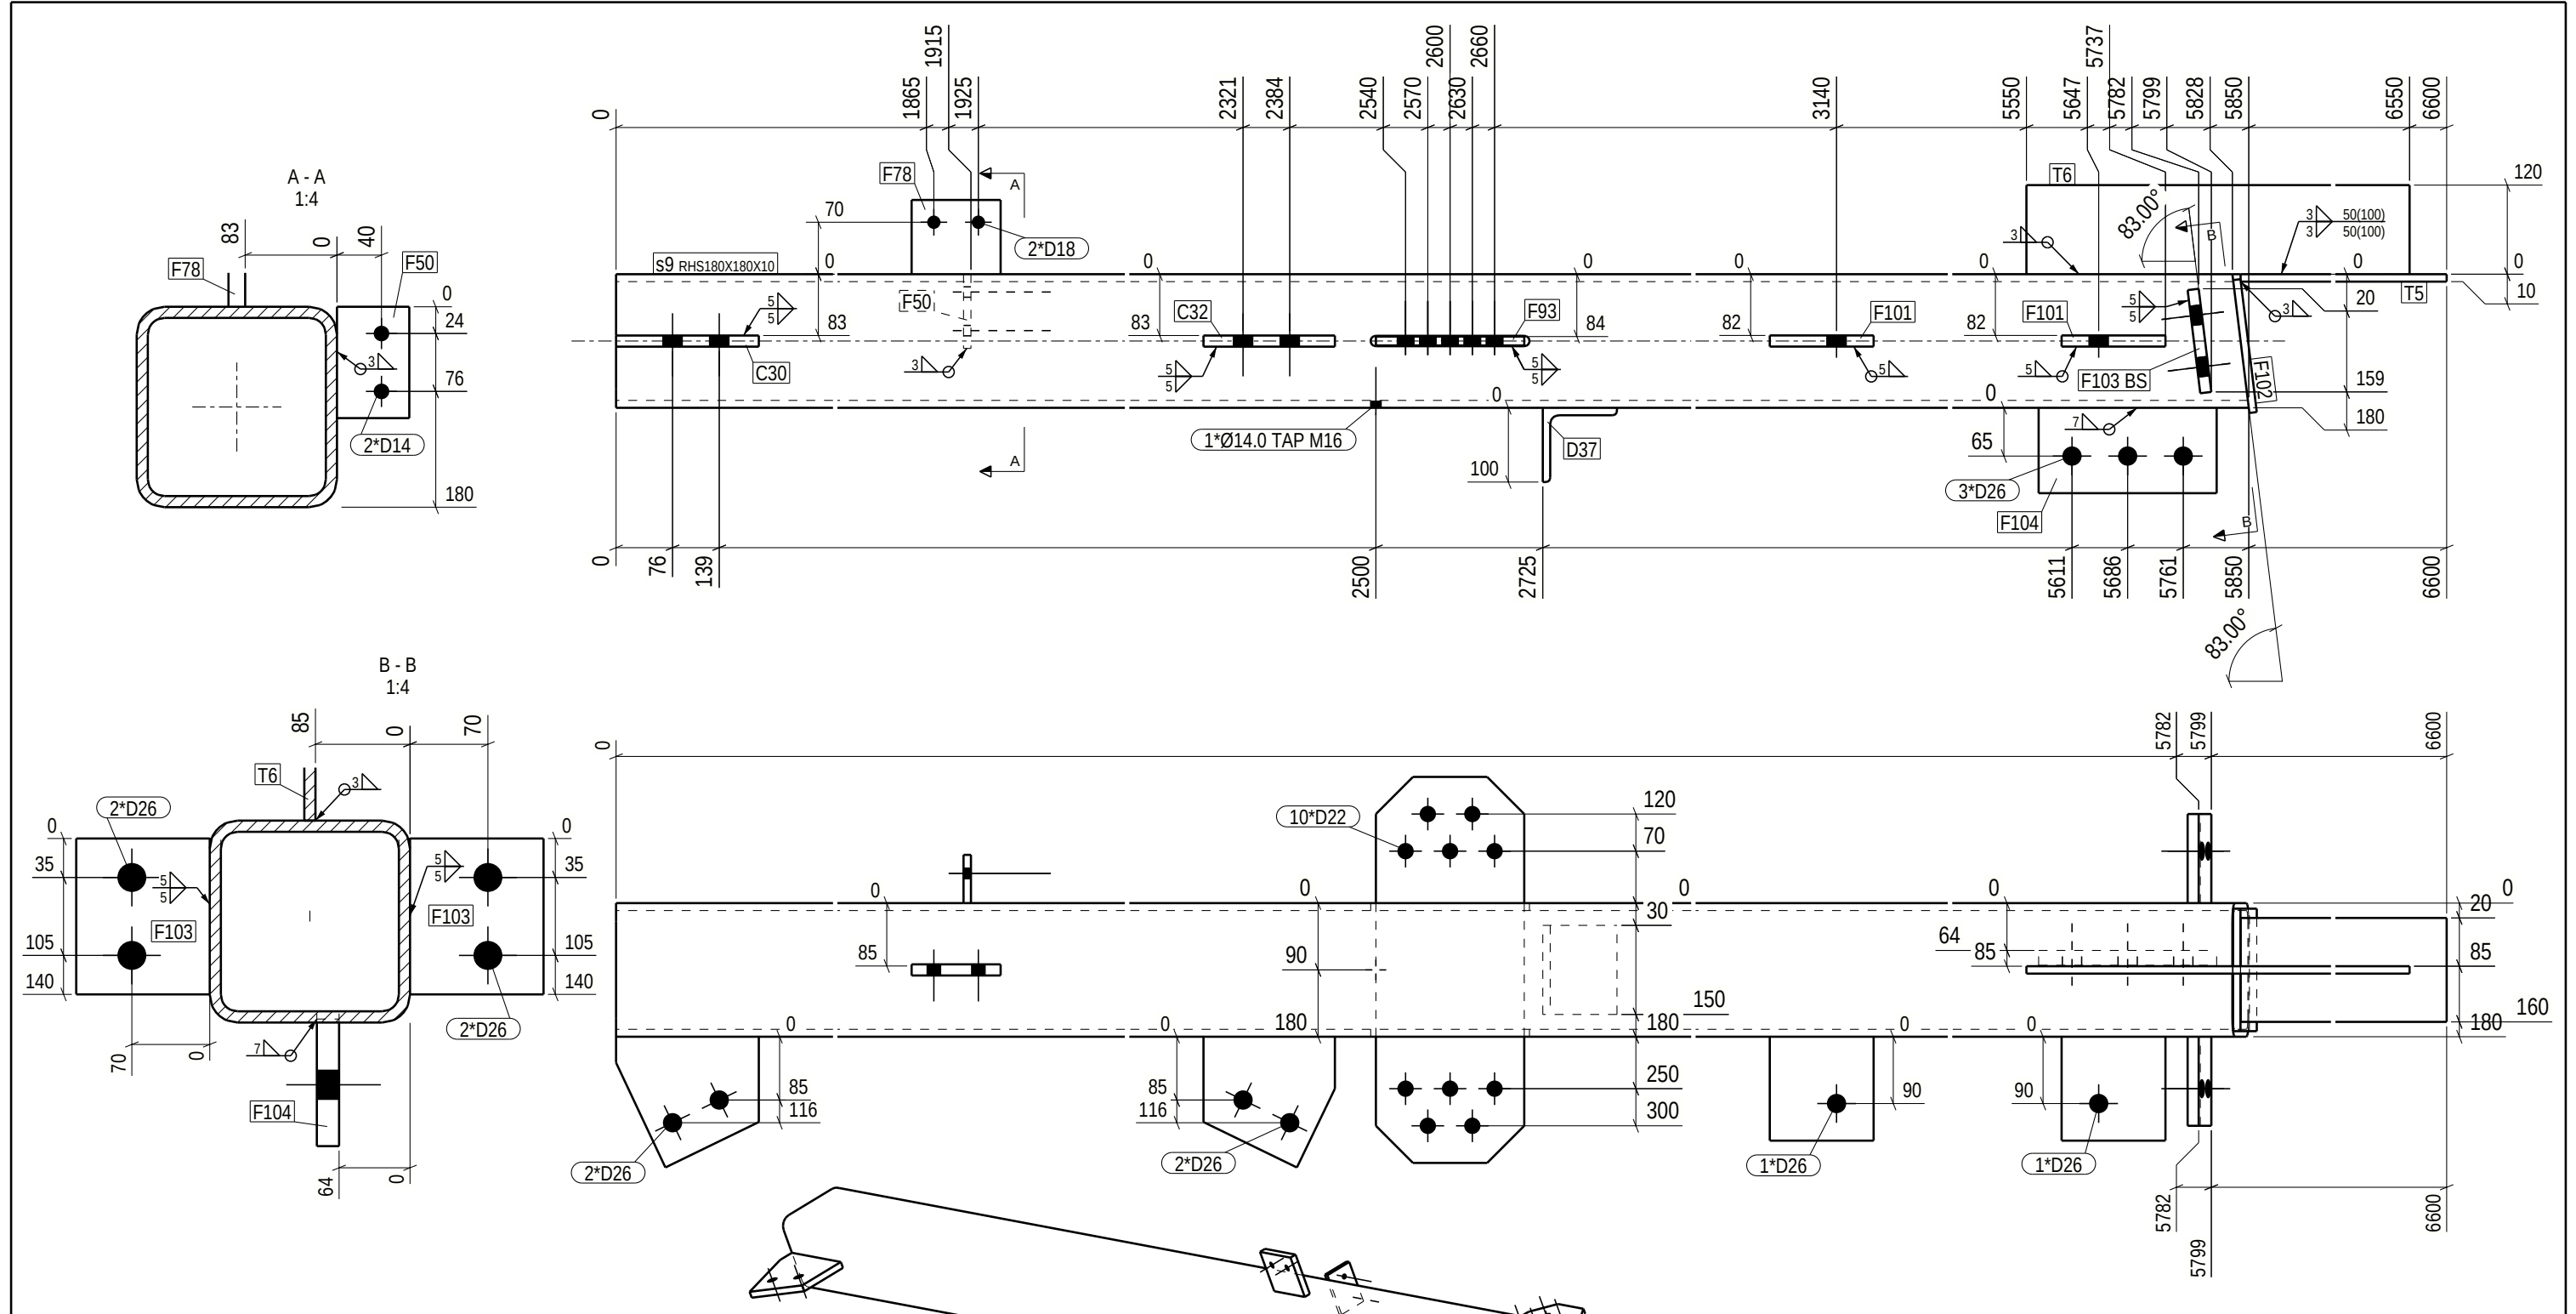

GENERAL NOTES: For your safety, check weight before handling:
0-5kg Light 5-15kg Normal 15+kg Heavy

ALL WELDS ARE 4 UNLESS NOTED ON DRAWING

MATERIAL LIST FOR ASSEMBLY MK'D S.9 1 No. Required

Mark	Profile	Material	No.	Length	Area	Weight
s9	RHS180X180X10	S355J2H	1	5850	4.0	294.0 !!
C30	PL15*176	S355J2	1	192	0.1	3.0
C32	PL15*176	S355J2	1	177	0.1	2.9
D37	L100*10	S355J2	1	120	0.0	1.8
F50	FL10*65	S355J2	1	100	0.0	0.5
F78	FL15*100	S355J2	1	120	0.0	1.4
F93	FL12*200	S355J2	1	520	0.2	9.3
F101	FL15*140	S355J2	2	140	0.0	2.3
F102	FL10*165	S355J2	1	180	0.1	2.3
F103	FL15*120	S355J2	2	140	0.0	2.0
F104	FL20*115	S355J2	1	240	0.1	4.3
T5	FL10*140	S355J2	1	761	0.2	8.4
T6	FL10*120	S355J2	1	1000	0.3	9.4
Total					5.2	346.0

Finish Class
Standard

Surface treatment info: Thickness/start point-> length No.

weld a = 4

PHASE	QUANTITY
1	1

* o 3 0 4 8 0 - 1 * DS Stalkonstruktion * A s 9 *			
PROJECT	Akkasæter Lager- og vedlikeholdshall	EXEC. CLASS	EXC 2
MEMBER	Søyle	QUANTITY:	1 PROJECT No 30480-1
REVISION	ISSUED: 03.11.2025	DRAFTER: ZLL SST	DRAWING No. s.9