


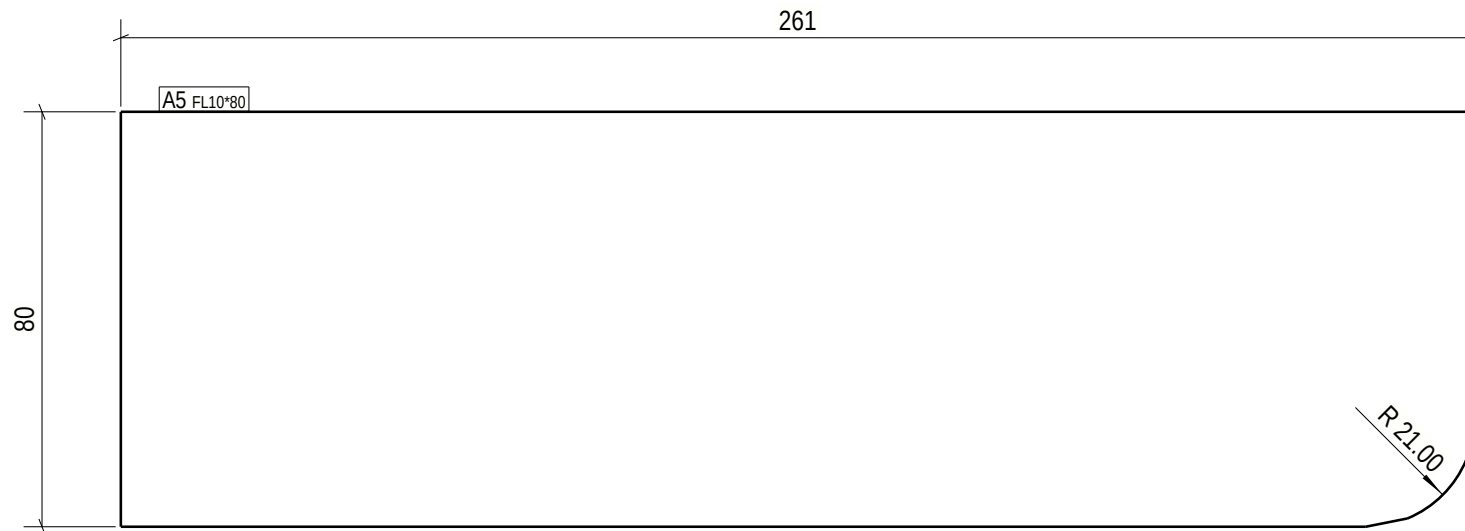

GENERAL NOTES:						
For your safety, check weight before handling:						
0-5kg Light 5-15kg Normal 15+kg Heavy						
MATERIAL LIST FOR PART - A5				2 PARTS REQUIRED		
POS. No.	PROFILE	No.	GRADE	L (mm)	AREA (m ²)	WEIGHT (kg)
A5	FL10*80	1	S355J2	261	0.0	1.6
TOTAL WEIGHT FOR				2	PARTS	3.3

Part list		Qty.
DR		2

Execution class: EXC 2			* o 3 0 4 8 0 - 1 *  DS <i>Skalkonstruktion</i> * W A 5 *		
No utilization on drawings = over 50%					
V-SEAM Utilization under 50% EXC 2=> Acc. to process control EXC 3=> 20% UT Utilization over 50% EXC 2=> 10% UT EXC 3=> 20% UT			PROJECT	Akkasæter Lager- og vedlikeholdshall	PHASE 1 / Phase 1
			MEMBER	Afstivning	QUANTITY: 2 PROJECT No 30480-1
			REVISION	ISSUED: 04.11.2025	DRAFTER: ZLL BIM control: SST DRAWING No. A.5