


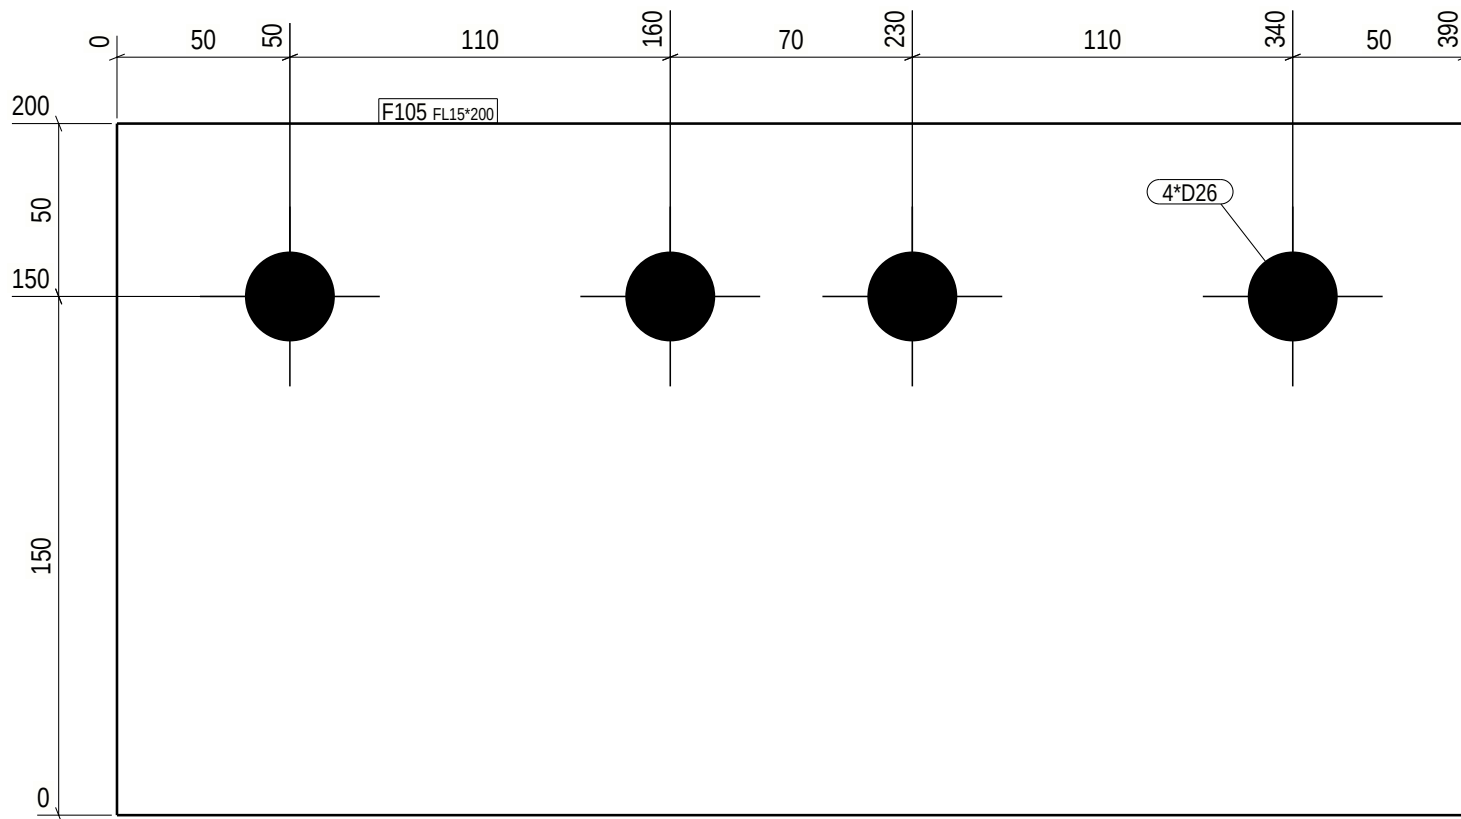

|   |          |     |        |        |                        |             |
|---|----------|-----|--------|--------|------------------------|-------------|
| GENERAL NOTES: For your safety, check weight before handling:<br>0-5kg Light 5-15kg Normal 15+kg Heavy |          |     |        |        |                        |             |
| MATERIAL LIST FOR PART - F105 8 PARTS REQUIRED                                                         |          |     |        |        |                        |             |
| POS. No.                                                                                               | PROFILE  | No. | GRADE  | L (mm) | AREA (m <sup>2</sup> ) | WEIGHT (kg) |
| F105                                                                                                   | FL15*200 | 1   | S355J2 | 390    | 0.2                    | 9.2         |
| TOTAL WEIGHT FOR                                                                                       |          |     |        | 8      | PARTS                  | 73.5        |

|           |      |
|-----------|------|
| Part list | Qty. |
| DR        | 8    |

|   |  |   |                                      |  |                                                    |
|---|--|---|--------------------------------------|--|----------------------------------------------------|
| Execution class: EXC 2   |  | * o 3 0 4 8 0 - 1 *  DS <i>Skalkonstruktion</i> * WF 1 0 5 * |                                      |  |                                                    |
| No utilization on drawings = over 50%   |  |   |                                      |  |                                                    |
| V-SEAM<br>Utilization under 50%<br>EXC 2=> Acc. to process control<br>EXC 3=> 20% UT<br>Utilization over 50%<br>EXC 2=> 10% UT<br>EXC 3=> 20% UT |  | PROJECT   | Akkasæter Lager- og vedlikeholdshall |  | PHASE 1 / Phase 1                                  |
|   |  | MEMBER   | Fladstål                             |  | QUANTITY: 8 PROJECT No 30480-1                     |
|   |  | REVISION   | ISSUED: 03.11.2025                   |  | DRAFTER: ZLL<br>BIM control: SST DRAWING No. F.105 |