


Tekla Structures

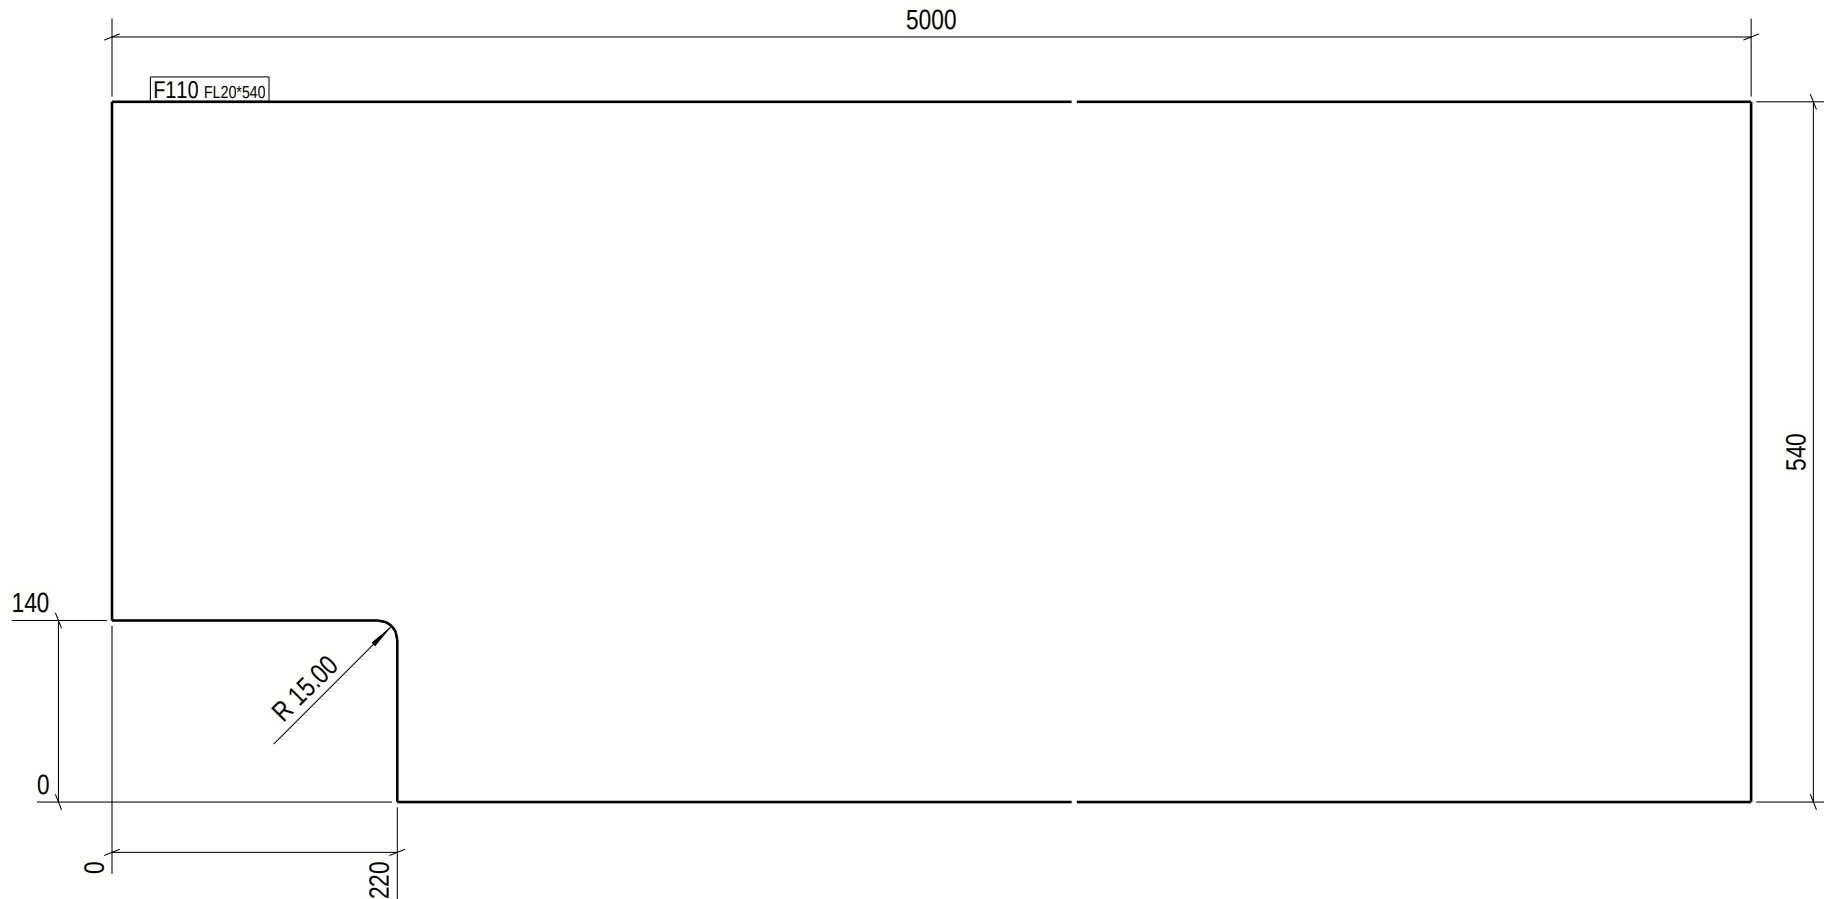

GENERAL NOTES:

For your safety, check weight before handling:
0-5kg Light 5-15kg Normal 15+kg Heavy

MATERIAL LIST FOR PART - F110 2 PARTS REQUIRED

POS. No.	PROFILE	No.	GRADE	L (mm)	AREA (m ²)	WEIGHT (kg)
F110	FL20*540	1	S355J2	5000	5.6	419.1 !!

TOTAL WEIGHT FOR 2 PARTS 838.1

Part list	Qty.
OB	2

Execution class: EXC 2

No utilization on drawings = over 50%

V-SEAM
Utilization under 50%
EXC 2=> Acc. to process control
EXC 3=> 20% UT
Utilization over 50%
EXC 2=> 10% UT
EXC 3=> 20% UT

* o 3 0 4 8 0 - 1 *  **DS** *Skalkonstruktion* * WF 1 1 0 *

PROJECT	Akkasæter Lager- og vedlikeholdshall		PHASE	1 / Phase 1	
MEMBER	HSQ		QUANTITY:	2	PROJECT No 30480-1
REVISION		ISSUED: 03.11.2025	DRAFTER: BIM control:	ZLL SST	DRAWING No. F.110