


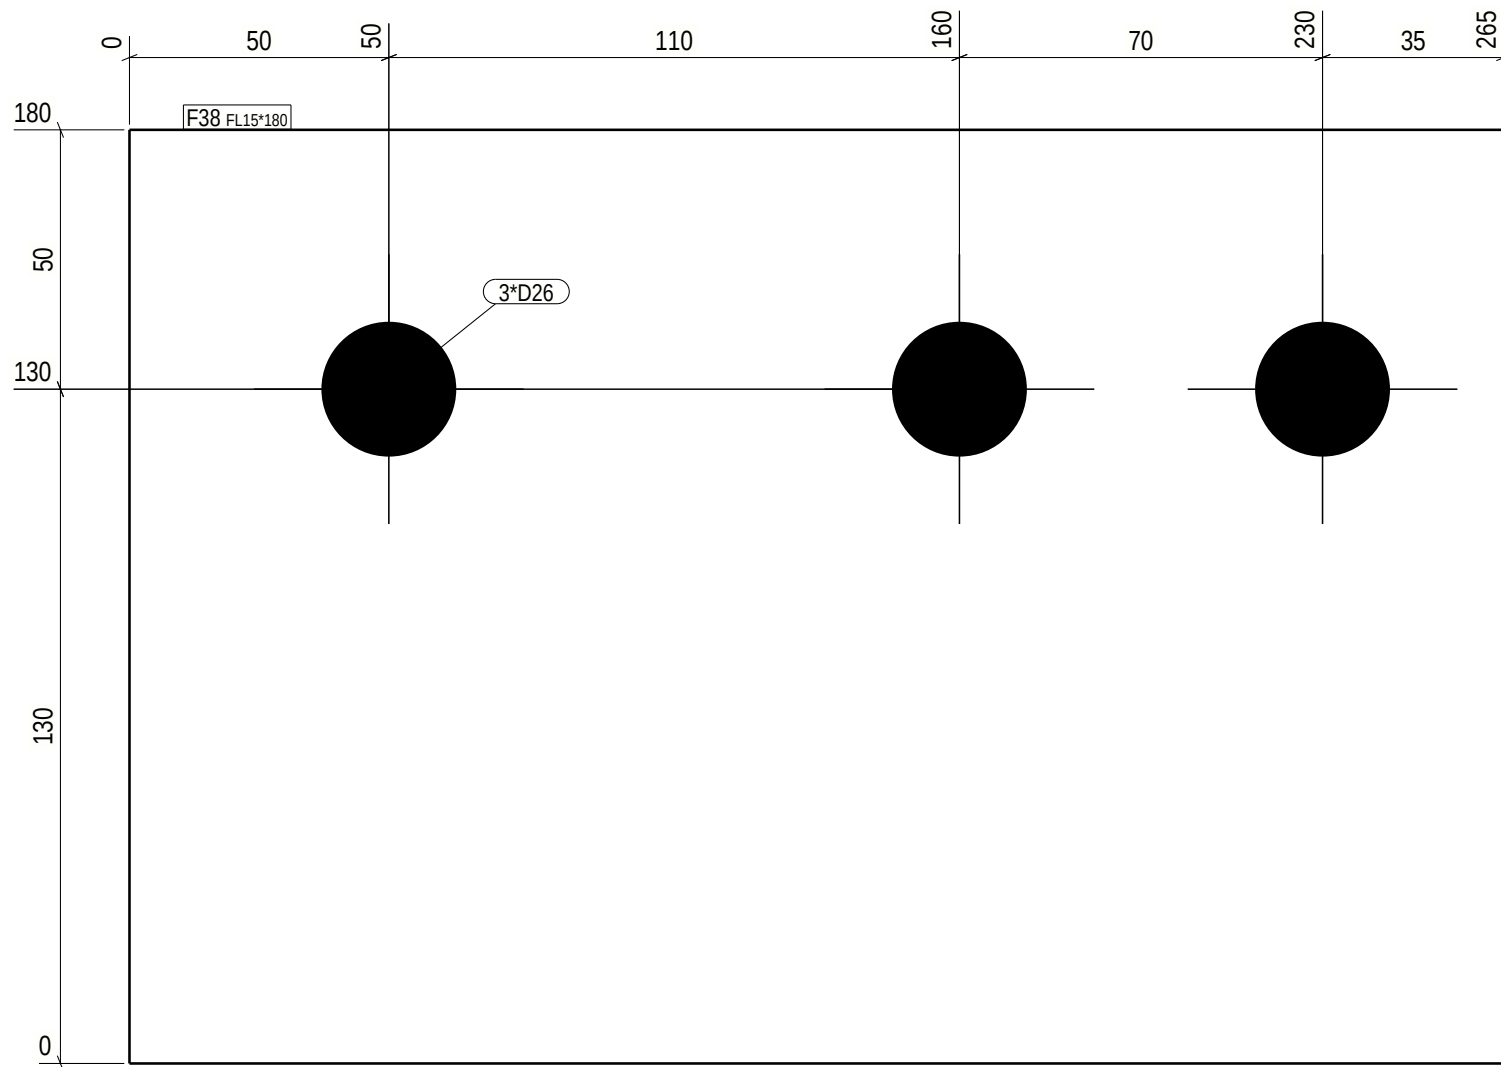

GENERAL NOTES:

For your safety, check weight before handling:
0-5kg Light 5-15kg Normal 15+kg Heavy

MATERIAL LIST FOR PART - F38 2 PARTS REQUIRED

POS. No.	PROFILE	No.	GRADE	L (mm)	AREA (m ²)	WEIGHT (kg)
F38	FL15*180	1	S355J2	265	0.1	5.6
TOTAL WEIGHT FOR		2	PARTS	11.2		

Execution class: EXC 2

No utilization on drawings = over 50%

V-SEAM
Utilization under 50%
EXC 2=> Acc. to process control
EXC 3=> 20% UT
Utilization over 50%
EXC 2=> 10% UT
EXC 3=> 20% UT

Part list	Qty.
DR	2

* o 3 0 4 8 0 - 1 *  **DS** *Stålkonstruktion* * W F 3 8 *

PROJECT	Akkasæter Lager- og vedlikeholdshall	PHASE	1 / Phase 1
MEMBER	Fladstål	QUANTITY:	2
REVISION		ISSUED:	03.11.2025
		DRAFTER:	ZLL
		BIM control:	SST
		PROJECT No	30480-1
		DRAWING No.	F.38