


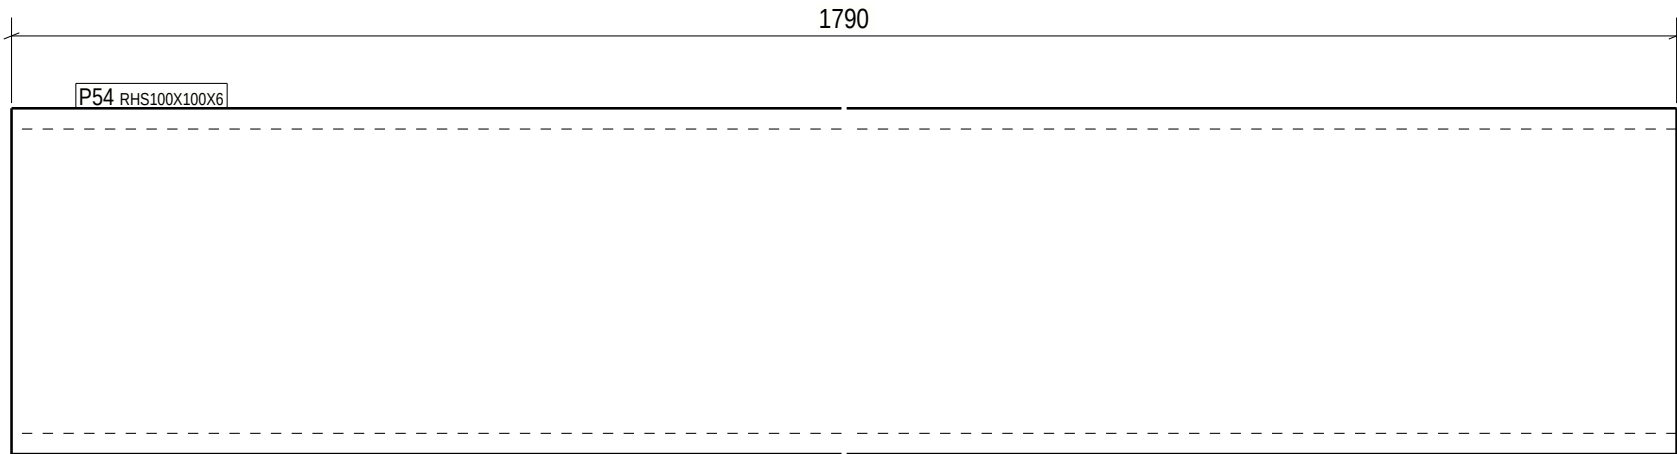

GENERAL NOTES:		For your safety, check weight before handling: 0-5kg Light 5-15kg Normal 15+kg Heavy				
MATERIAL LIST FOR PART - P54				3 PARTS REQUIRED		
POS. No.	PROFILE	No.	GRADE	L (mm)	AREA (m ²)	WEIGHT (kg)
P54	RHS100X100X6	1	S355J2H	1790	0.7	30.3 !!
TOTAL WEIGHT FOR				3	PARTS	90.8

Part list	Qty.
GS	3

Execution class: EXC 2		* o 3 0 4 8 0 - 1 *  DS <i>Skalkonstruktion</i> * WP 5 4 *			
No utilization on drawings = over 50%		PROJECT	Akkasæter Lager- og vedlikeholdshall	PHASE	1 / Phase 1
V-SEAM Utilization under 50% EXC 2=> Acc. to process control EXC 3=> 20% UT		MEMBER	Portomfatning	QUANTITY:	3
Utilization over 50% EXC 2=> 10% UT EXC 3=> 20% UT		REVISION		DRAFTER: BIM control:	ZLL SST
		ISSUED:	03.11.2025	DRAWING No.	P.54