


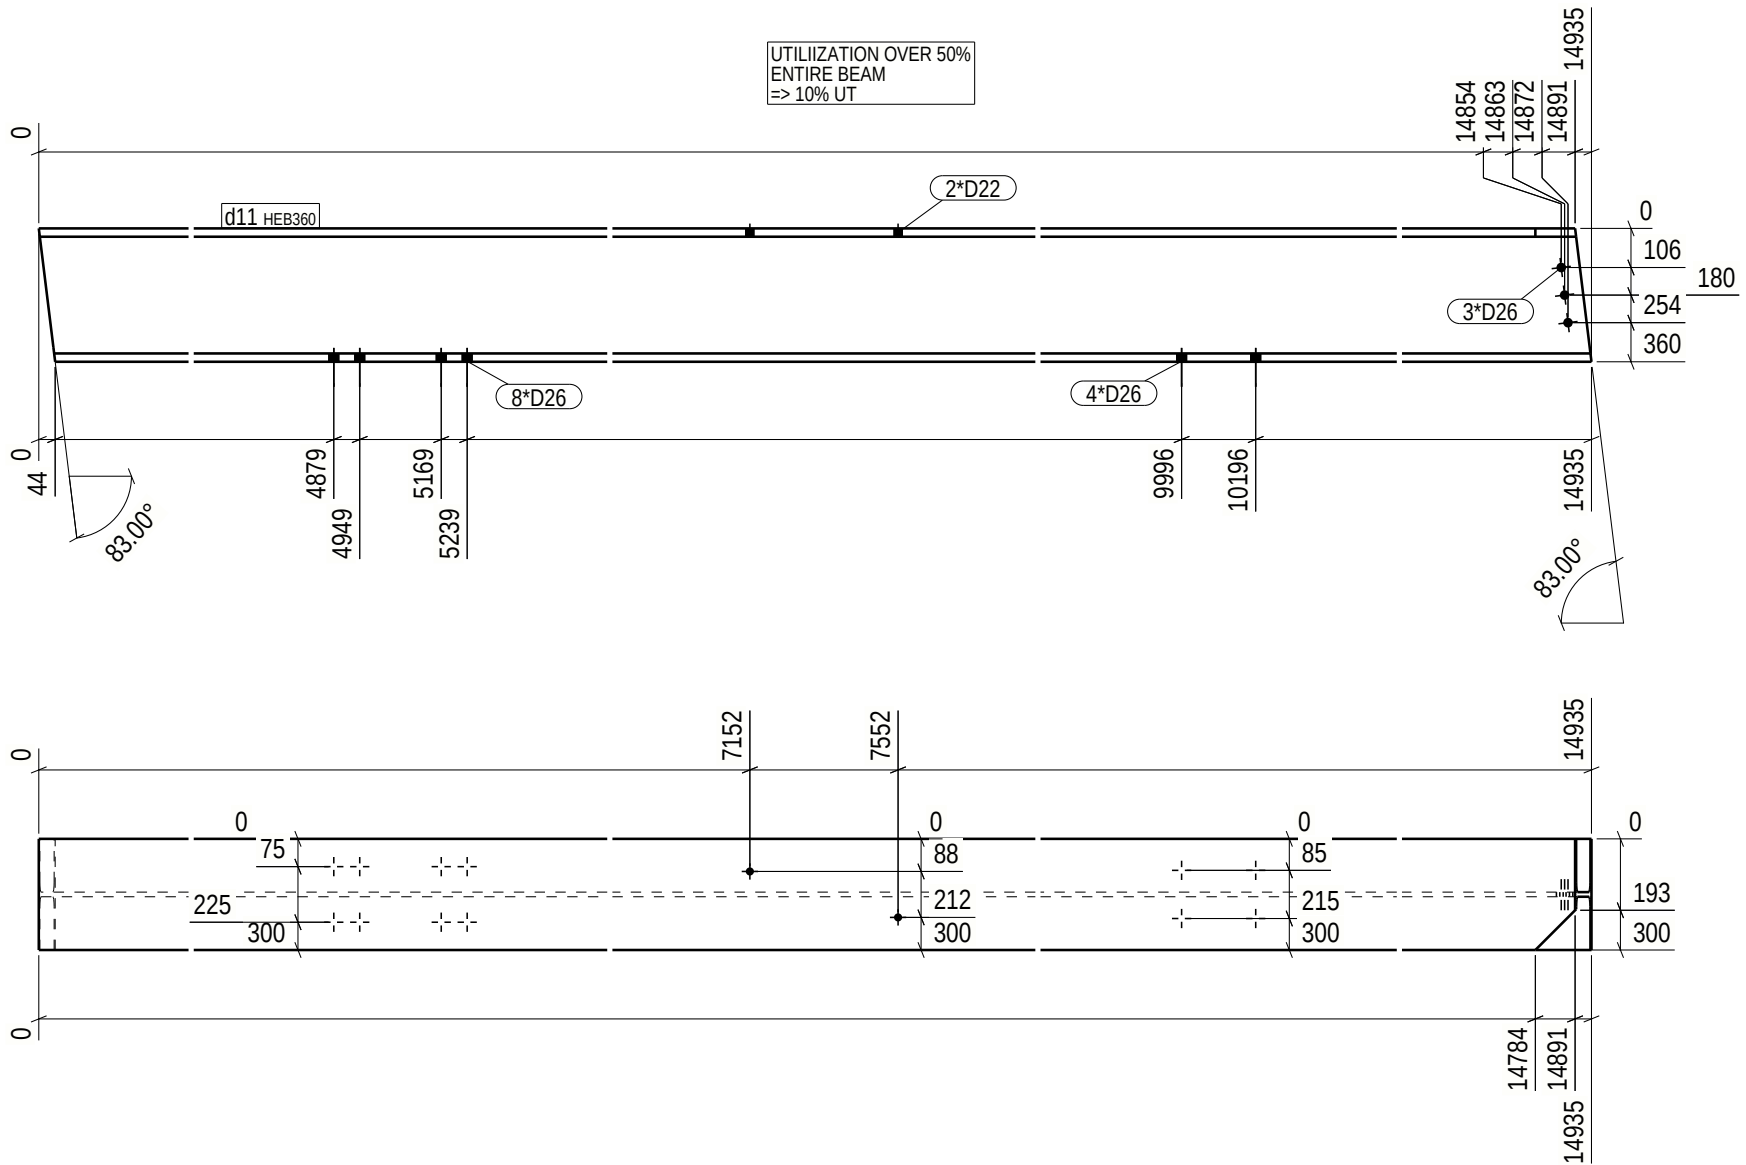

GENERAL NOTES:

For your safety, check weight before handling:
0-5kg Light 5-15kg Normal 15+kg Heavy

MATERIAL LIST FOR PART - d11

1 PARTS REQUIRED

POS. No.	PROFILE	No.	GRADE	L (mm)	AREA (m ²)	WEIGHT (kg)
d11	HEB360	1	S355J2	14935	27.6	2117.3 !!

TOTAL WEIGHT FOR 1 PARTS 2117.3

Part list	Qty.
DR	1

Execution class: EXC 2

No utilization on drawings = over 50%

V-SEAM
Utilization under 50%
EXC 2=> Acc. to process control
EXC 3=> 20% UT
Utilization over 50%
EXC 2=> 10% UT
EXC 3=> 20% UT

* o 3 0 4 8 0 - 1 *



DS Skanska Construction

* W d 1 1 *

PROJECT	Akkasæter Lager- og vedlikeholdshall		PHASE	1 / Phase 1	
MEMBER	Drager		QUANTITY:	1	PROJECT No 30480-1
REVISION		ISSUED: 05.11.2025	DRAFTER: ZLL	BIM control: SST	DRAWING No. d.11