


Tekla Structures

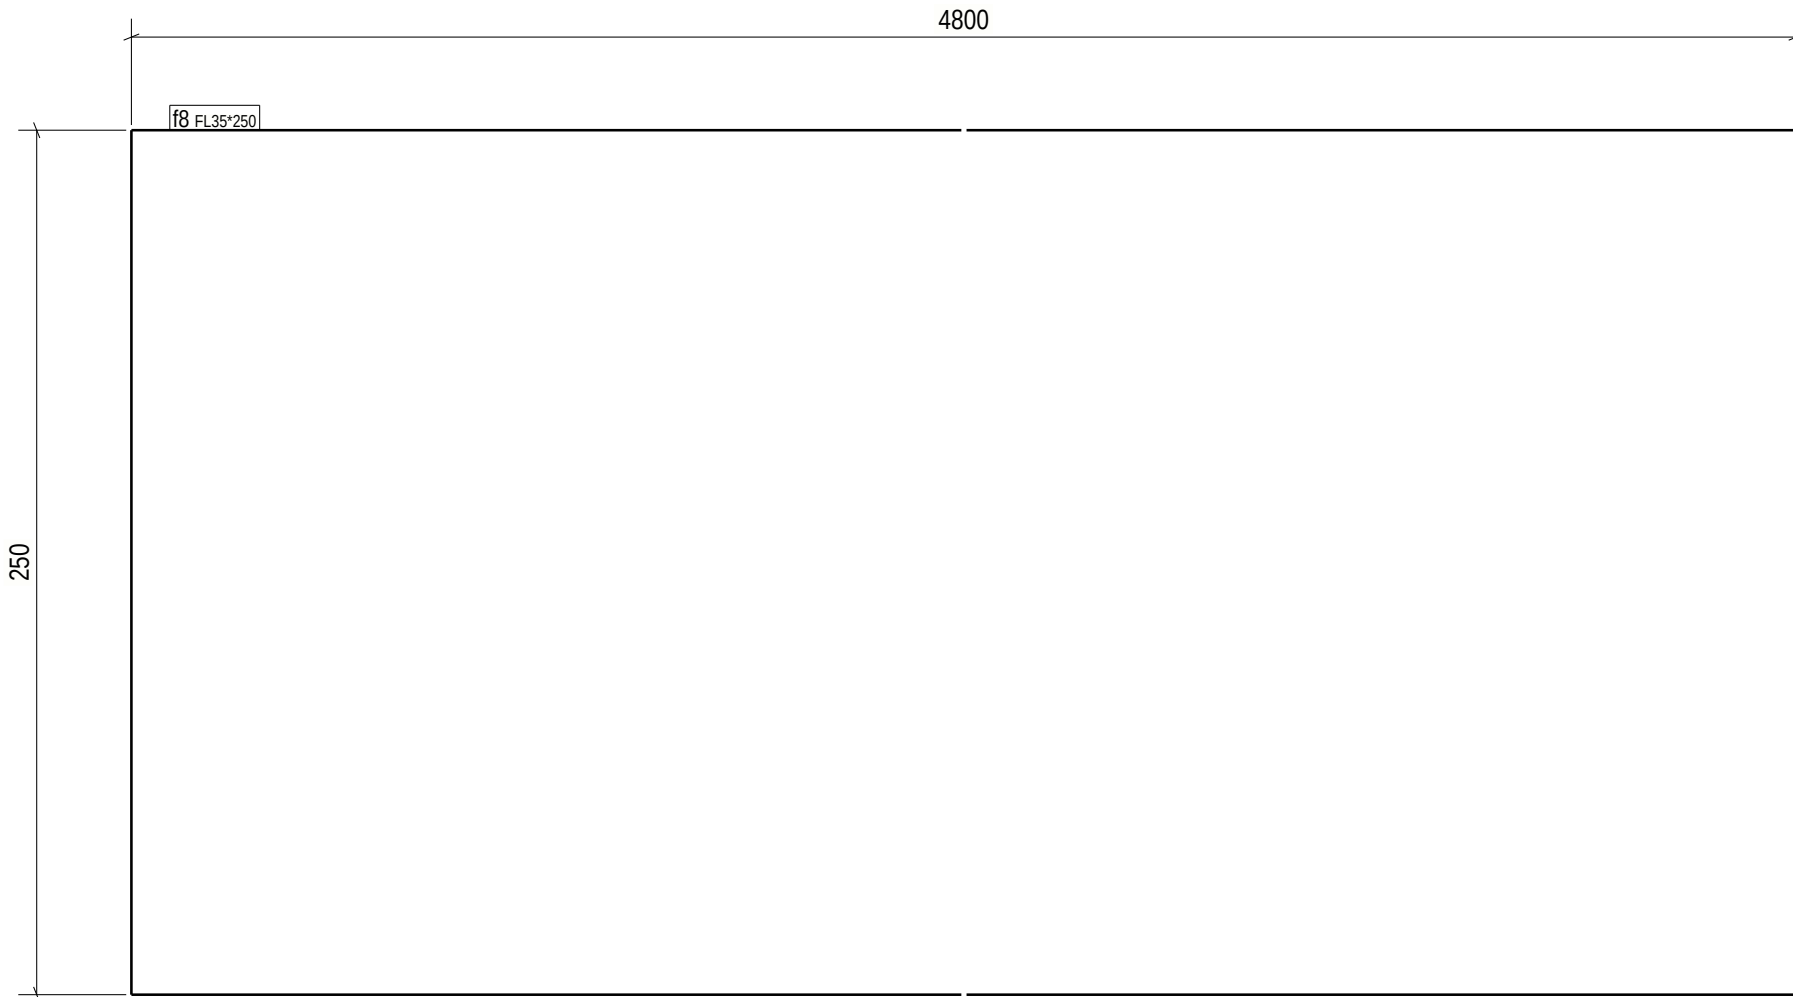

GENERAL NOTES:						
For your safety, check weight before handling:						
0-5kg Light 5-15kg Normal 15+kg Heavy						
MATERIAL LIST FOR PART - f8						
1 PARTS REQUIRED						
POS. No.	PROFILE	No.	GRADE	L (mm)	AREA (m ²)	WEIGHT (kg)
f8	FL35*250	1	S355J2	4800	2.8	329.7 !!
TOTAL WEIGHT FOR		1	PARTS	329.7		

Part list	Qty.
OB	1

Execution class: EXC 2		* o 3 0 4 8 0 - 1 *  DS <i>Skalkonstruktion</i> * W f 8 *			
No utilization on drawings = over 50%					
V-SEAM Utilization under 50% EXC 2=> Acc. to process control EXC 3=> 20% UT Utilization over 50% EXC 2=> 10% UT EXC 3=> 20% UT		PROJECT	Akkasæter Lager- og vedlikeholdshall		PHASE 1 / Phase 1
		MEMBER	HSQ		QUANTITY: 1 PROJECT No 30480-1
		REVISION		ISSUED: 03.11.2025	DRAFTER: ZLL BIM control: SST DRAWING No. f.8