


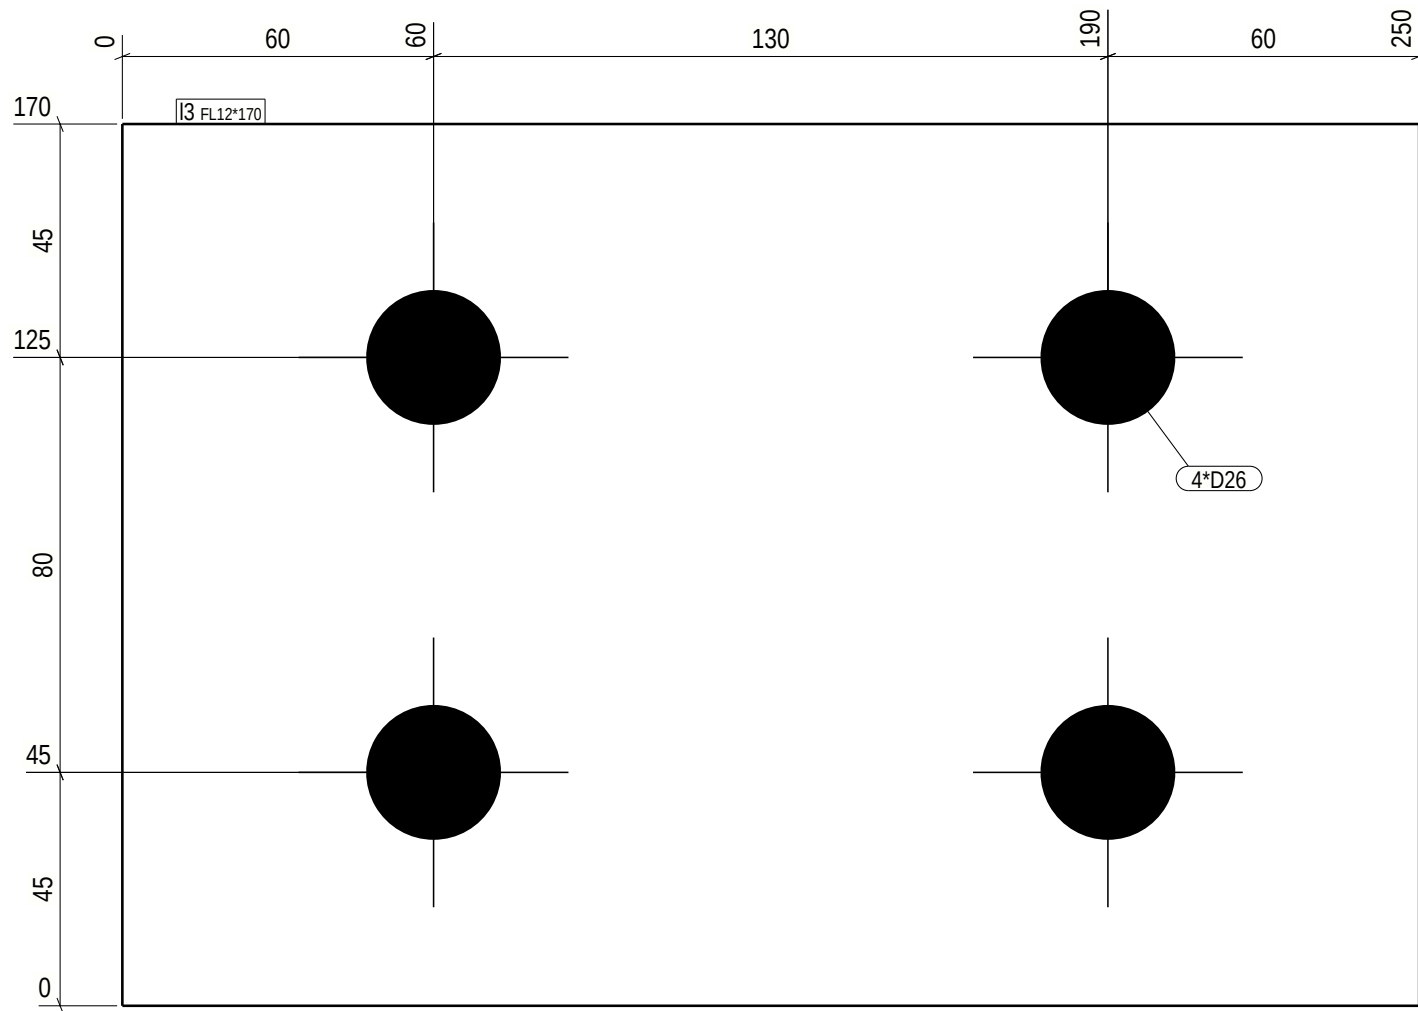

GENERAL NOTES:						
For your safety, check weight before handling:						
0-5kg Light 5-15kg Normal 15+kg Heavy						
MATERIAL LIST FOR PART - I3				32 PARTS REQUIRED		
POS. No.	PROFILE	No.	GRADE	L (mm)	AREA (m ²)	WEIGHT (kg)
I3	FL12*170	1	S355J2	250	0.1	4.0
TOTAL WEIGHT FOR				32 PARTS	128.1	

Part list	Qty.
LP	32

Execution class: EXC 2		* o 3 0 4 8 0 - 1 *  DS <i>Skalkonstruktion</i> * W I 3 *			
No utilization on drawings = over 50%					
V-SEAM Utilization under 50% EXC 2=> Acc. to process control EXC 3=> 20% UT Utilization over 50% EXC 2=> 10% UT EXC 3=> 20% UT		PROJECT	Akkasæter Lager- og vedlikeholdshall	PHASE	1 / Phase 1
		MEMBER	Løsdele	QUANTITY:	32
		REVISION		ISSUED:	03.11.2025
				DRAFTER:	ZLL
				BIM control:	SST
		PROJECT No			30480-1
		DRAWING No.			I.3