


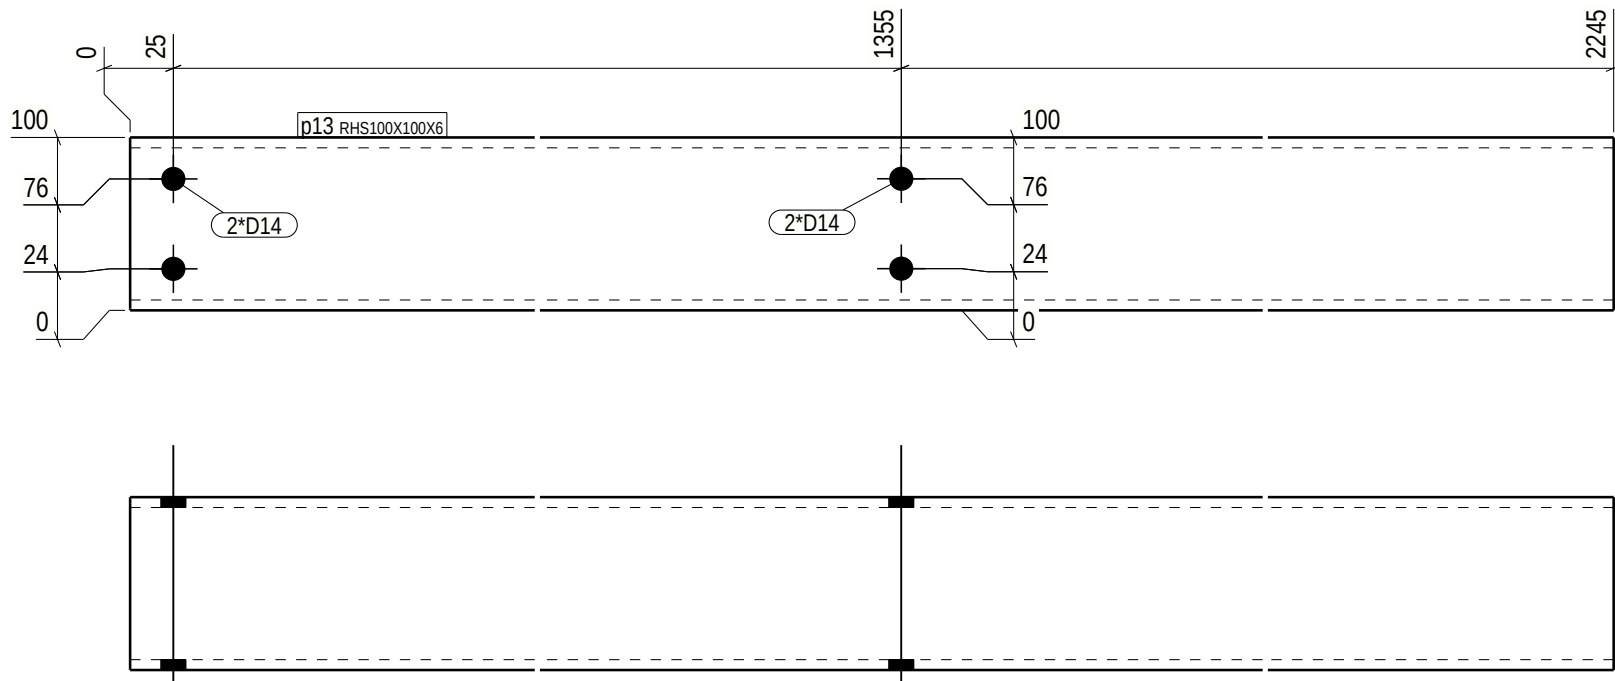

GENERAL NOTES:

For your safety, check weight before handling:
0-5kg Light 5-15kg Normal 15+kg Heavy

MATERIAL LIST FOR PART - p13

1 PARTS REQUIRED

POS. No.	PROFILE	No.	GRADE	L (mm)	AREA (m ²)	WEIGHT (kg)
p13	RHS100X100X6	1	S355J2H	2245	0.9	38.0 !!

TOTAL WEIGHT FOR 1 PARTS 38.0

Part list	Qty.
OP	1

Execution class: EXC 2

No utilization on drawings = over 50%

V-SEAM
Utilization under 50%
EXC 2=> Acc. to process control
EXC 3=> 20% UT
Utilization over 50%
EXC 2=> 10% UT
EXC 3=> 20% UT

* o 3 0 4 8 0 - 1 *  **DS** *Skalkonstruktion* * W p 1 3 *

PROJECT	Akkasæter Lager- og vedlikeholdshall	PHASE	1 / Phase 1
MEMBER	Portomfatning	QUANTITY:	1
REVISION	ISSUED: 03.11.2025	DRAFTER:	ZLL
		BIM control:	SST
		PROJECT No	30480-1
		DRAWING No.	p.13